


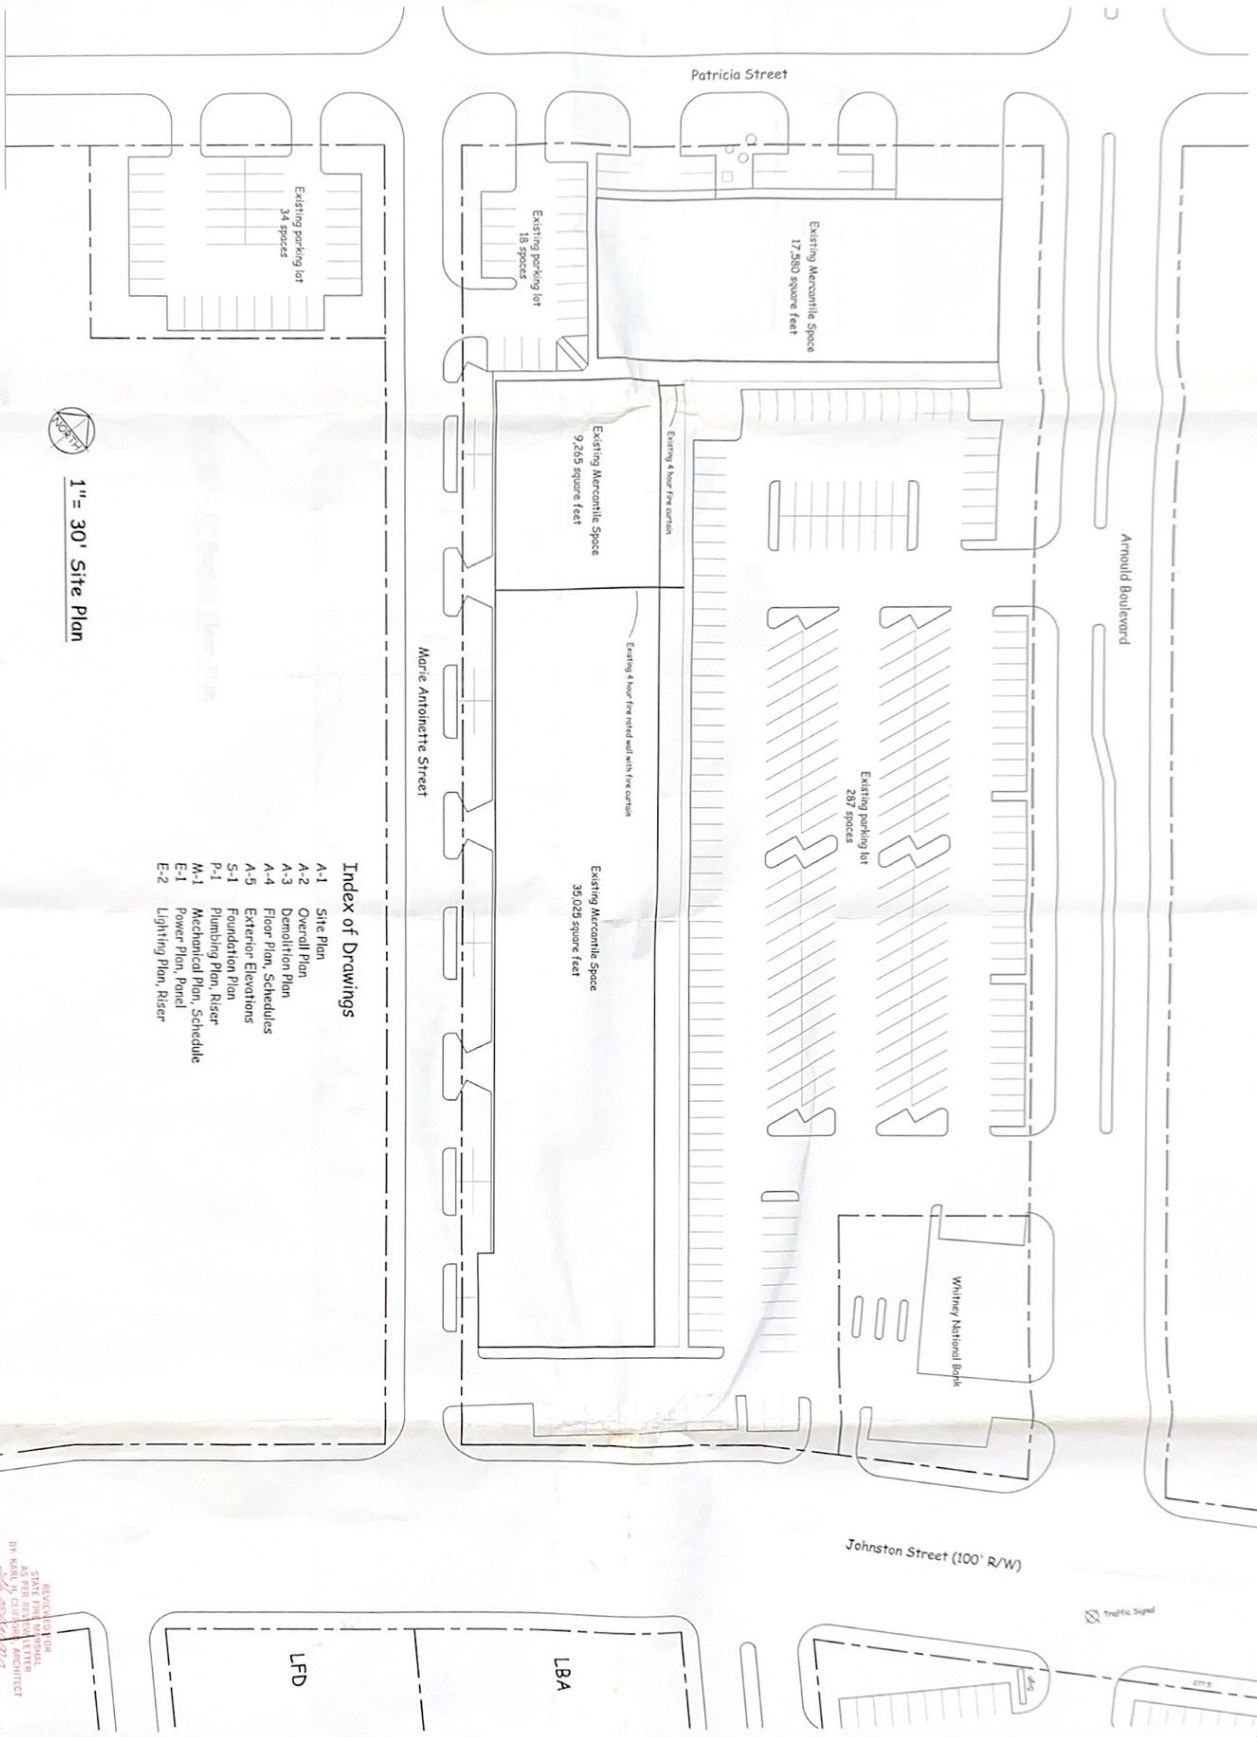

1" = 30' Site Plan

- Index of Drawings**
- A-1 Site Plan
 - A-2 Overall Plan
 - A-3 Demolition Plan
 - A-4 Floor Plan, Schedules
 - A-5 Exterior Elevations
 - S-1 Foundation Plan
 - P-1 Plumbing Plan, Riser
 - M-1 Mechanical Plan, Schedule
 - E-1 Power Plan, Panel
 - E-2 Lighting Plan, Riser

REVISION FOR
STAMPED AND SIGNED
AS PER CITY LETTER
BY K&L H. CLAYTON, ARCHITECT
3/27/08

Finish Out of Existing Tenant Space:
The Boulevard Shopping Center
Arnold Boulevard & Johnston Street
Lafayette, LA

William J. Crist, AIA
201 Alva Road
Youngville, LA 70592
(337) 856-6812

DATE 11/14/07	BY K&L H. CLAYTON
DESIGN 04/02/2007	BY K&L H. CLAYTON
DATE May 6, 2007	BY K&L H. CLAYTON
SHEET A-1	OF 10