


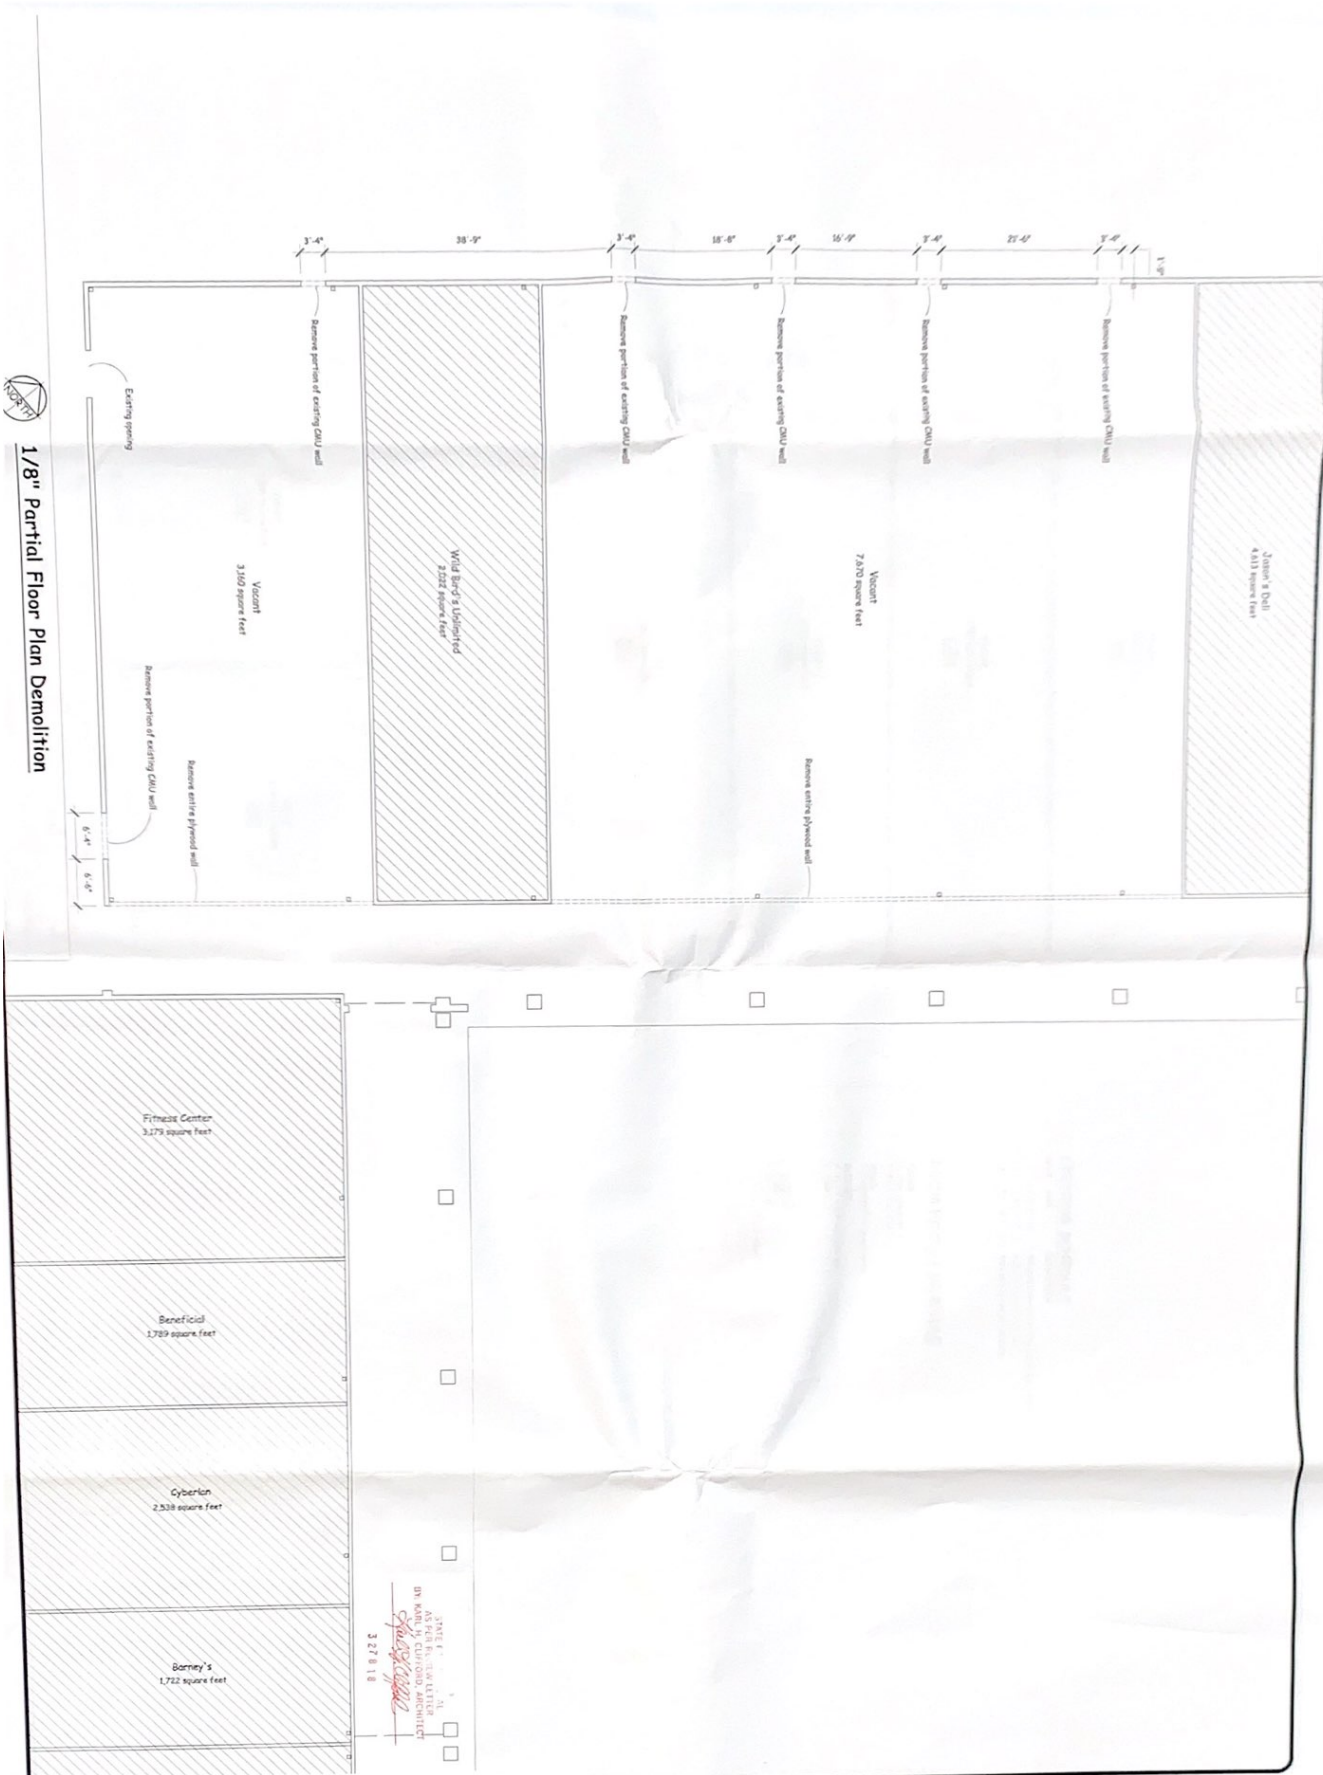

1/8" Partial Floor Plan Demolition

3	A-3	10
DATE	May 6, 2007	
DESIGNED BY	W. J. C.	
CHECKED BY	W. J. C.	
DATE	May 6, 2007	
DESIGNED BY	W. J. C.	
CHECKED BY	W. J. C.	

Finish Out of Existing Tenant Space:

The Boulevard Shopping Center

Arnold Boulevard & Johnston Street
Lafayette, LA

William J. Chat, AIA
201 Alva Road
Youngville, LA 70592
(337) 856-6812

DATE	May 6, 2007
DESIGNED BY	W. J. C.
CHECKED BY	W. J. C.
DATE	May 6, 2007
DESIGNED BY	W. J. C.
CHECKED BY	W. J. C.