


FIRST FLOOR PLAN - SALES AREA

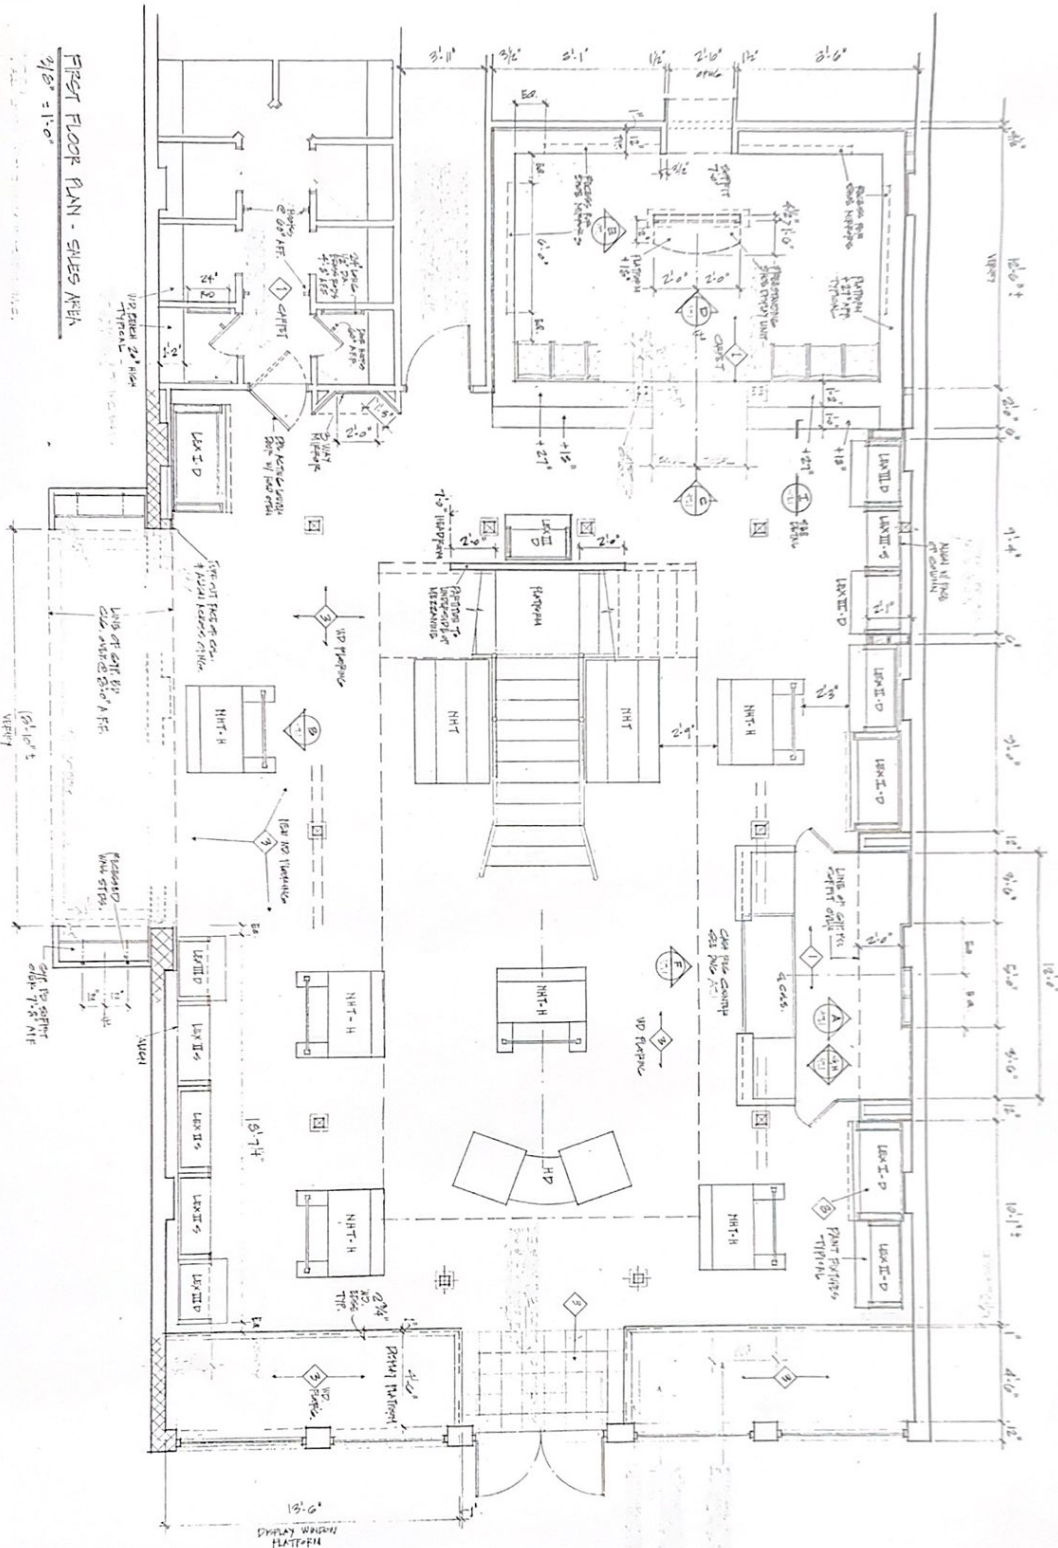

PROPOSED ALTERNATIONS TO RETAIL STORE FOR

101 ARNOULD BOULEVARD
LAFAYETTE, LOUISIANA

Stephen W. Schwartz, AIA
Architect / Planner

316 Eisenhower Parkway
Livingston, N.J. 07039
(201) 964-9797 • Fax (201) 535-0565

NJ 10664 • NY 11347 • PA B-9287
MA 6106 • CT 5744 • DE 5489 • FL 7178

JOE MO 9/9/4
SCALE AS 10000
DRAWN BY JCS
CHECKED BY GJS
DATE 6/4/93

A2.2

DRAWING NUMBER

CV