


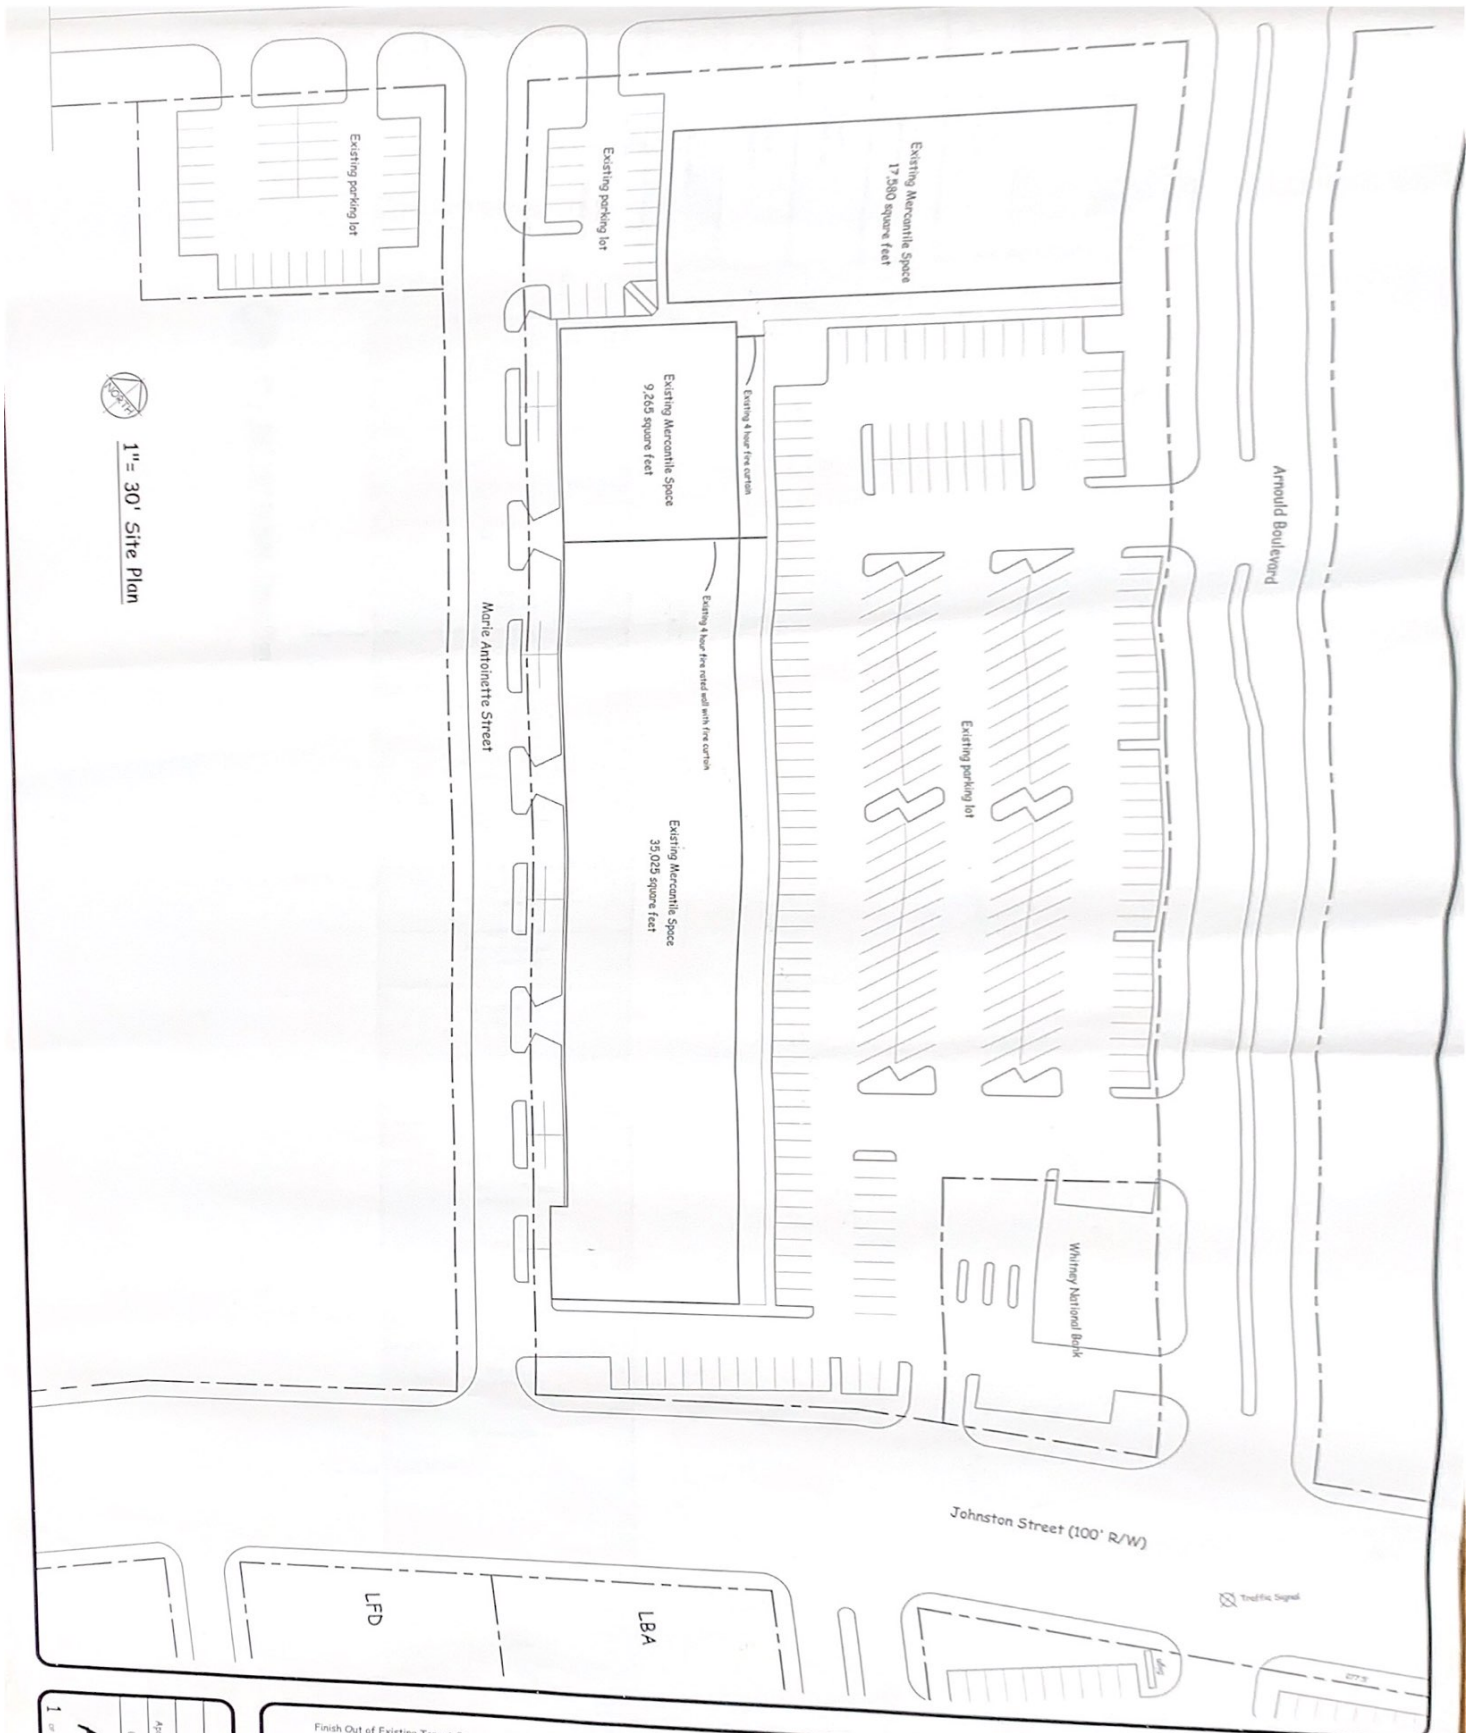

1" = 30' Site Plan

1	A-1
2	
3	
Finish Out of Existing Tenant Space:
The Boulevard Shopping Center
 Arnold Boulevard & Johnston Street
 Lafayette, LA


William J. Crut, AIA
 201 Alva Road
 Youngsville, LA 70592



1" = 20' - 0" Partial Floor Plan

4 hour fire wall

2 hour fire wall

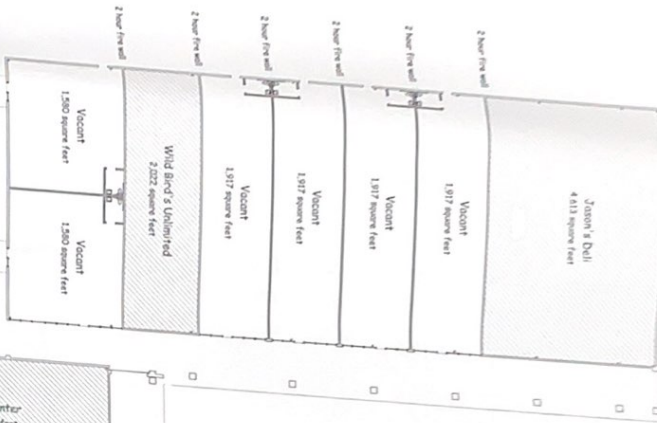

2 of 2
A-2



DATE: April 18, 2007
DRAWN BY: J. J. J.
CHECKED BY: J. J. J.
SHEET: 2 of 2

Finish Out of Existing Tenant Space
The Boulevard Shopping Center
Arnold Boulevard & Johnston Street

William J. Crist, AIA



1/8" Partial Floor Plan Demolition

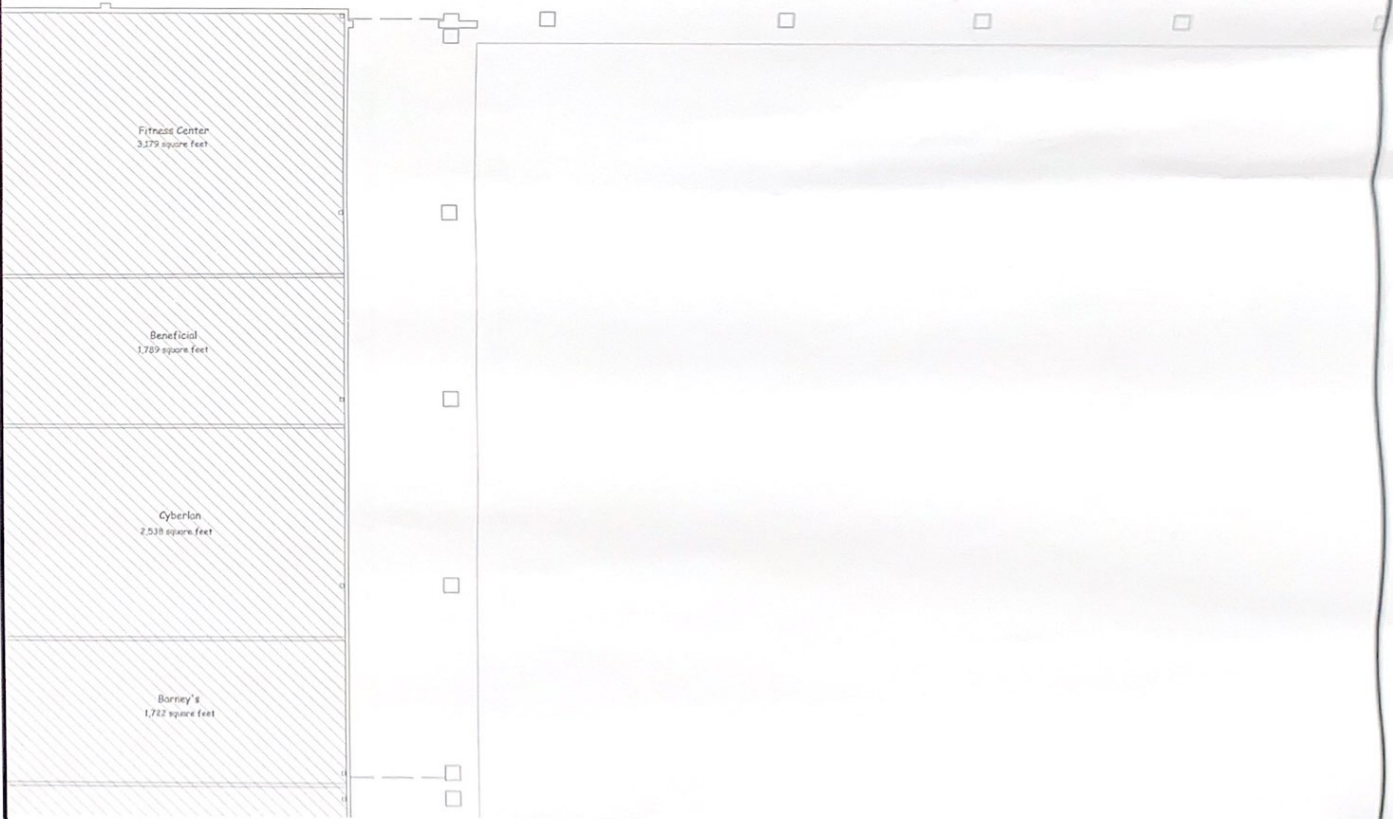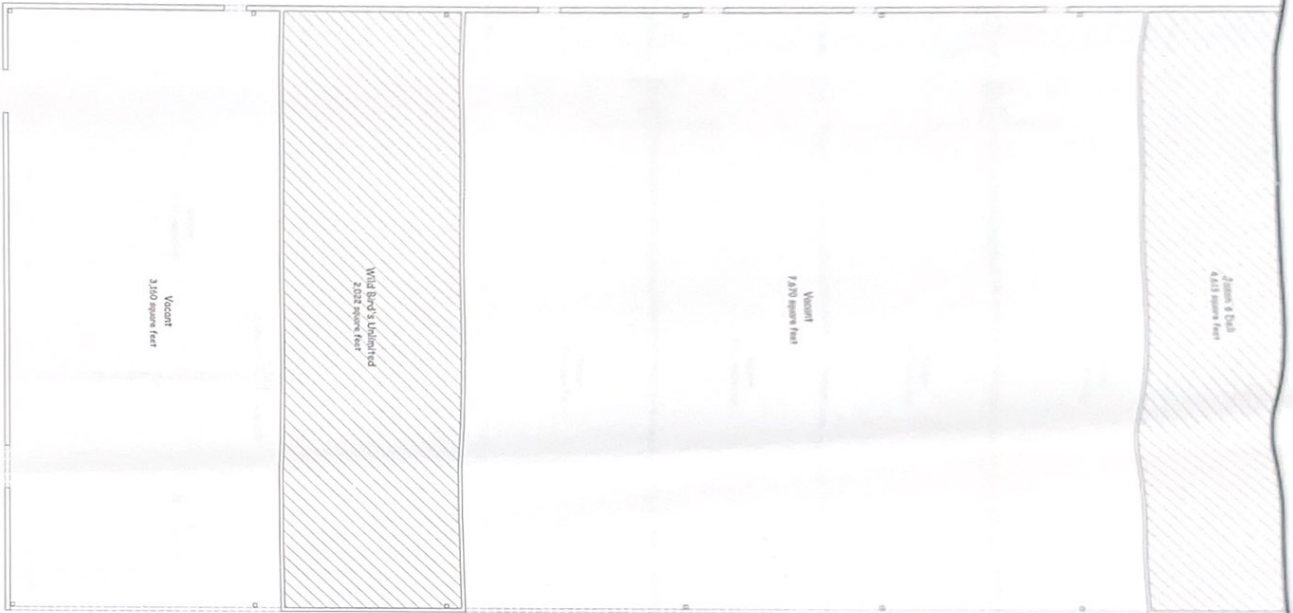

3 of 2
A-3
DATE: 04/18/07
BY: J. C.
PROJECT: 000000
REVISION: 000000

Finish Out of Existing Tenant Space:
The Boulevard Shopping Center
Arnold Boulevard & Johnston Street
Lafayette, LA

William J. Crain, AIA
201 Alms Road
Youngsville, LA 70592
(337) 856-6822







William J. Crist, AT

The Boulevard Shopping Center
Arnold Boulevard & Johnston Street
Lafayette, LA


DATE	APRIL 18, 2007
ORDERED	020225
BY	4-4
BY	4-4

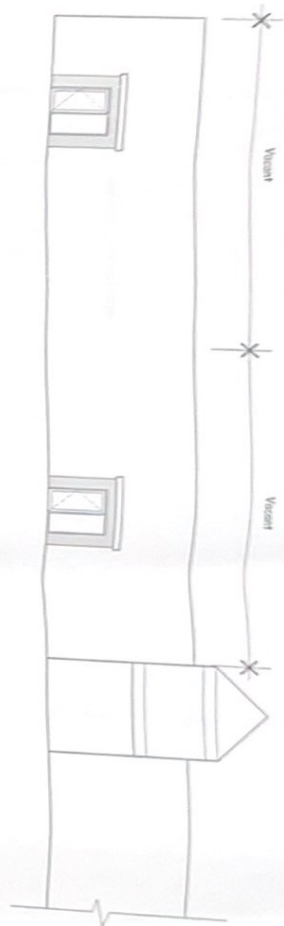

1/8" Marie Antoinette Elevation (Option 2)

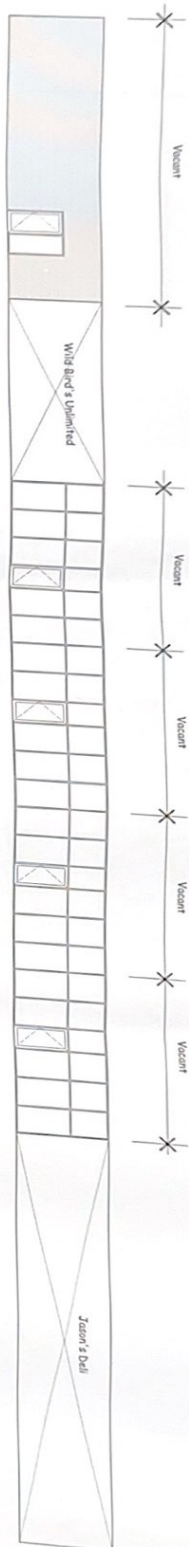

1/8" Front Elevation (Option 2)

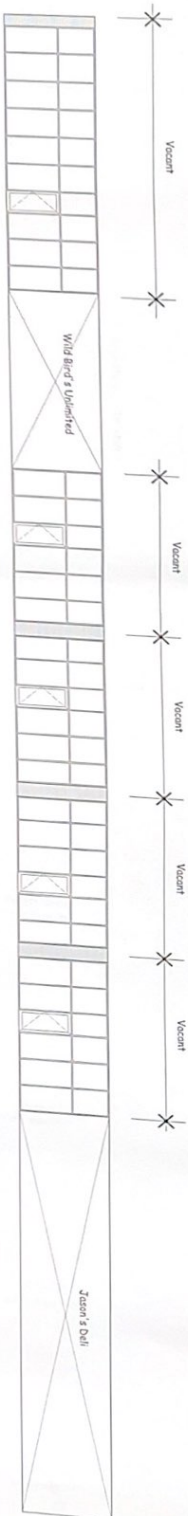

1/8" Front Elevation (Option 1)

