


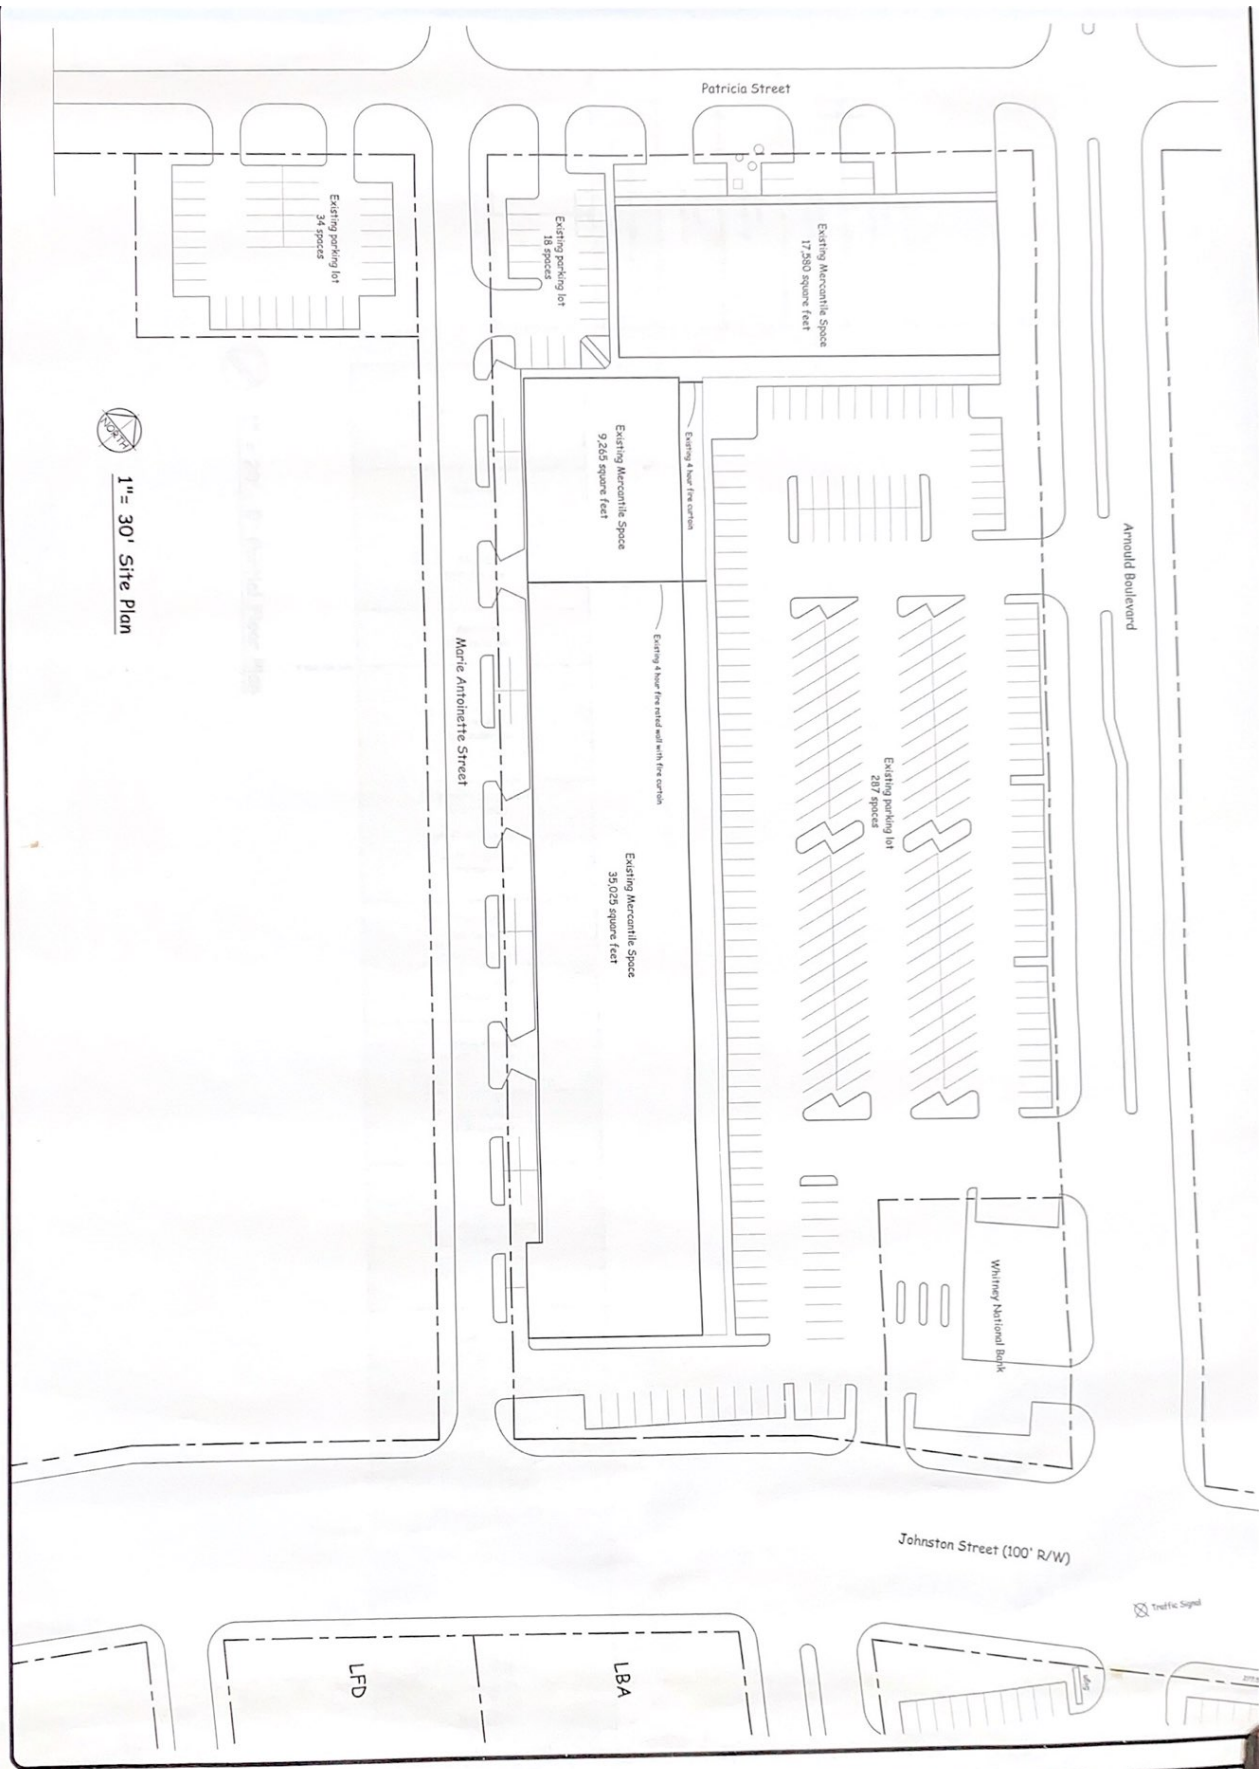

1" = 30' Site Plan

1	of 2	SHEET
A-1		
ISSUED	W.J.C.	
DESIGNED		
DATE	APRIL 24, 2007	
PROJECT NO.	04022007	
SHEET		

Finish Out of Existing Tenant Space:
The Boulevard Shopping Center
 Arnold Boulevard & Johnston Street
 Lafayette, LA

William J. Crist, AIA
 201 Alva Road
 Youngville, LA 70592
 (337) 856-6812




Arnold Boulevard & Johnston Street
Lafayette, LA

DEAN
W J C
D-BOXES
DATE
April 18, 2007
JOB NO.
020225
SHEET
A-2
2 OF 2 SHEETS



1/8" Partial Floor Plan Demolition

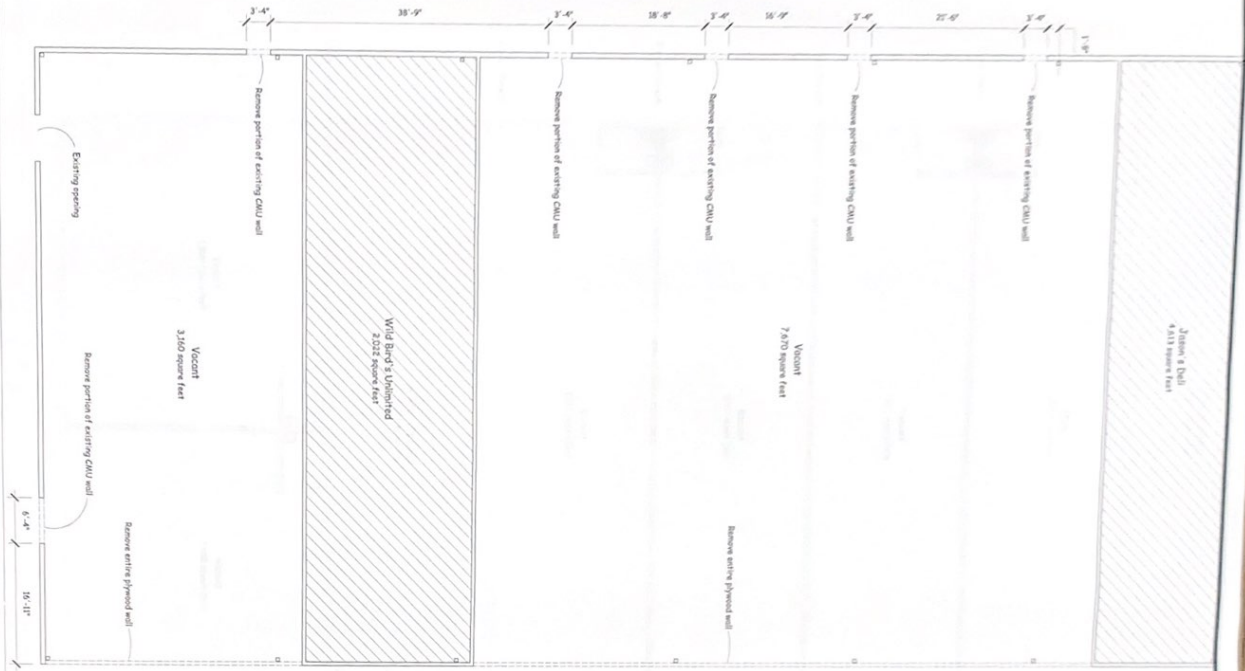

Fitness Center
3,379 square feet

Beneficial
1,729 square feet

Cyberlon
2,538 square feet

Barney's
1,752 square feet

Finish Out of Existing Tenant Space:

The Boulevard Shopping Center

Arnold Boulevard & Johnston Street
Lafayette, LA

William J. Crist, AIA

201 Alca Road

Youngville, LA 70592



(337) 856-6812

DATE	W 2 C
DATE	03/03/07
DATE	April 24, 2007
DATE	03/03/07
DATE	03/03/07
DATE	03/03/07
DATE	03/03/07
DATE	03/03/07
DATE	03/03/07
DATE	03/03/07
DATE	03/03/07

3 of 2
A-3



1/8" Floor Plan

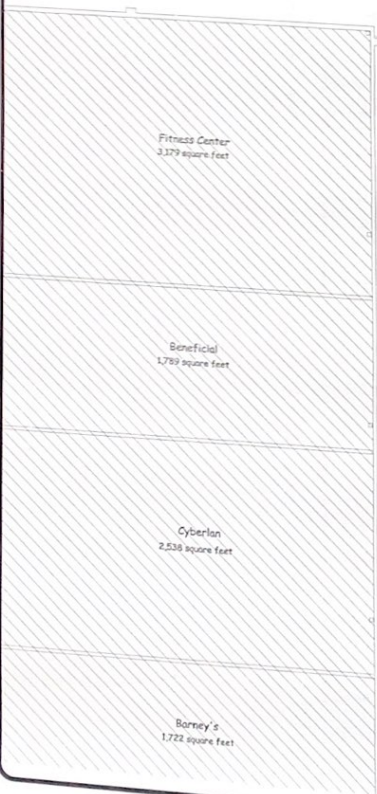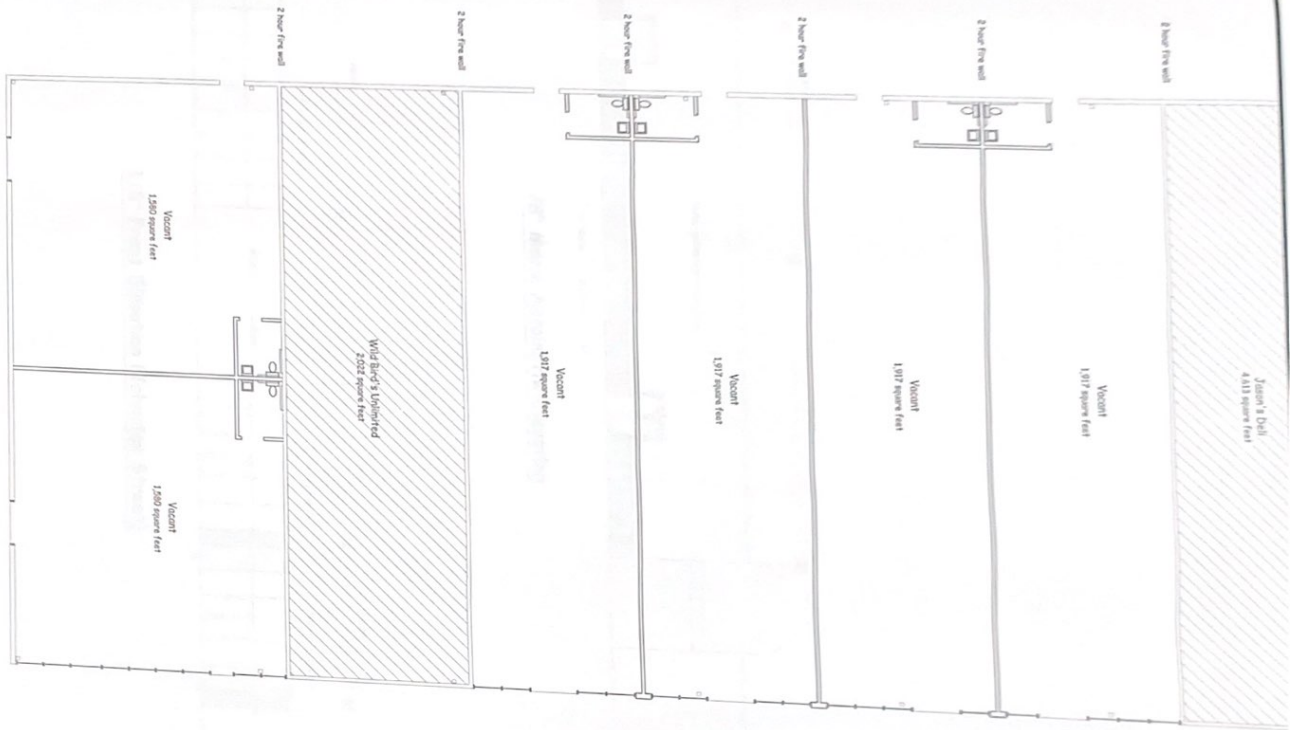


4	A-4	APR 14, 2007	W J C	020225	4 of 2
---	-----	--------------	-------	--------	--------


Finish Out of Existing Tenant Space:
The Boulevard Shopping Center
Arnold Boulevard & Johnston Street
Lafayette, LA



William J. Crist, AIA

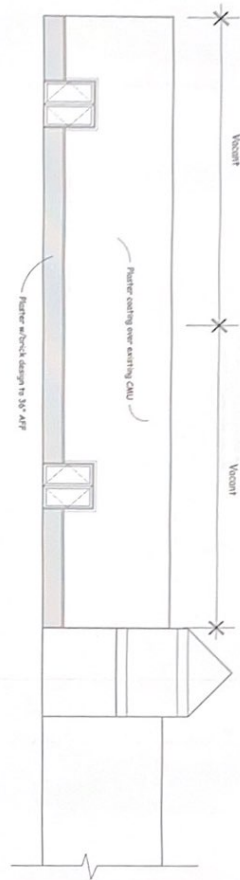

1/8" Marie Antoinette Elevation

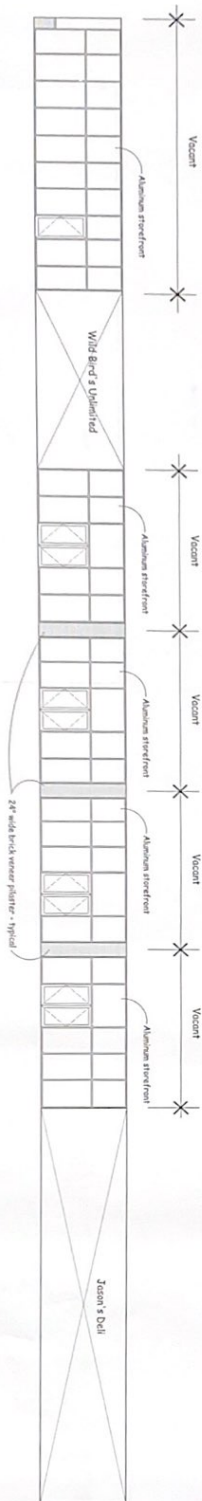

1/8" Front Elevation (Johnston Street)



William J. Crist, AIA
201 Alva Road
Youngsville, LA 70592
(337) 856-6812



Finish Out of Existing Tenant Space:
The Boulevard Shopping Center
Arnold Boulevard & Johnston Street
Lafayette, LA

SCALE:
W. J. C.
DATE: 04/24/07
BY: WJC
PROJECT: 2002225

A-5
5



1/8" Foundation Plan

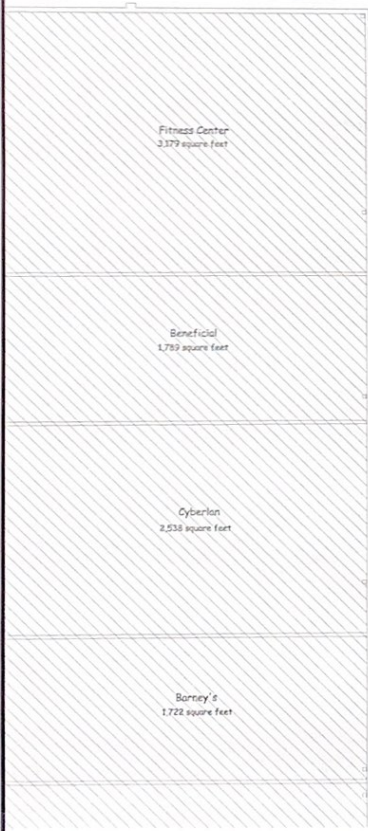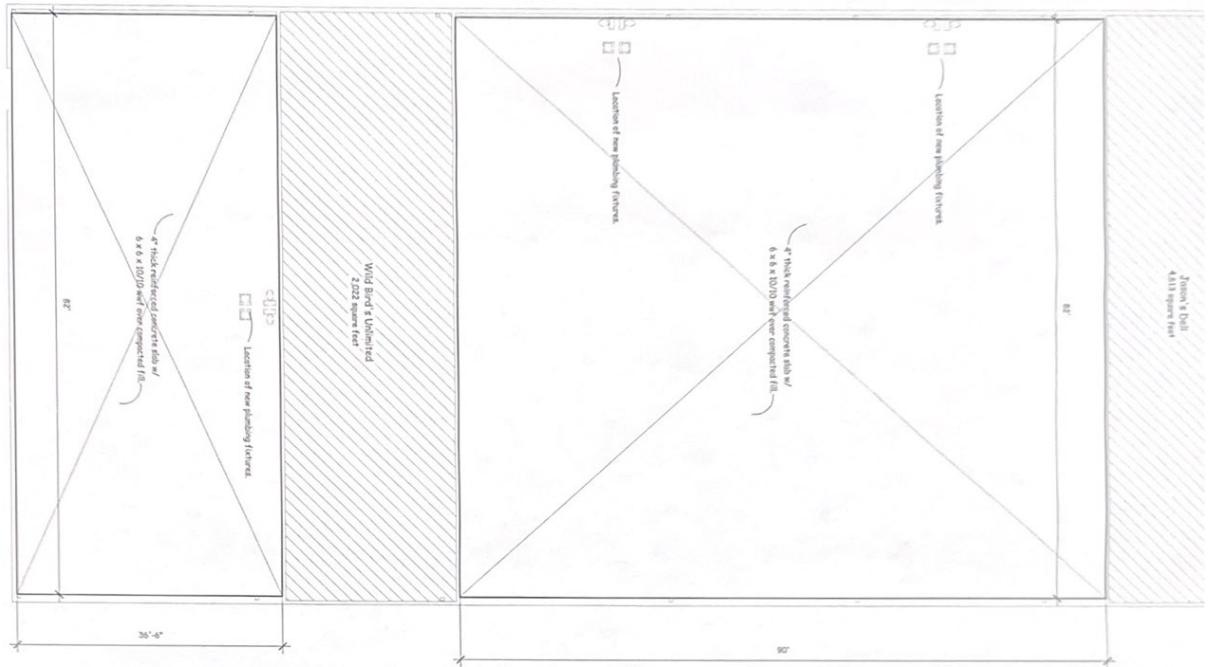

6 of 2
A-6
Sheet
020225
22940
April 18, 2007
WJC
Sketch

Finish Out of Existing Tenant Space:
The Boulevard Shopping Center
Arnold Boulevard & Johnston Street
Lafayette, LA



William J. Crist, AIA
201 Alva Road
Youngville, LA 70592
(337) 856-6812