


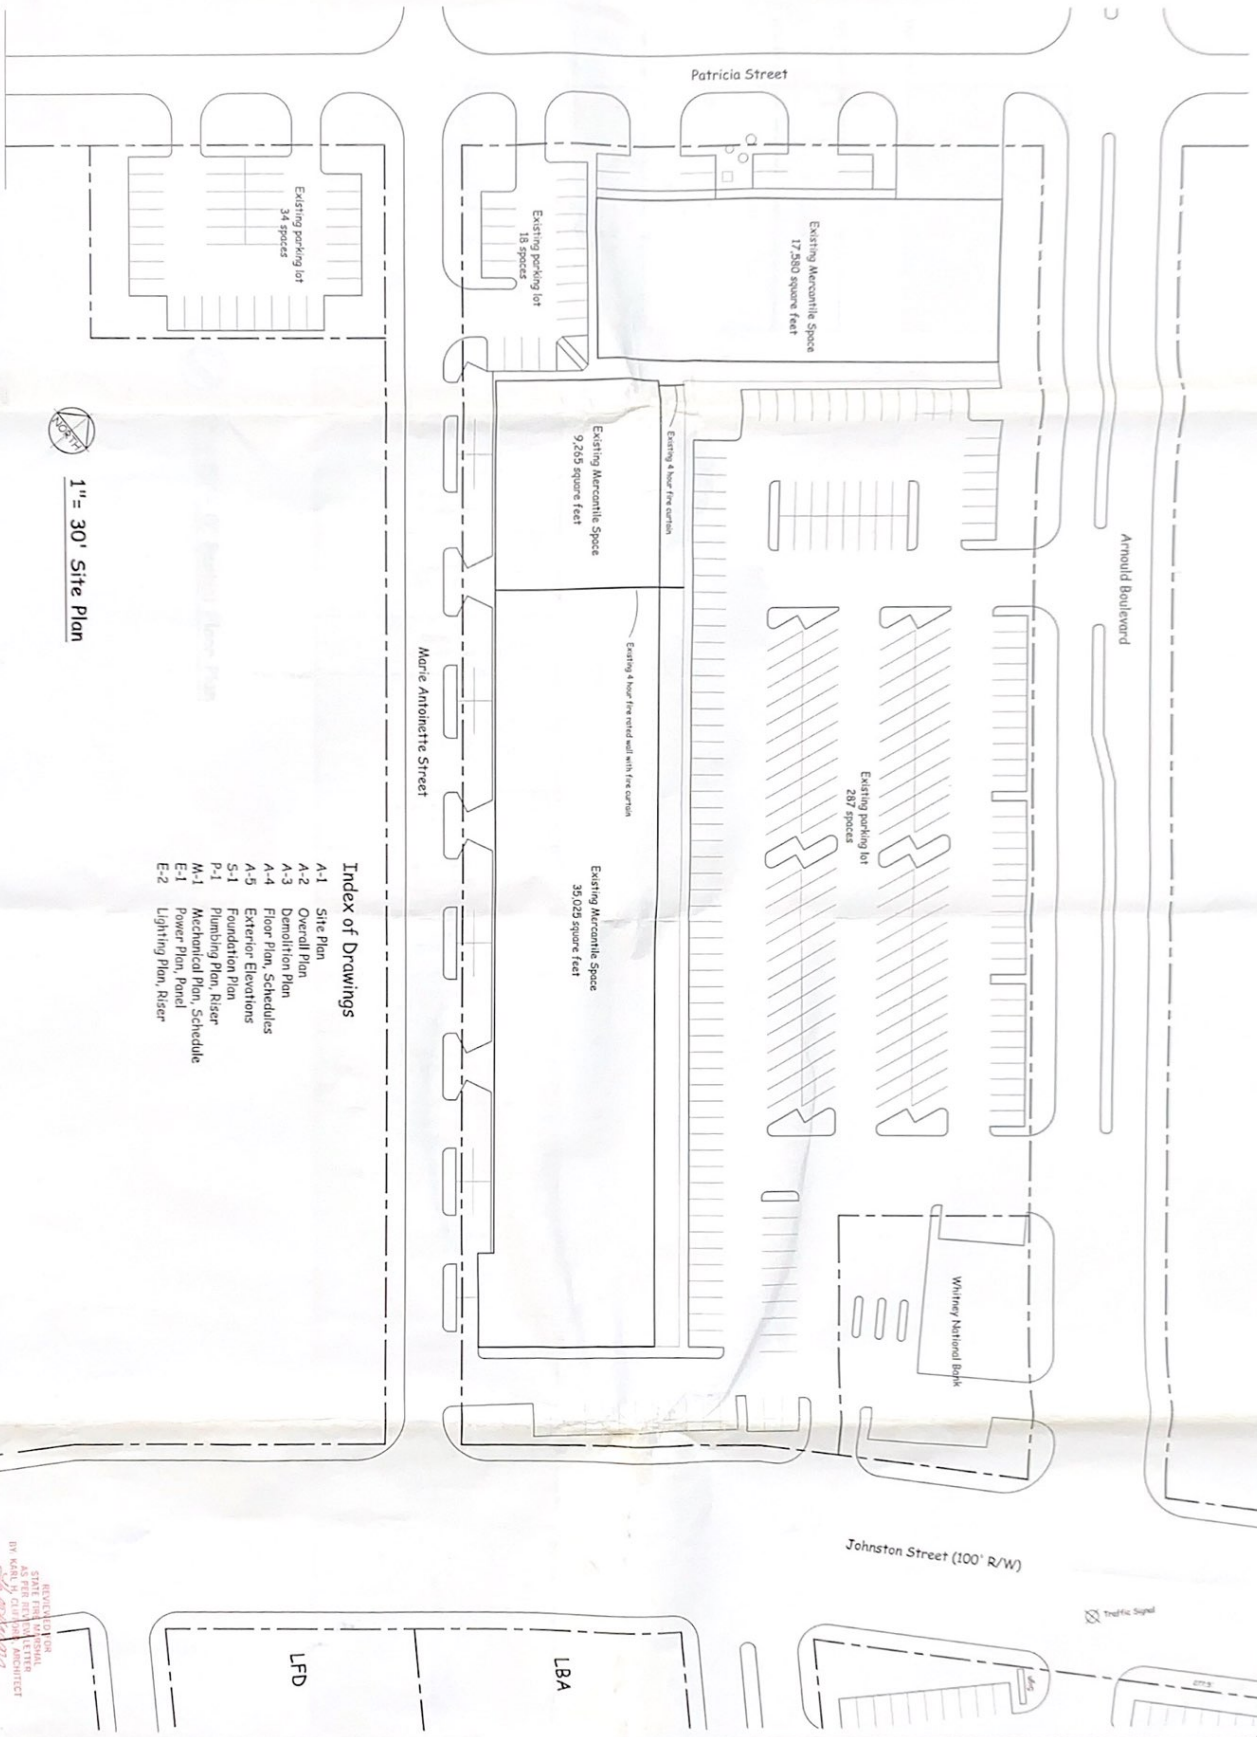

1" = 30' Site Plan

- Index of Drawings**
- A-1 Site Plan
 - A-2 Overall Plan
 - A-3 Demolition Plan
 - A-4 Floor Plan, Schedules
 - A-5 Exterior Elevations
 - S-1 Foundation Plan
 - P-1 Plumbing Plan, Riser
 - M-1 Mechanical Plan, Schedule
 - E-1 Power Plan, Panel
 - E-2 Lighting Plan, Riser

REVISION FOR
STAMPED AND SIGNED
AS PER CITY LETTER
BY K&L H. CLAYTON, ARCHITECT
3/27/08

Finish Out of Existing Tenant Space:
The Boulevard Shopping Center
Arnold Boulevard & Johnston Street
Lafayette, LA

William J. Crist, AIA
201 Alva Road
Youngville, LA 70592
(337) 856-6812



DATE 11/14/07	SCALE 1" = 30'
DESIGN C4022007	DATE May 6, 2007
SHEET A-1	1 OF 10



1" = 20' - 0" Partial Floor Plan

4 hour fire wall

2 hour fire wall

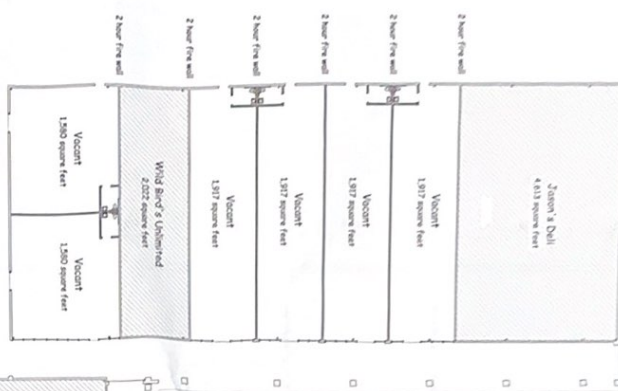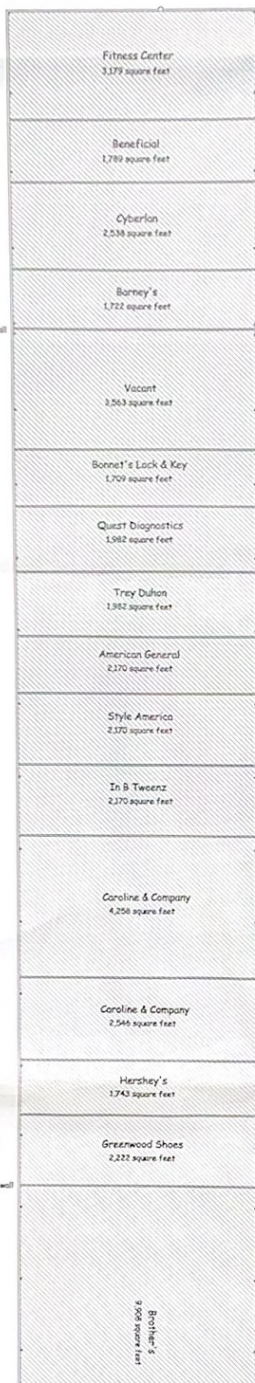


REVIEWED FOR
STATE FIRE MARSHAL
BY
3/27/81
3/27/81

2 of 10
A-2
DATE May 6, 2007
ISSUED 02/02/25
SHEET

Finish Out of Existing Tenant Space:
The Boulevard Shopping Center
Arnold Boulevard & Johnston Street
Lafayette, LA

William J. Crist, AIA
201 Alvo Road
Youngville, LA 70592
(337) 856-6812

REVISIONS
NO.
DATE
DESCRIPTION

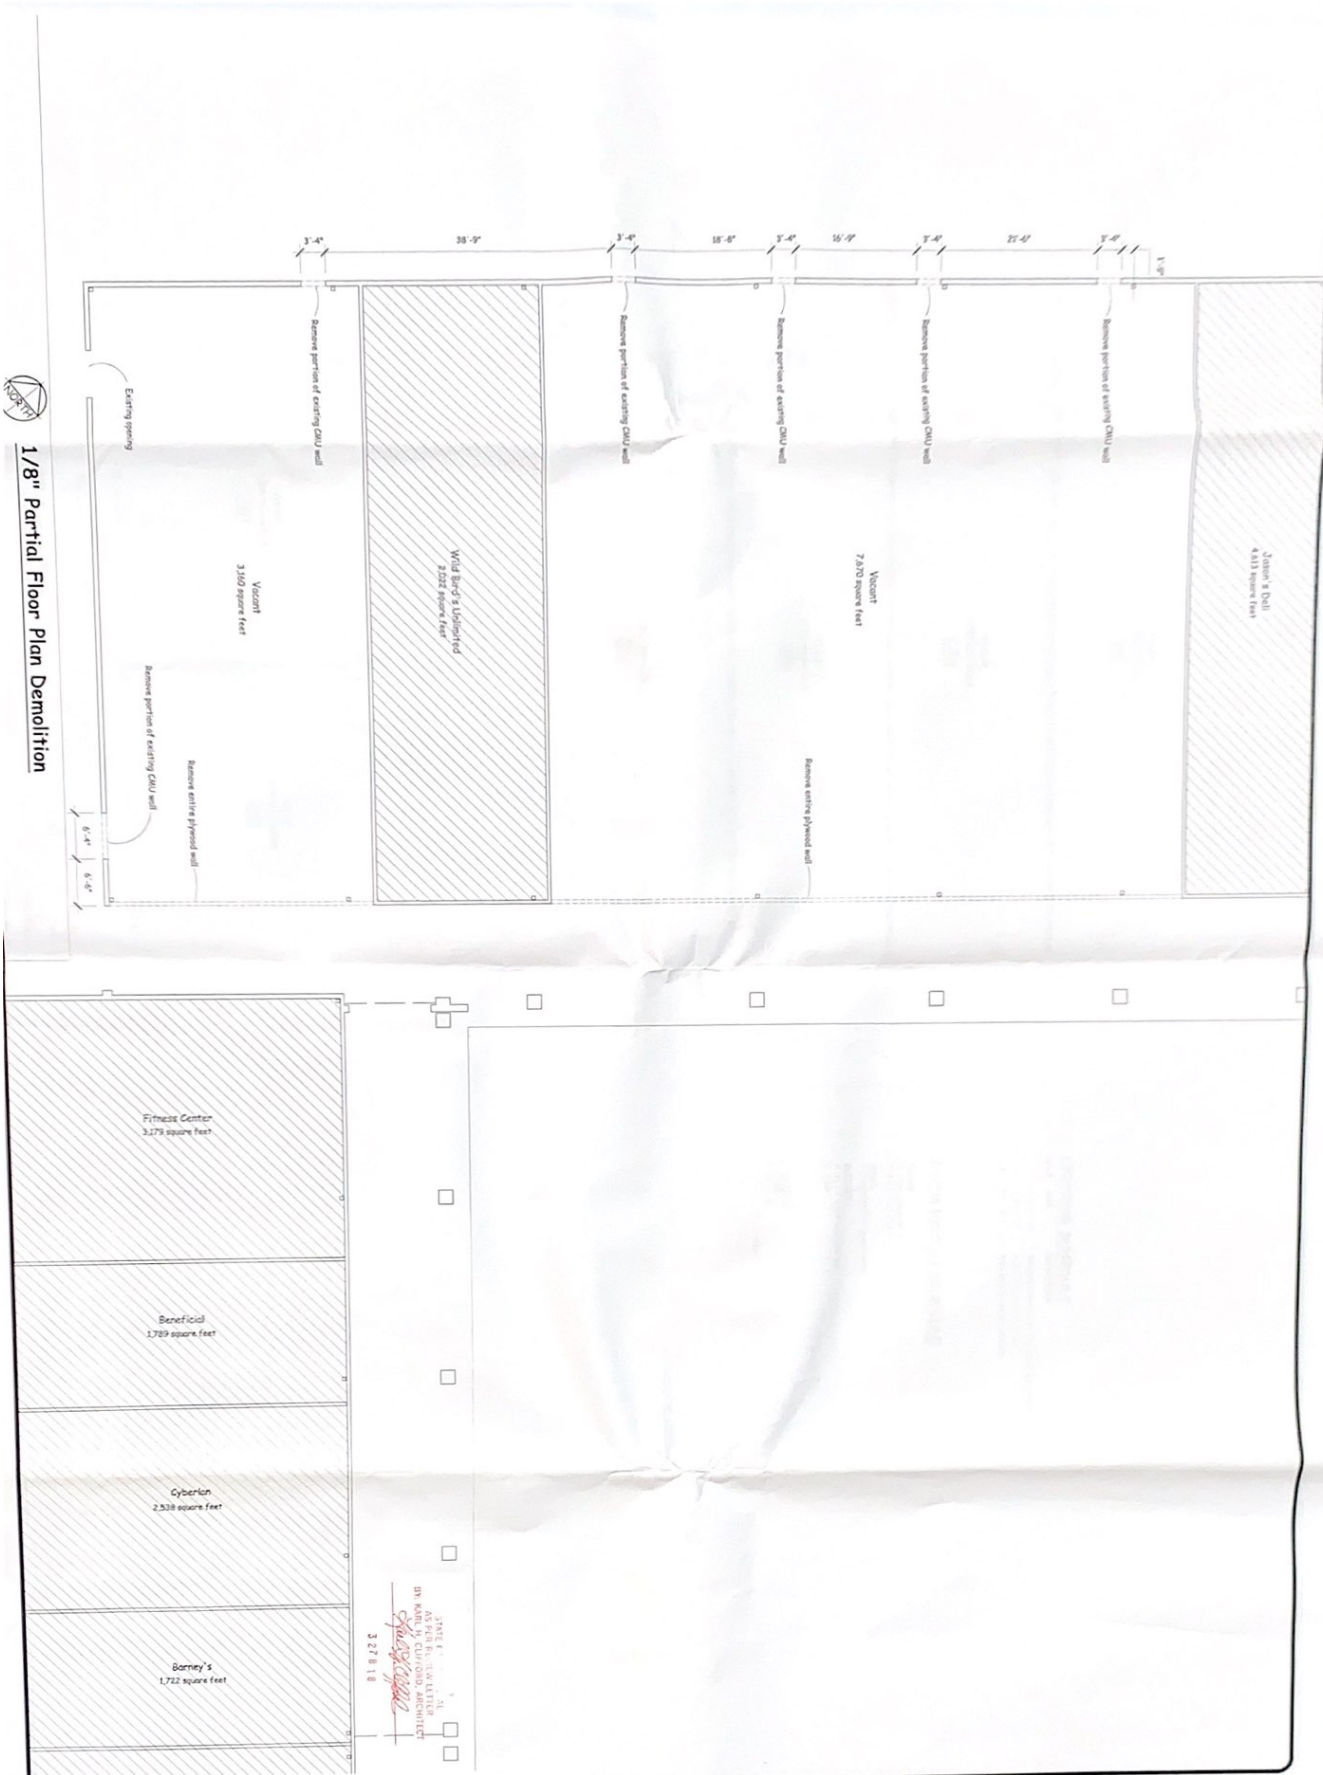

1/8" Partial Floor Plan Demolition

STATE OF LOUISIANA
 BR. MARK H. CLAYTON, ARCHITECT
 3 278 18

3	A-3
10	
20	
30	
40	
50	
60	
70	
80	
90	
100	

Finish Out of Existing Tenant Space:
The Boulevard Shopping Center
 Arnold Boulevard & Johnston Street
 Lafayette, LA


William J. Chat, AIA
201 Alva Road
Youngville, LA 70592
(337) 856-6812




A-5
5 or 10 METS

William J. Crist, AIA
201 Alva Road
Youngsville, LA 70592
(337) 856-6812

[illegible]

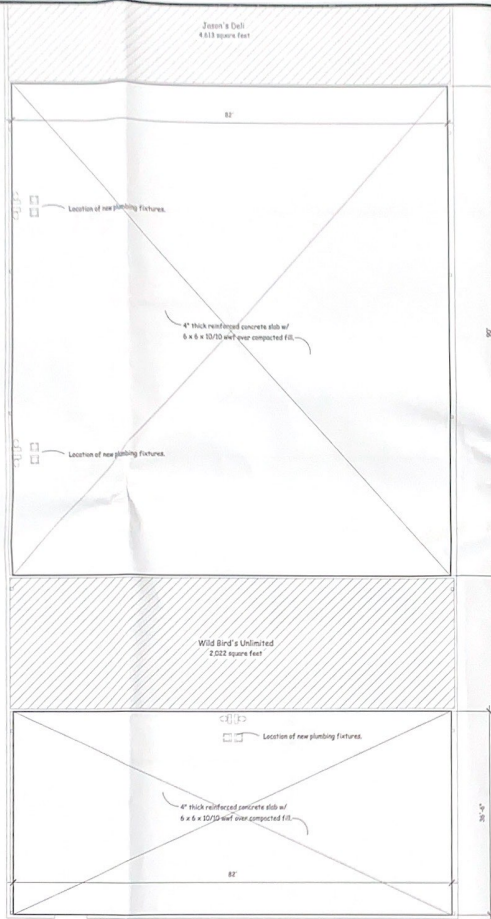

1/8" Foundation Plan

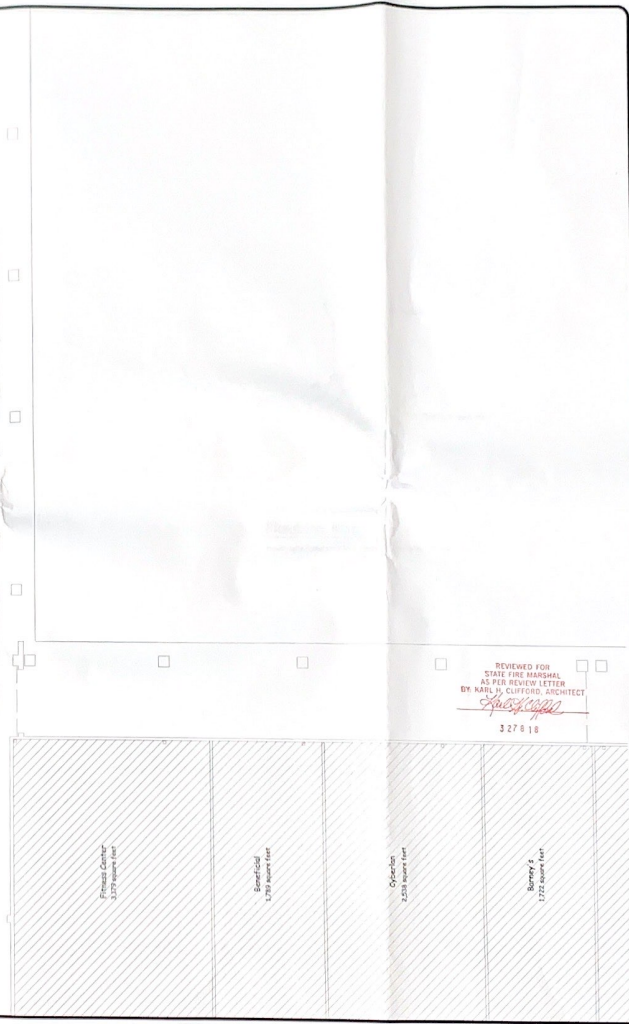

REVISION	BY


William J. Orr, AIA
201 And Road
Youngsville, LA 70552
(504) 856-6832



Final Out of Existing "Trout" Space:
The Boulevard Shopping Center
Arnold Boulevard & Johnston Street
Lafayette, LA

DESIGNED BY	W. J. C.
CHECKED	
DATE	May 6, 2007
JOB NO.	020225

SHEET
S-1
6 OF 10 SHEETS

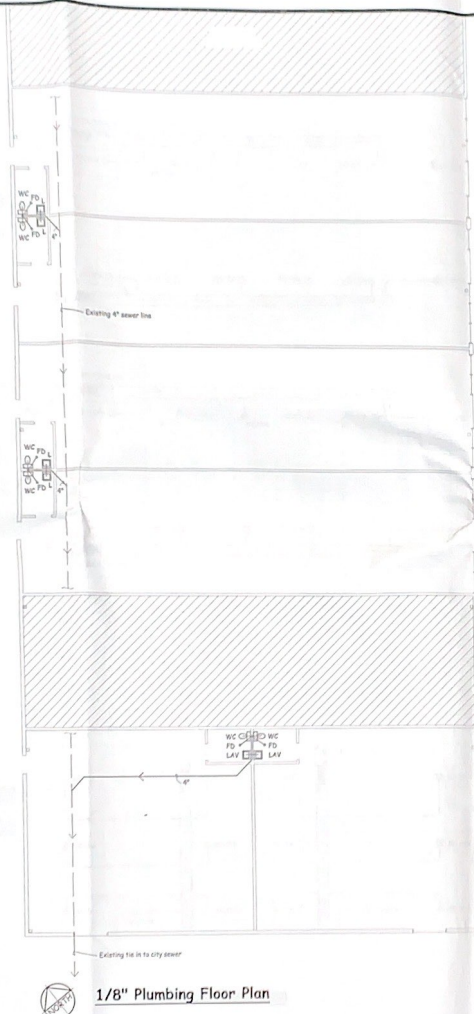

1/8" Plumbing Floor Plan

□


□

□

□

□

□

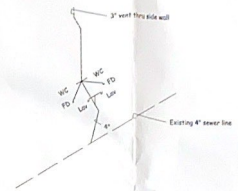

Plumbing Riser
Provide instantaneous hot water heater @ each Laundry (5 total)

REVIEWED F.W.
STATE FIRE MARSHAL
AS PER REVIEW LETTER
BY KAREL W. CLYDE, ARCHITECT
3/27/10


REVISION	BY

William J. Choi, AIA
201 Ann Road
Baton Rouge, LA 70802
(504) 386-8822



Finish Out of Existing Tenant Space
The Boulevard Shopping Center
Arnold Boulevard & Johnston Street
Lafayette, LA

DESIGN
W J C
DATE
May 6, 2007
JOB NO.
020215
SHEET
P-1
7 of 10

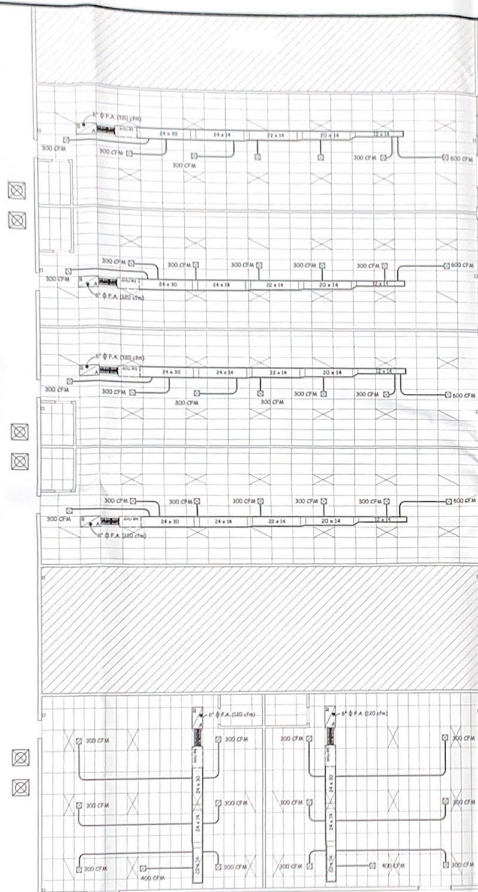

1/8" Mechanical Floor Plan

AC EQUIPMENT SCHEDULE

ANU #	WPA	BTU COOLING	CFM	HEAT (BTU)	AIR HANDLER	ELEC HEAT	CONDENSER	ELEC POWER
12.3.4	True	64,000	2,400	11.0	TRACOR 047	BAWHTR12.3.4	TTXAG05A	208, 3 phase
5.5	True	59,000	2,200	11.5	2-ATEC050A	BAWHTR53-5500	TTXAG06A	208, 3 phase

FLEX DUCT SCHEDULE

CFM	DUCT SIZE
300	12" Ø
400	12" Ø
600	12" Ø

REVIEWED FOR:
STATE FIRE MARSHAL
AS PER REVIEW LETTER
BY KYLE W. CLIFFORD ARCHITECT
Kyle Clifford
5/27/18

REVISION	BY

William Z. Orr, AIA
302 Alca Road
Newquinn, LA 70562
(337) 856-4832




The Boulevard Shopping Center
Architects & Builders, Inc.
Lafayette, LA

Final Out of Existing Tenant Space:
STATE FIRE MARSHAL
AS PER REVIEW LETTER
BY KYLE W. CLIFFORD ARCHITECT
Kyle Clifford
5/27/18


DATE	BY
May 5, 2007	WZC
May 5, 2007	WZC
May 5, 2007	WZC
May 5, 2007	WZC
May 5, 2007	WZC

M-1
8 of 10 SHEETS

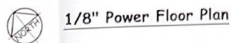

REVIEWED FOR
STATE FIRE MARSHAL
AS PER REVIEW LETTER
BY: KARL H. CLIFFORD, ARCHITECT
Karl H. Clifford
3/27/18

DRAWN	W J C
CHECKED	
DATE	May 6, 2007
JOB NO	020225
SHEET	E-1
9 OF 10 SHEETS	

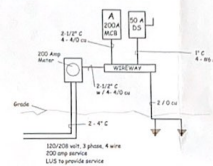

☐ REVIEWED FOR
 STATE FIRE MARSHAL
 AS PER REVIEW LETTER
 BY: KARL H. CLIFFORD, ARCHITECT
Karl H. Clifford
 327818

Finish Out of Existing Tenant Space:
The Boulevard
 Arnold Boulevard & Johnston Street
 Lafayette, LA

William J. Crist, AIA
101 Alva Road
Youngsville, LA 70592
(337) 856-6812

center

Page 10 of 10

DRAWN
WJC
CHECKED

DATE
May 6, 2007

020225
SHEET
F-2

10 of 10 54
