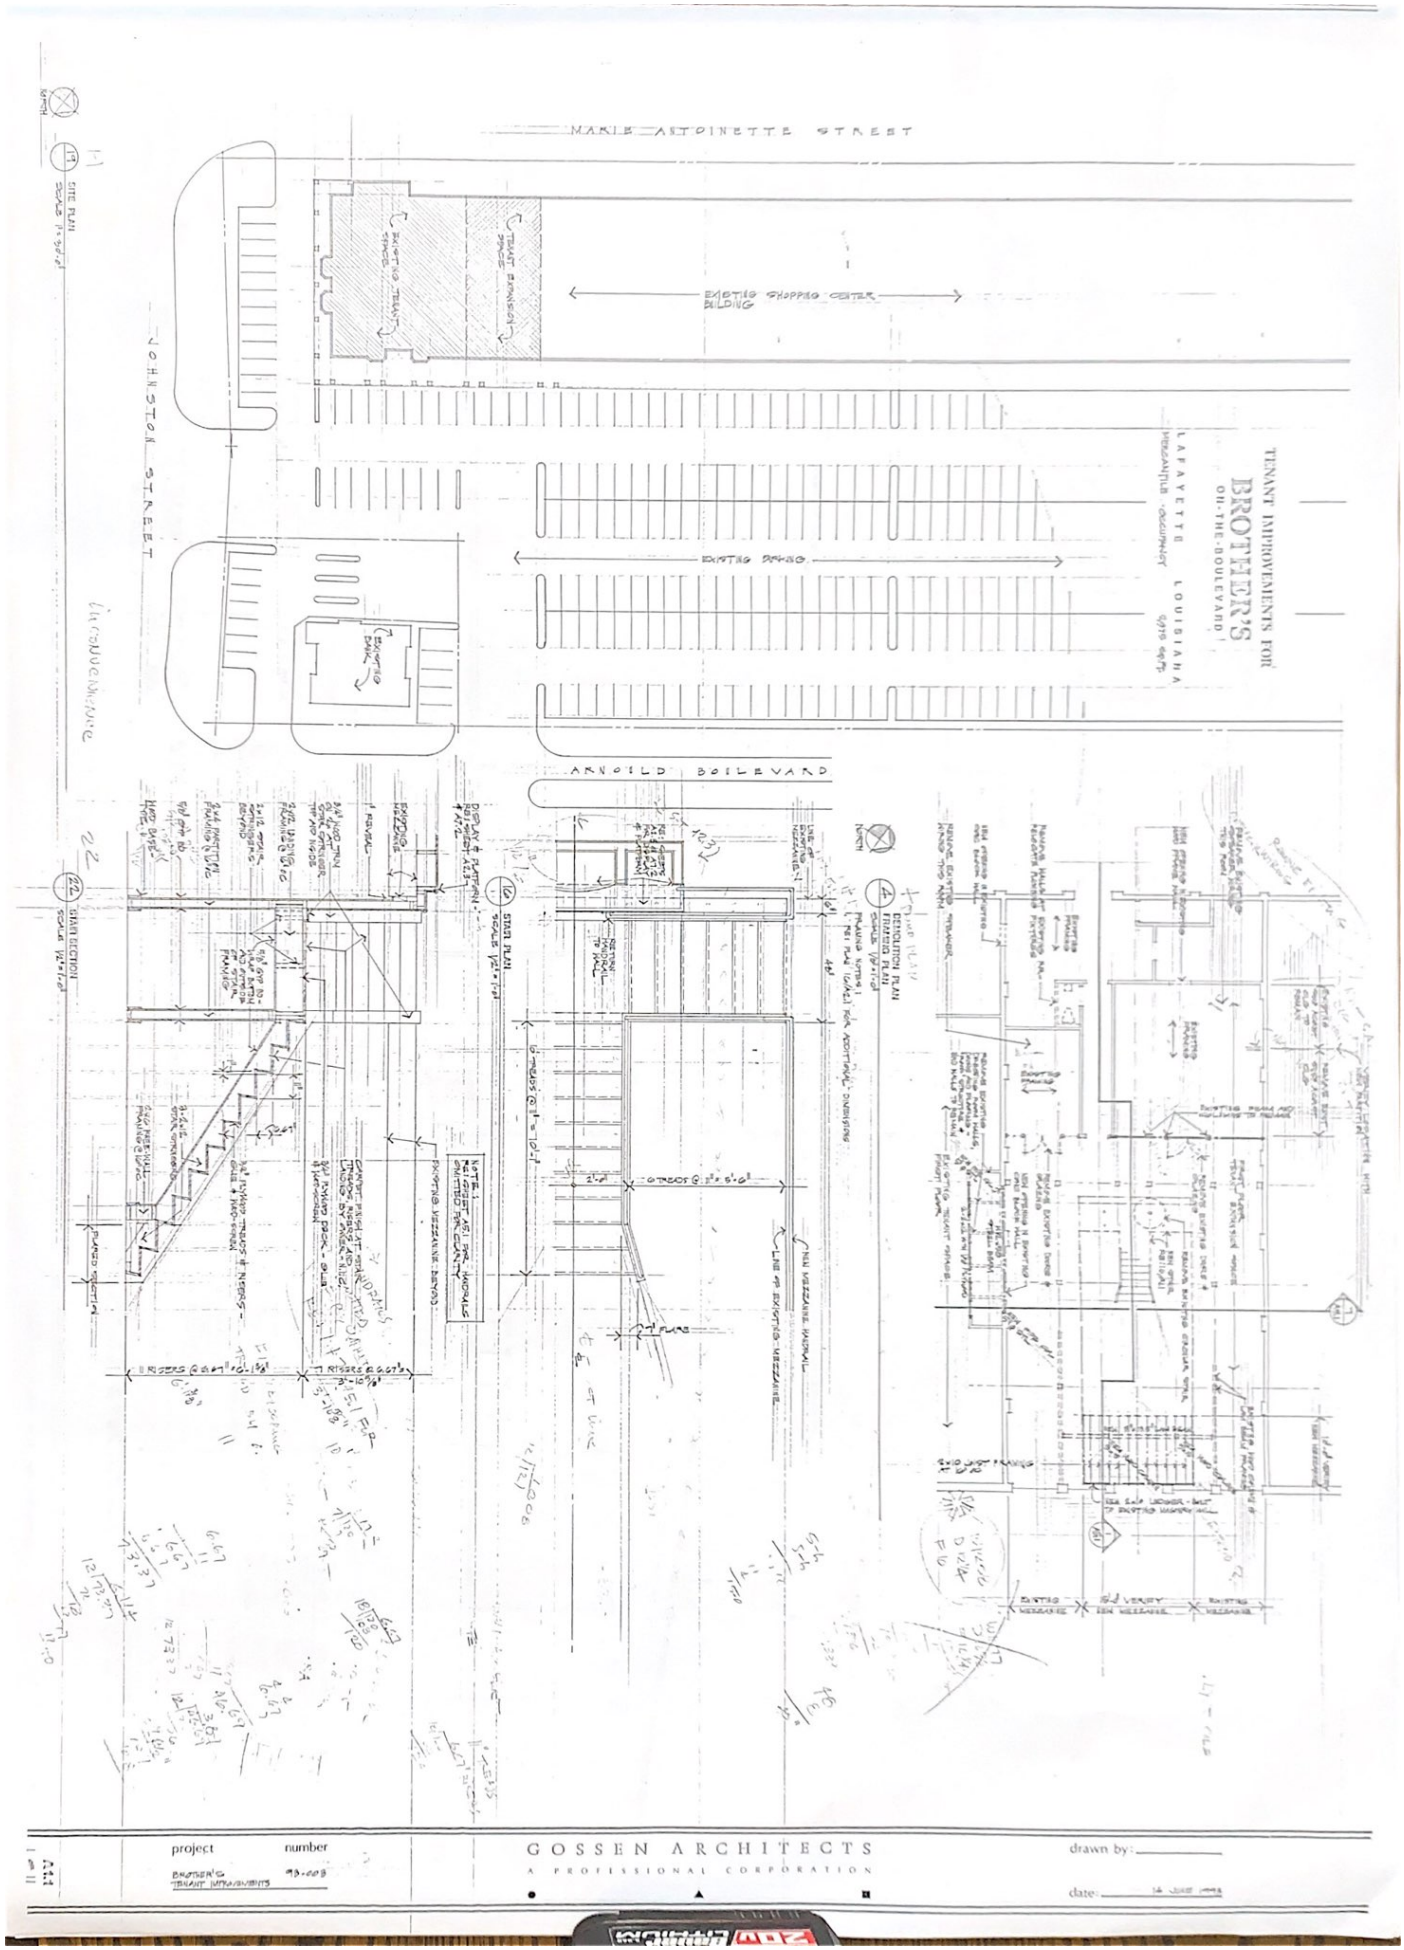

MARIE ANTOINETTE STREET
JOHNSTON STREET
ARNOULD BOULEVARD
EXISTING SHOPPING CENTER BUILDING
EXISTING BANK
TENANT EXPANSION SPACE
EXISTING TENANT SPACE
TENANT IMPROVEMENTS FOR
BROTHER'S
ON THE BOULEVARD
LAFAYETTE LOUISIANA
SITE PLAN
SCALE 1"=50'-0"
STAIR ELEVATION
SCALE 1/4"=1'-0"
STAIR PLAN
SCALE 1/4"=1'-0"
DEMOLITION PLAN
FRAMING PLAN
project
BROTHER'S TENANT IMPROVEMENTS
number
98-008
GOSSEN ARCHITECTS
A PROFESSIONAL CORPORATION
drawn by:
date: