

NOTES:

BUILDING HEIGHT EXCLUDES FACADE WHICH IS APPROX. 23.6'

"THIS SURVEY WAS CONDUCTED BY ME OR UNDER MY DIRECT SUPERVISION BASED ON STANDARDS FOR CLASS C SURVEYS IN ACCORDANCE WITH THE MINIMUM STANDARDS FOR PROPERTY BOUNDARY SURVEYS AS ADOPTED BY THE BOARD OF REGISTRATION FOR PROFESSIONAL ENGINEERS AND LAND SURVEYORS."

"THIS PROPERTY IS NOT LOCATED IN A FLOOD HAZARD AREA ACCORDING TO THE F.E.M.A. FLOOD INSURANCE RATE MAP DATED: DECEMBER 21, 2018 (ZONE X) Community Panel No. 22055C0160 J."

STATE OF LOUISIANA
LAFAYETTE PARISH

I, Andre E. Montagnet, a registered Professional Land Surveyor in the State of Louisiana of the firm of "Montagnet & Domingue, Inc.; Lafayette, LA; Telephone #337-981-2130", hereby certify that the premises shown hereon is a true and correct plot of the property described herein; that the buildings thereon are located with respect to property boundaries as shown; that there are no electric or telephone wires or structures or supports thereon or over said premises except as shown; that all rights-of-way, easements or joint drives over or across said premises visible on the surface are shown; that the premises surveyed do not encroach on the adjoining property and that the adjoining property does not encroach on the premises surveyed except as shown; I further certify that I have consulted Federal Insurance Administration Flood Hazard Boundary Maps as are currently available and have found that the subject property DOES NOT lie in a Special Flood Hazard Area.

WITNESS my hand this 2nd day of May, 2007.
Andre E. Montagnet, P.L.S.
LA Reg. No. 4484

LEGAL DESCRIPTION


A parcel of Ground located in Section 42, Township 10 South, Range 4 East, Lafayette Parish, Louisiana, within the City Limits of City of Lafayette and being a portion of the formally dedicated Block I of Arnould Heights Subdivision and Block I of Arnould Heights Extension No. 1.

Commencing at the Southwest Right-of-Way corner of intersection of Arnould Boulevard and Patricia Street thence South 38°32'00" East a distance of 25.00 feet to the Point of Beginning.
Thence South 38°32'00" East a distance of 550.12 feet; thence South 51°28'00" West a distance of 100.00 feet; thence South 38°32'00" East a distance of 120.61 feet; thence along a curved line to the Left having a radius of 1,872.44 feet, Length of 168.53 feet and a chord of South 51°07'34" West with a distance of 168.48 feet; thence along a curved line to the Right having a radius of 30.00 feet, Length of 48.65 feet and a chord of North 84°59'34" West with a distance of 43.49 feet; thence North 38°32'00" West a distance of 641.77 feet; thence along a curved line to the Right having a Radius of 25.00 feet, Length of 39.27 feet and a chord of North 06°28'00" East a distance of 35.36 feet; thence North 51°28'00" East a distance of 250.00 feet; thence along a curved line to the Right having a Radius of 25.00 feet, Length of 39.27 feet and a chord of South 83°32'00" East a distance of 35.36 feet to the Point of Beginning.

LOT 7, BLOCK M, ARNOULD HEIGHTS SUBDIVISION, EXT. NO. 1 A parcel of ground located in Section 42, Township 10 South, Range 4 East, Lafayette Parish, Louisiana, within the City of Lafayette being more particularly described as follows:

Commencing at the southwestern right-of-way corner of the intersection of Marie Antoinette Street and Patricia Street, thence South 38°32'00" East a distance of 25.00 feet to the Point of Beginning.

Thence South 38°32'00" East a distance of 75.00 feet; thence South 51°28'00" West a distance of 150.17 feet; thence North 38°43'28" West a distance of 100.00 feet; thence North 51°28'00" East a distance of 125.50 feet; thence along a curve to the right having a radius of 25.00 feet, an arc length of 39.27 feet, and a chord of South 83°32'00" East and a distance of 35.36 feet to the Point of Beginning.

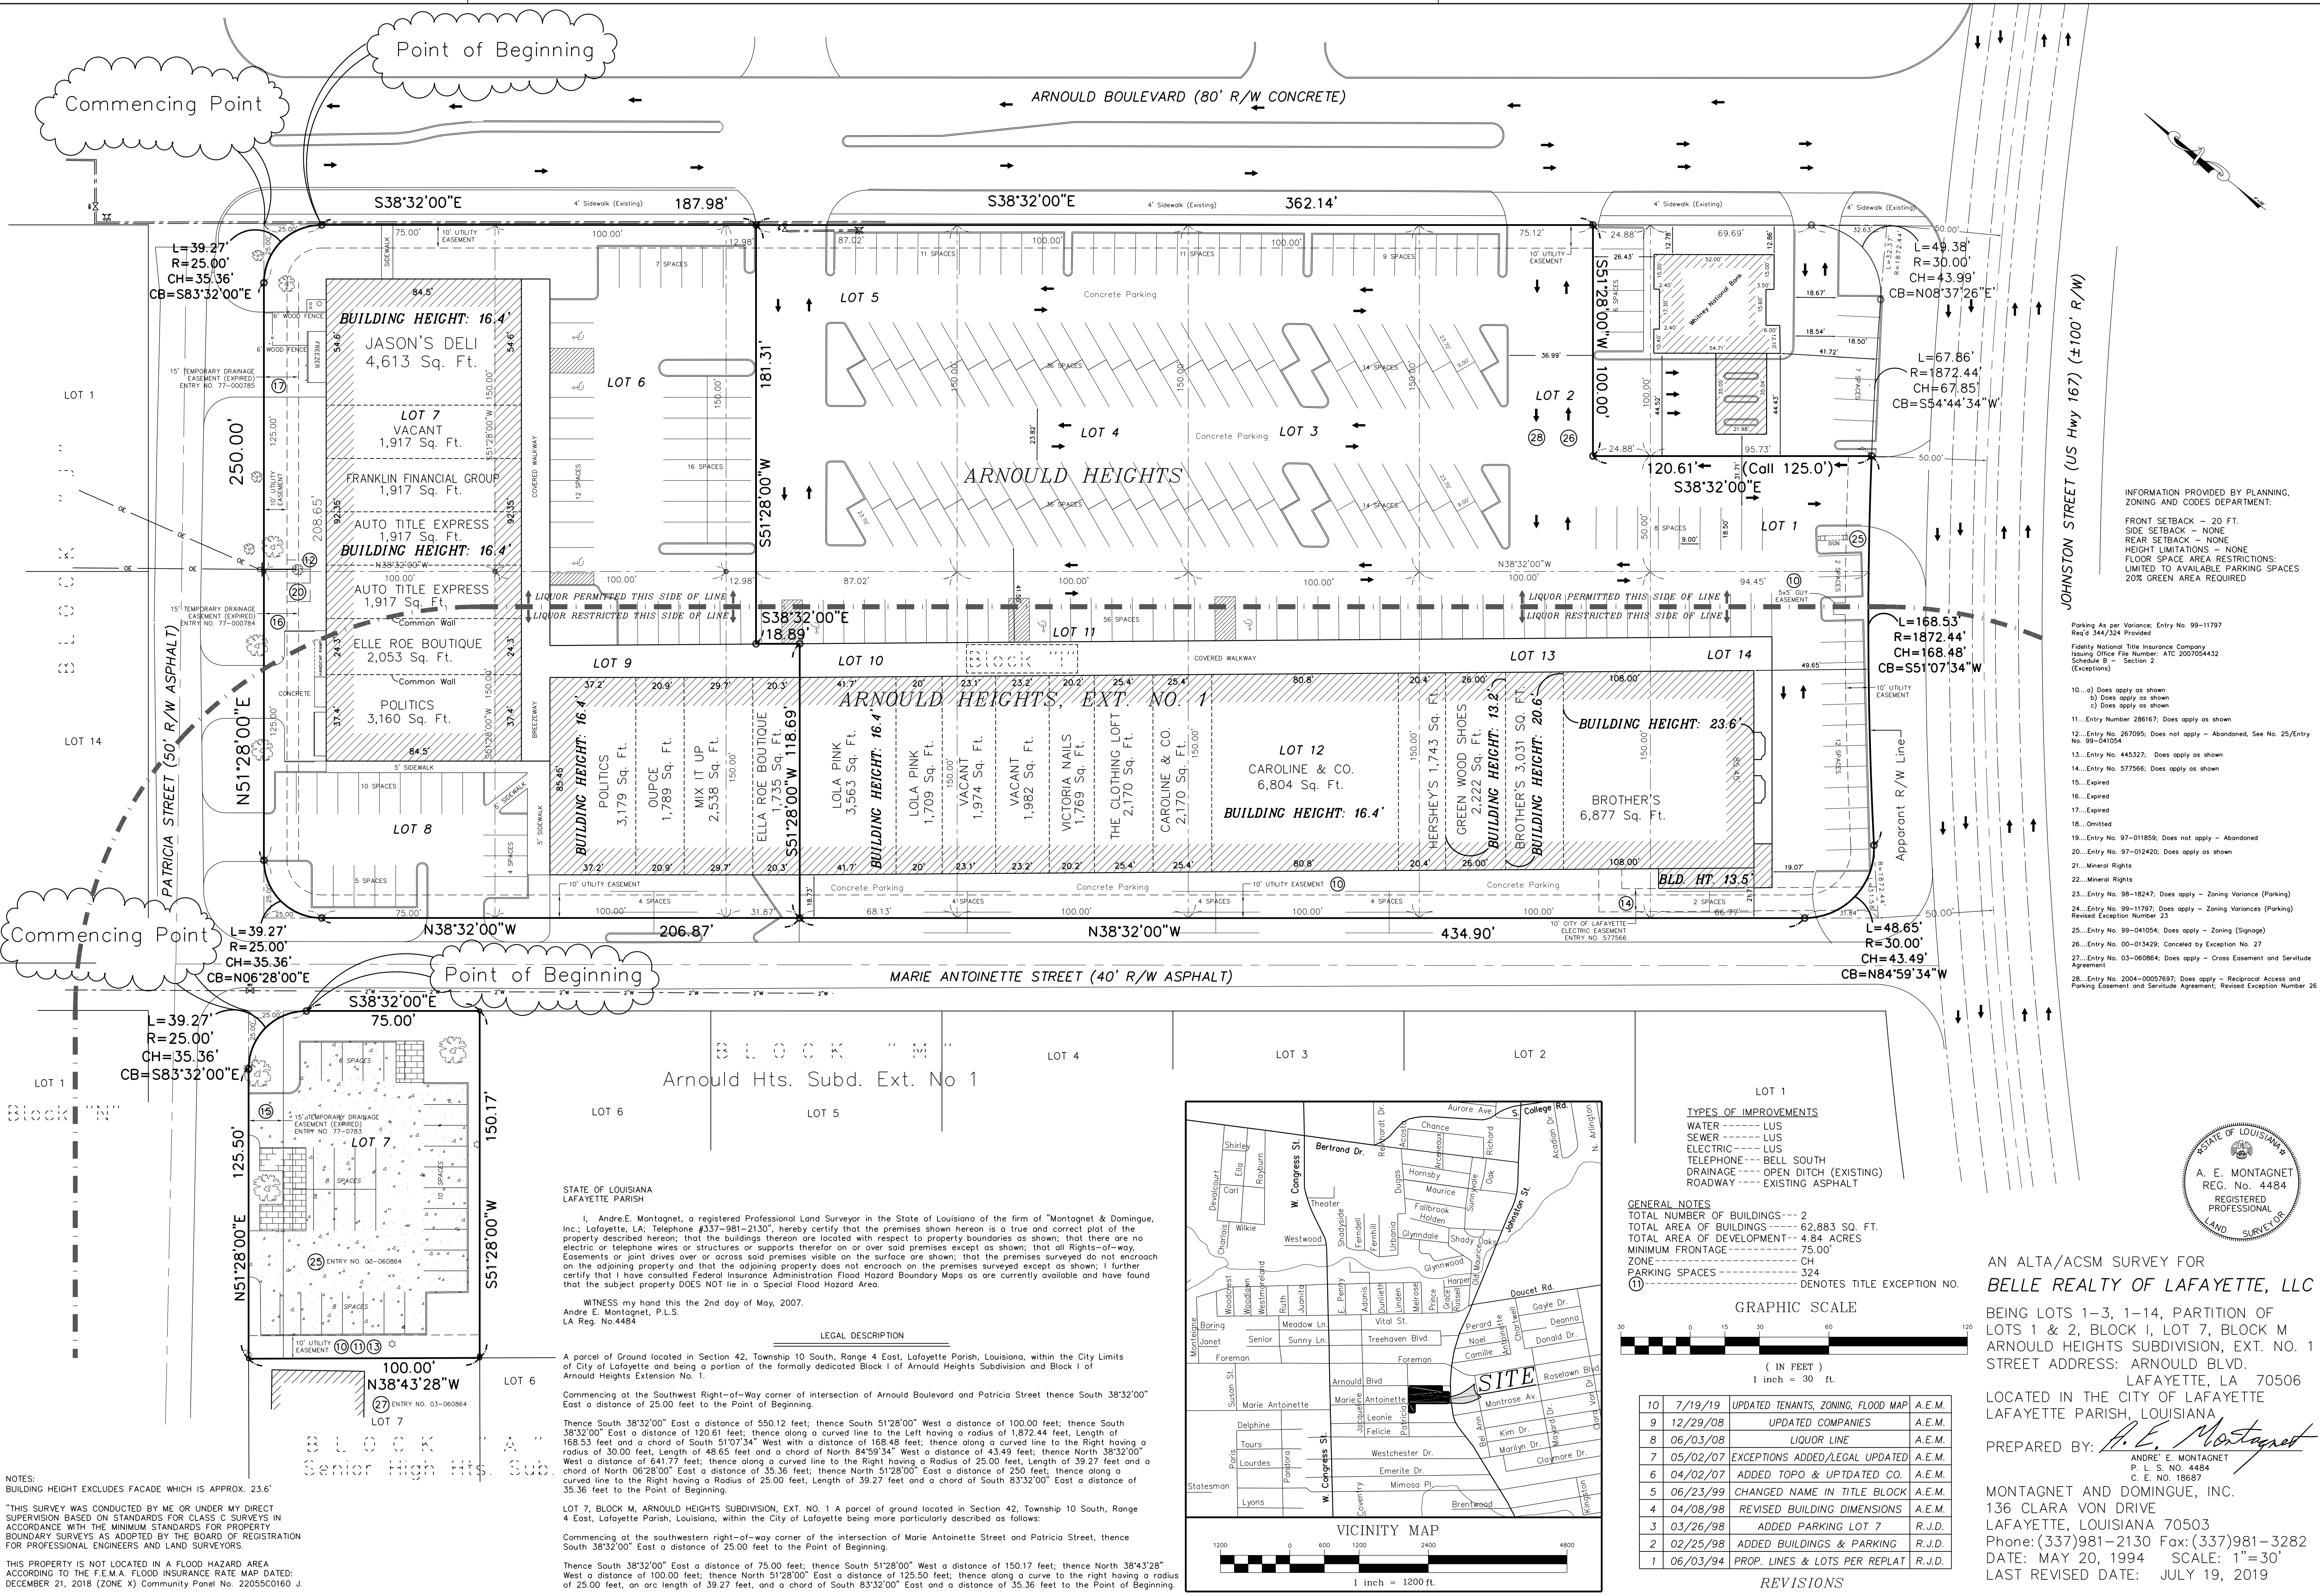

INFORMATION PROVIDED BY PLANNING, ZONING AND CODES DEPARTMENT:
FRONT SETBACK - 20 FT.
SIDE SETBACK - NONE
REAR SETBACK - NONE
HEIGHT LIMITATIONS - NONE
FLOOR SPACE AREA RESTRICTIONS: LIMITED TO AVAILABLE PARKING SPACES
20% GREEN AREA REQUIRED

- Parking As per Variance; Entry No. 99-11797
Reqd 344/324 Provided
Fidelity National Title Insurance Company
Issuing Office File Number: ATC 2007054432
Schedule B - Section 2
(Exceptions)
- 10...a) Does apply as shown
b) Does apply as shown
c) Does apply as shown
 - 11...Entry Number 286167; Does apply as shown
 - 12...Entry No. 267095; Does not apply - Abandoned, See No. 25/Entry No. 99-041054
 - 13...Entry No. 445327; Does apply as shown
 - 14...Entry No. 577566; Does apply as shown
 - 15...Expired
 - 16...Expired
 - 17...Expired
 - 18...Omitted
 - 19...Entry No. 97-011859; Does not apply - Abandoned
 - 20...Entry No. 97-012420; Does apply as shown
 - 21...Mineral Rights
 - 22...Mineral Rights
 - 23...Entry No. 98-18247; Does apply - Zoning Variance (Parking)
 - 24...Entry No. 99-11797; Does apply - Zoning Variance (Parking)
 - 25...Entry No. 99-041054; Does apply - Zoning (Signage)
 - 26...Entry No. 00-013429; Cancelled by Exception No. 27
 - 27...Entry No. 03-060864; Does apply - Cross Easement and Servitude Agreement
 - 28...Entry No. 2004-00057897; Does apply - Reciprocal Access and Parking Easement and Servitude Agreement; Revised Exception Number 28



AN ALTA/ACSM SURVEY FOR
BELLE REALTY OF LAFAYETTE, LLC
BEING LOTS 1-3, 1-14, PARTITION OF
LOTS 1 & 2, BLOCK I, LOT 7, BLOCK M
ARNOULD HEIGHTS SUBDIVISION, EXT. NO. 1
STREET ADDRESS: ARNOULD BLVD.
LAFAYETTE, LA 70506
LOCATED IN THE CITY OF LAFAYETTE
LAFAYETTE PARISH, LOUISIANA
PREPARED BY: *A.E. Montagnet*
ANDRE E. MONTAGNET
P. L. S. NO. 4484
C. E. NO. 18687
MONTAGNET AND DOMINGUE, INC.
136 CLARA VON DRIVE
LAFAYETTE, LOUISIANA 70503
Phone: (337)981-2130 Fax: (337)981-3282
DATE: MAY 20, 1994 SCALE: 1"=30'
LAST REVISED DATE: JULY 19, 2019