


NOTE: BUILDING HEIGHT EXCLUDES
FACADE WHICH IS APPROX. 23.6'

"THIS SURVEY WAS CONDUCTED
BY ME OR UNDER MY DIRECT
SUPERVISION BASED ON
STANDARDS FOR CLASS C
SURVEYS IN ACCORDANCE WITH
THE MINIMUM STANDARDS FOR
PROPERTY BOUNDARY SURVEYS
AS ADOPTED BY THE BOARD OF
REGISTRATION FOR PROFESSIONAL
ENGINEERS AND LAND SURVEYORS.

NOTE: THIS PROPERTY IS NOT
LOCATED IN A FLOOD HAZARD
AREA ACCORDING TO THE F.E.M.A.
FLOOD INSURANCE RATE MAP
DATED: JANUARY 19, 1996 (ZONE X)
Community Panel No. 22055C0045 X

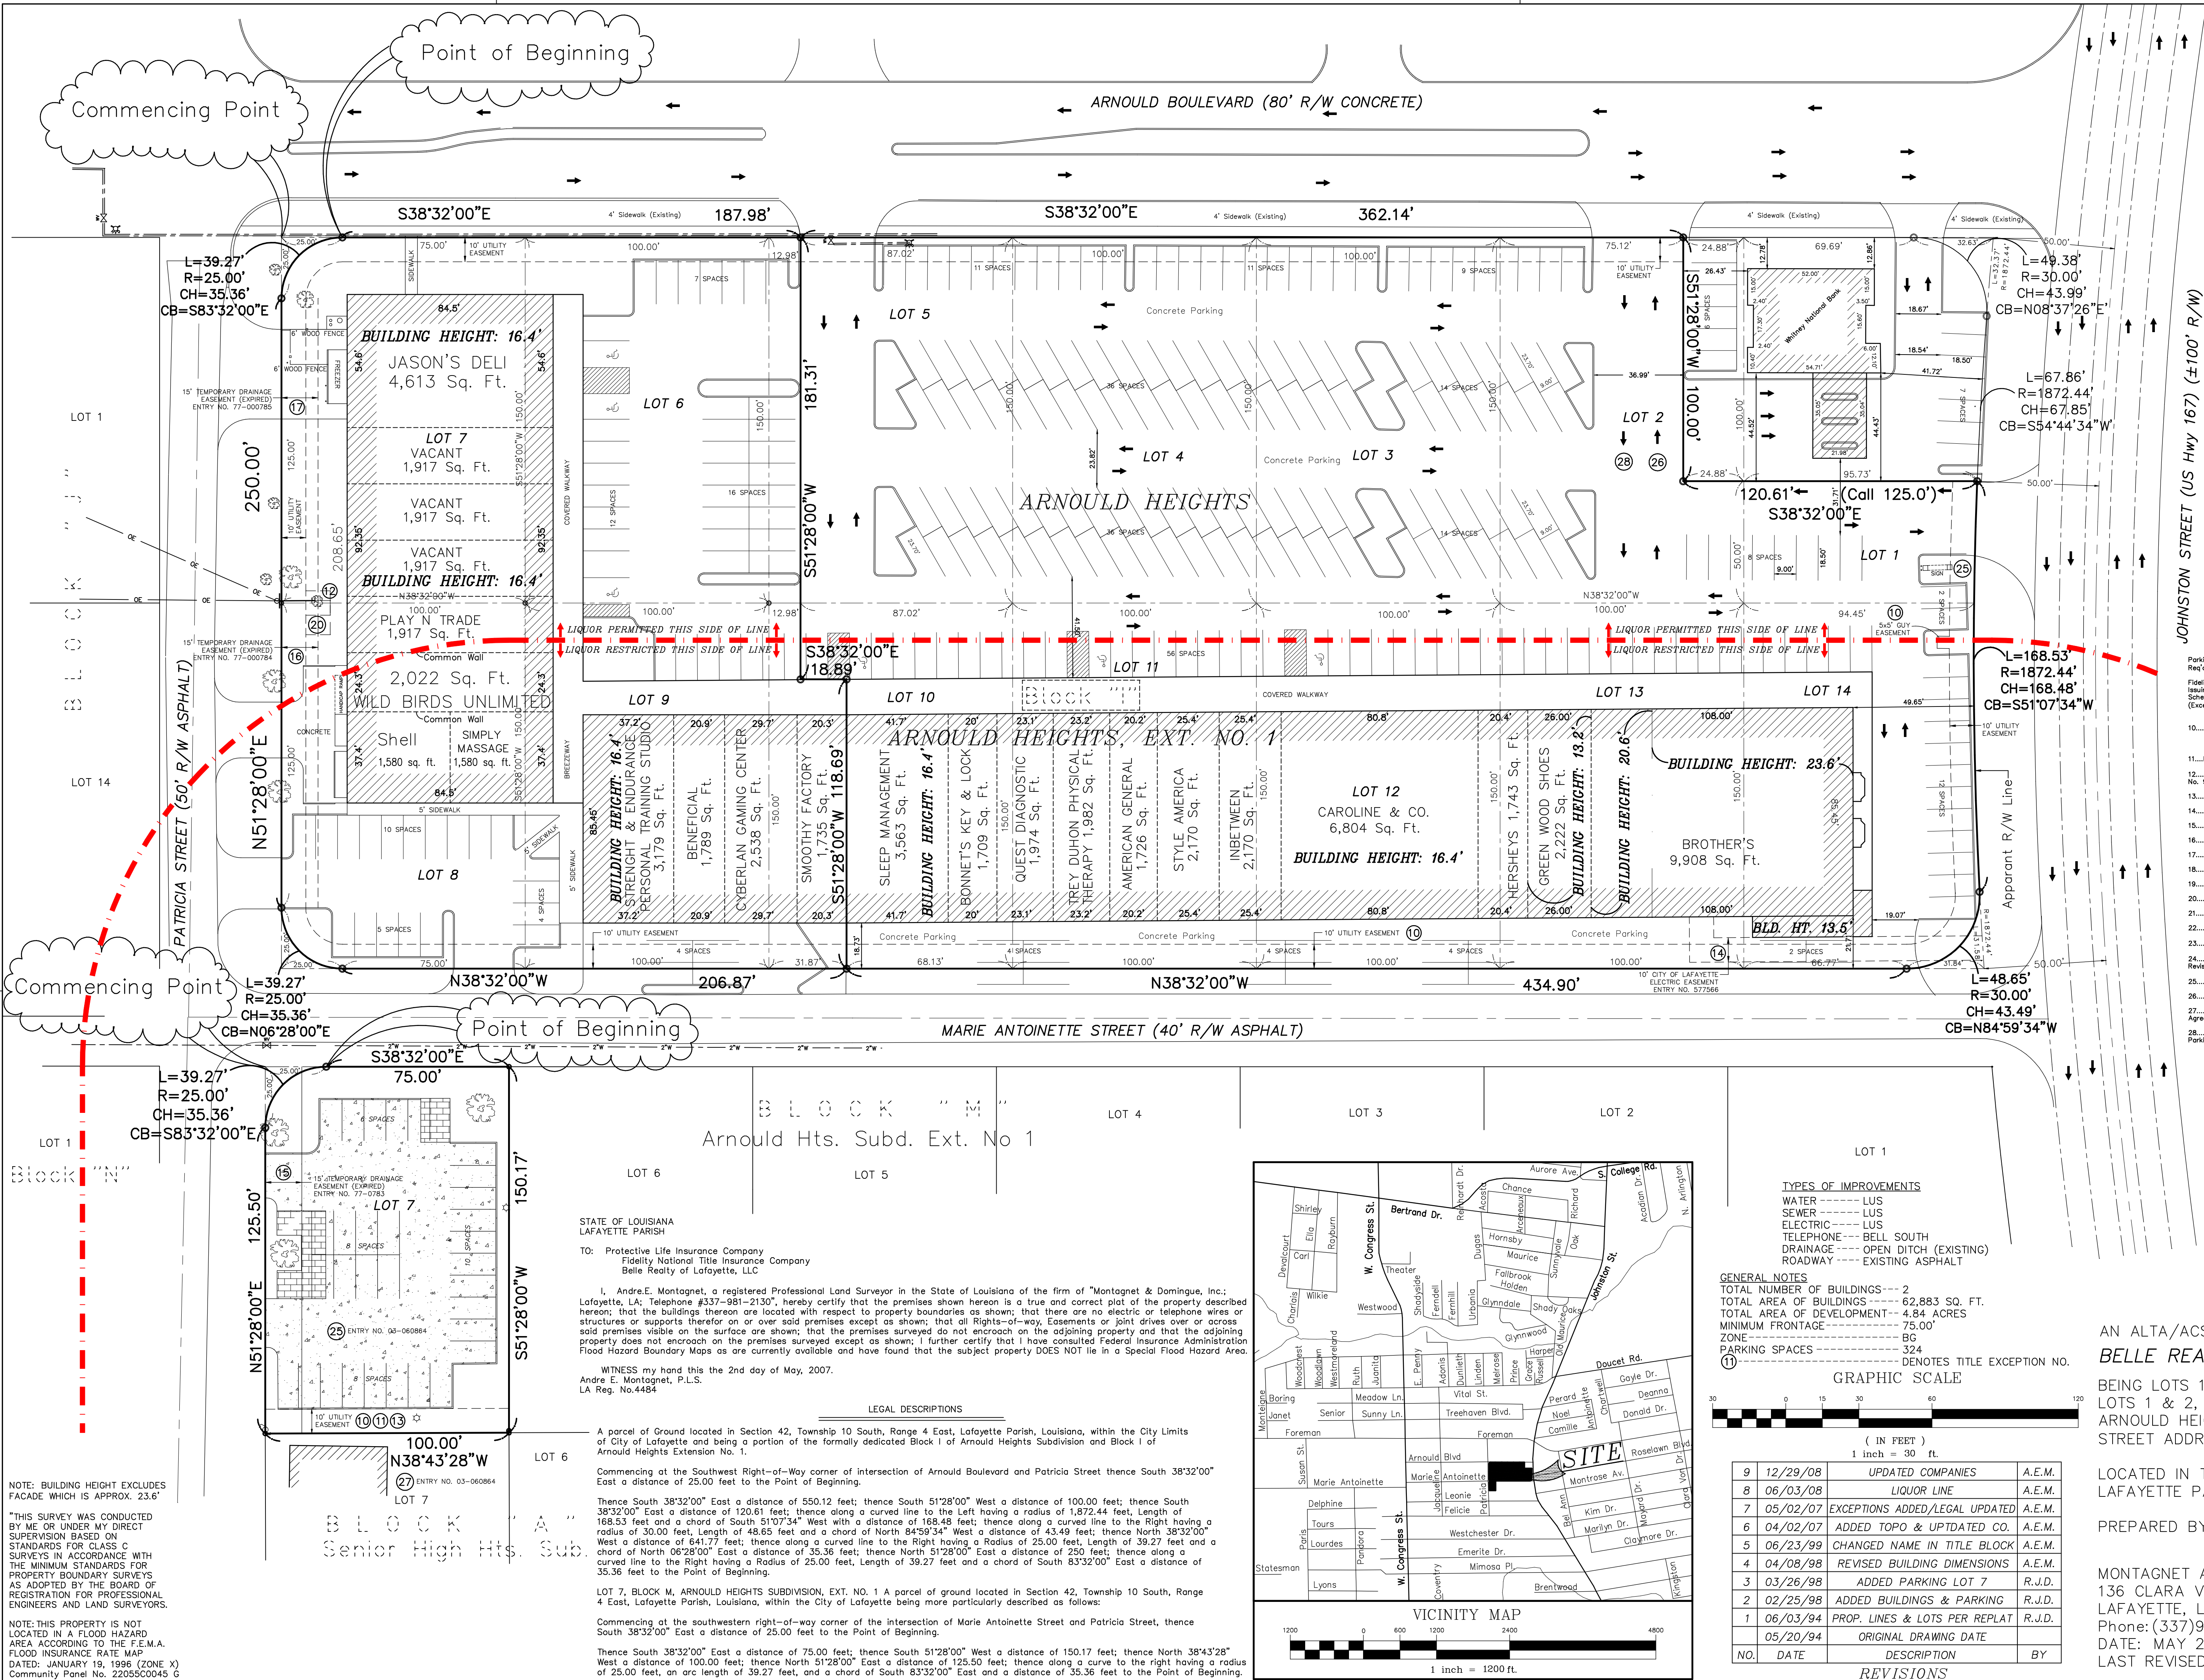

INFORMATION PROVIDED BY PLANNING,
ZONING AND CODES DEPARTMENT:

FRONT SETBACK - 20 FT.
SIDE SETBACK - NONE
REAR SETBACK - NONE
HEIGHT LIMITATIONS - NONE
FLOOR SPACE AREA RESTRICTIONS:
LIMITED TO AVAILABLE PARKING SPACES
20% GREEN AREA REQUIRED

Parking As per Variance; Entry No. 99-11797
Rec'd 544/324 Provided

Fidelity National Title Insurance Company
Issuing Office File Number: ATC 2007054432
Schedule B - Section 2
(Exceptions)

10...a) Does apply as shown
b) Does apply as shown
c) Does apply as shown

11...Entry Number 286167; Does apply as shown

12...Entry No. 267095; Does not apply - Abandoned, See No. 25/Entry
No. 99-041054

13...Entry No. 445327; Does apply as shown

14...Entry No. 577566; Does apply as shown

15...Expired

16...Expired

17...Expired

18...Omitted

19...Entry No. 97-011859; Does not apply - Abandoned

20...Entry No. 97-012420; Does apply as shown

21...Mineral Rights

22...Mineral Rights

23...Entry No. 98-18247; Does apply - Zoning Variance (Parking)

24...Entry No. 98-11797; Does apply - Zoning Variances (Parking)
Revised Exception Number 23

25...Entry No. 98-041054; Does apply - Zoning (Signage)

26...Entry No. 00-013429; Cancelled by Exception No. 27

27...Entry No. 03-060864; Does apply - Cross Easement and Servitude
Agreement

28...Entry No. 2004-00057697; Does apply - Reciprocal Access and
Parking Easement and Servitude Agreement; Revised Exception Number 28

TYPES OF IMPROVEMENTS

WATER ----- LUS
SEWER ----- LUS
ELECTRIC ----- LUS
TELEPHONE ----- BELL SOUTH
DRAINAGE ----- OPEN DITCH (EXISTING)
ROADWAY ----- EXISTING ASPHALT

GENERAL NOTES


TOTAL NUMBER OF BUILDINGS ---- 2
TOTAL AREA OF BUILDINGS ---- 62,883 SQ. FT.
TOTAL AREA OF DEVELOPMENT -- 4.84 ACRES
MINIMUM FRONTAGE ----- 75.00'
ZONE ----- BG
PARKING SPACES ----- 324
⑪ ----- DENOTES TITLE EXCEPTION NO.

GRAPHIC SCALE



NO.	DATE	DESCRIPTION	BY
9	12/29/08	UPDATED COMPANIES	A.E.M.
8	06/03/08	LIQUOR LINE	A.E.M.
7	05/02/07	EXCEPTIONS ADDED/LEGAL UPDATED	A.E.M.
6	04/02/07	ADDED TOPO & UPDATED CO.	A.E.M.
5	06/23/99	CHANGED NAME IN TITLE BLOCK	A.E.M.
4	04/08/98	REVISED BUILDING DIMENSIONS	A.E.M.
3	03/26/98	ADDED PARKING LOT 7	R.J.D.
2	02/25/98	ADDED BUILDINGS & PARKING	R.J.D.
1	06/03/94	PROP. LINES & LOTS PER REPLAT	R.J.D.
	05/20/94	ORIGINAL DRAWING DATE	

REVISIONS

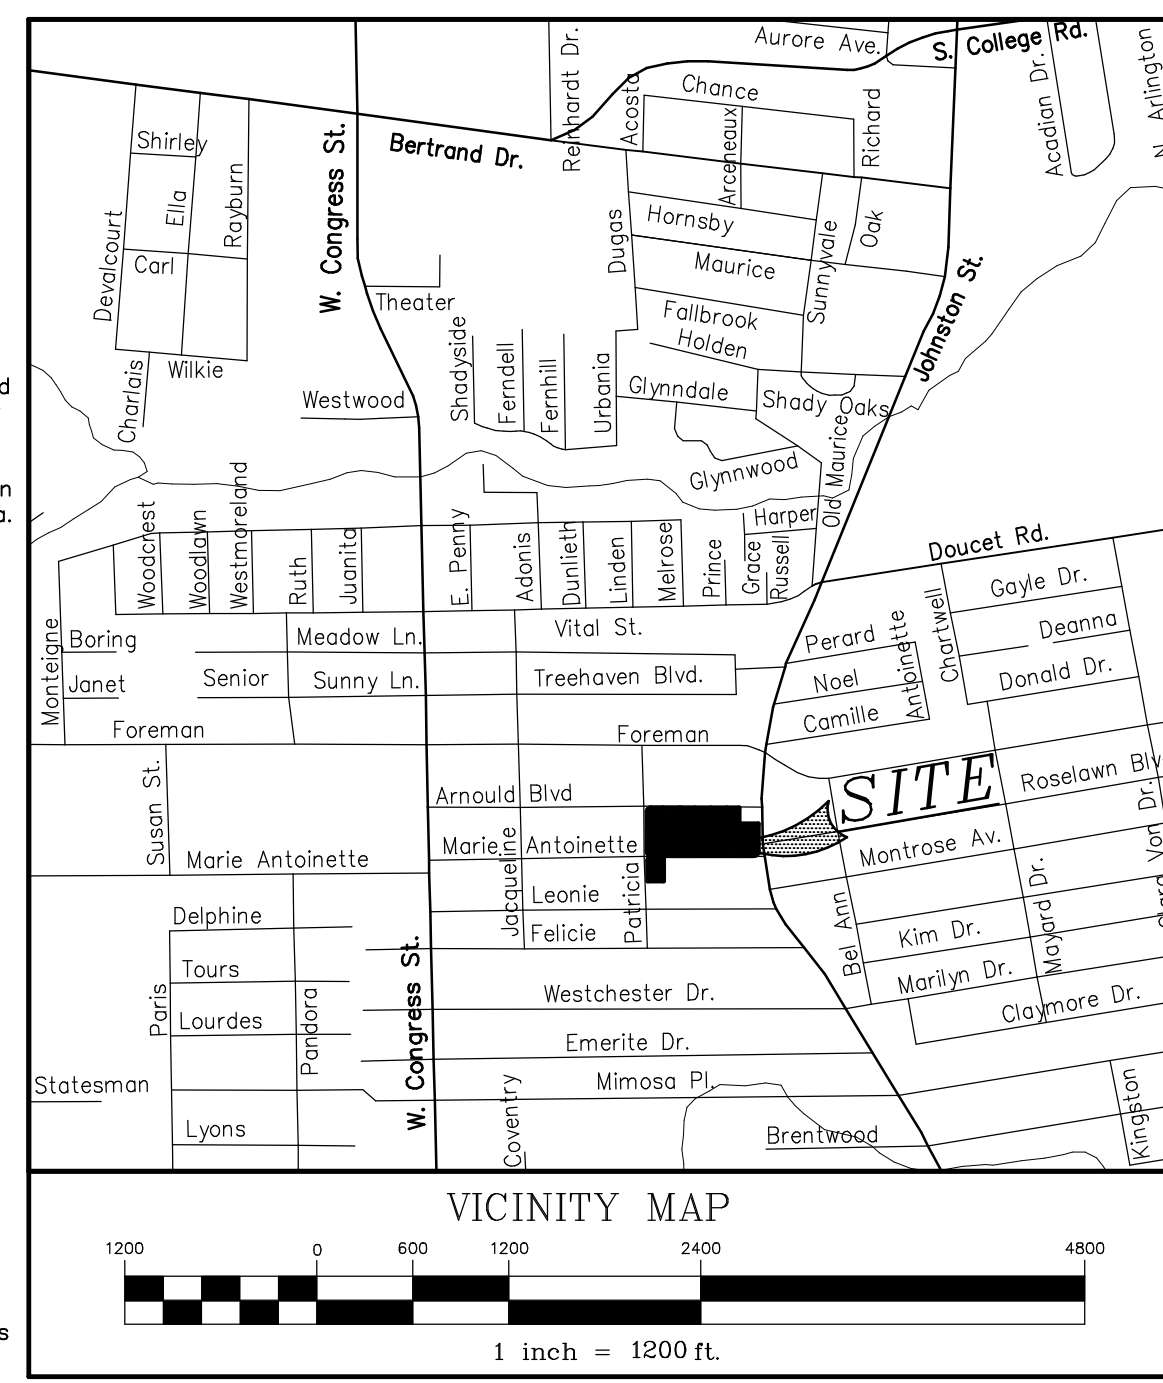

AN ALTA/ACSM SURVEY FOR
BELLE REALTY OF LAFAYETTE, LLC

BEING LOTS 1-3, 1-14, PARTITION OF
LOTS 1 & 2, BLOCK I, LOT 7, BLOCK M
ARNOULD HEIGHTS SUBDIVISION, EXT. NO. 1
STREET ADDRESS: ARNOULD BLVD.

LAFAYETTE, LA 70506
LOCATED IN THE CITY OF LAFAYETTE
LAFAYETTE PARISH, LOUISIANA

PREPARED BY:

ANDRE E. MONTAGNET
P. L. S. NO. 4484
C. E. NO. 18687
MONTAGNET AND DOMINGUE, INC.
136 CLARA VON DRIVE
LAFAYETTE, LOUISIANA 70503
Phone: (337)981-2130 Fax: (337)981-3282
DATE: MAY 20, 1994 SCALE: 1"=30'
LAST REVISED DATE: MAY 2, 2007