

ARNOULD BOULEVARD (80' R/W CONCRETE)


PATRICIA STREET (50' R/W ASPHALT)


MARIE ANTOINETTE STREET (40' R/W ASPHALT)

JOHNSTON STREET (US Hwy 167) (±100' R/W)

A SITE PLAN FOR  
**BELLE REALTY OF LAFAYETTE, LLC**  
BEING LOTS 1-3, 1-14, PARTITION OF  
LOTS 1 & 2, BLOCK I, LOT 7, BLOCK M  
ARNOULD HEIGHTS SUBDIVISION, EXT. NO. 1  
STREET ADDRESS: ARNOULD BLVD.  
LAFAYETTE, LA 70506  
LOCATED IN THE CITY OF LAFAYETTE  
LAFAYETTE PARISH, LOUISIANA


GRAPHIC SCALE

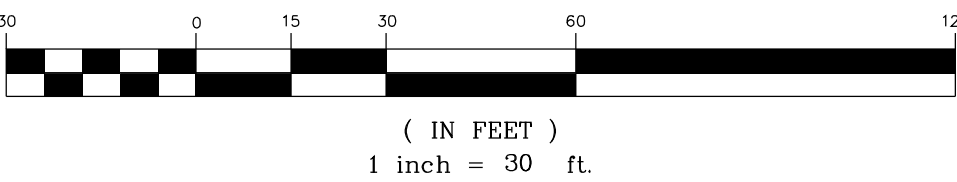

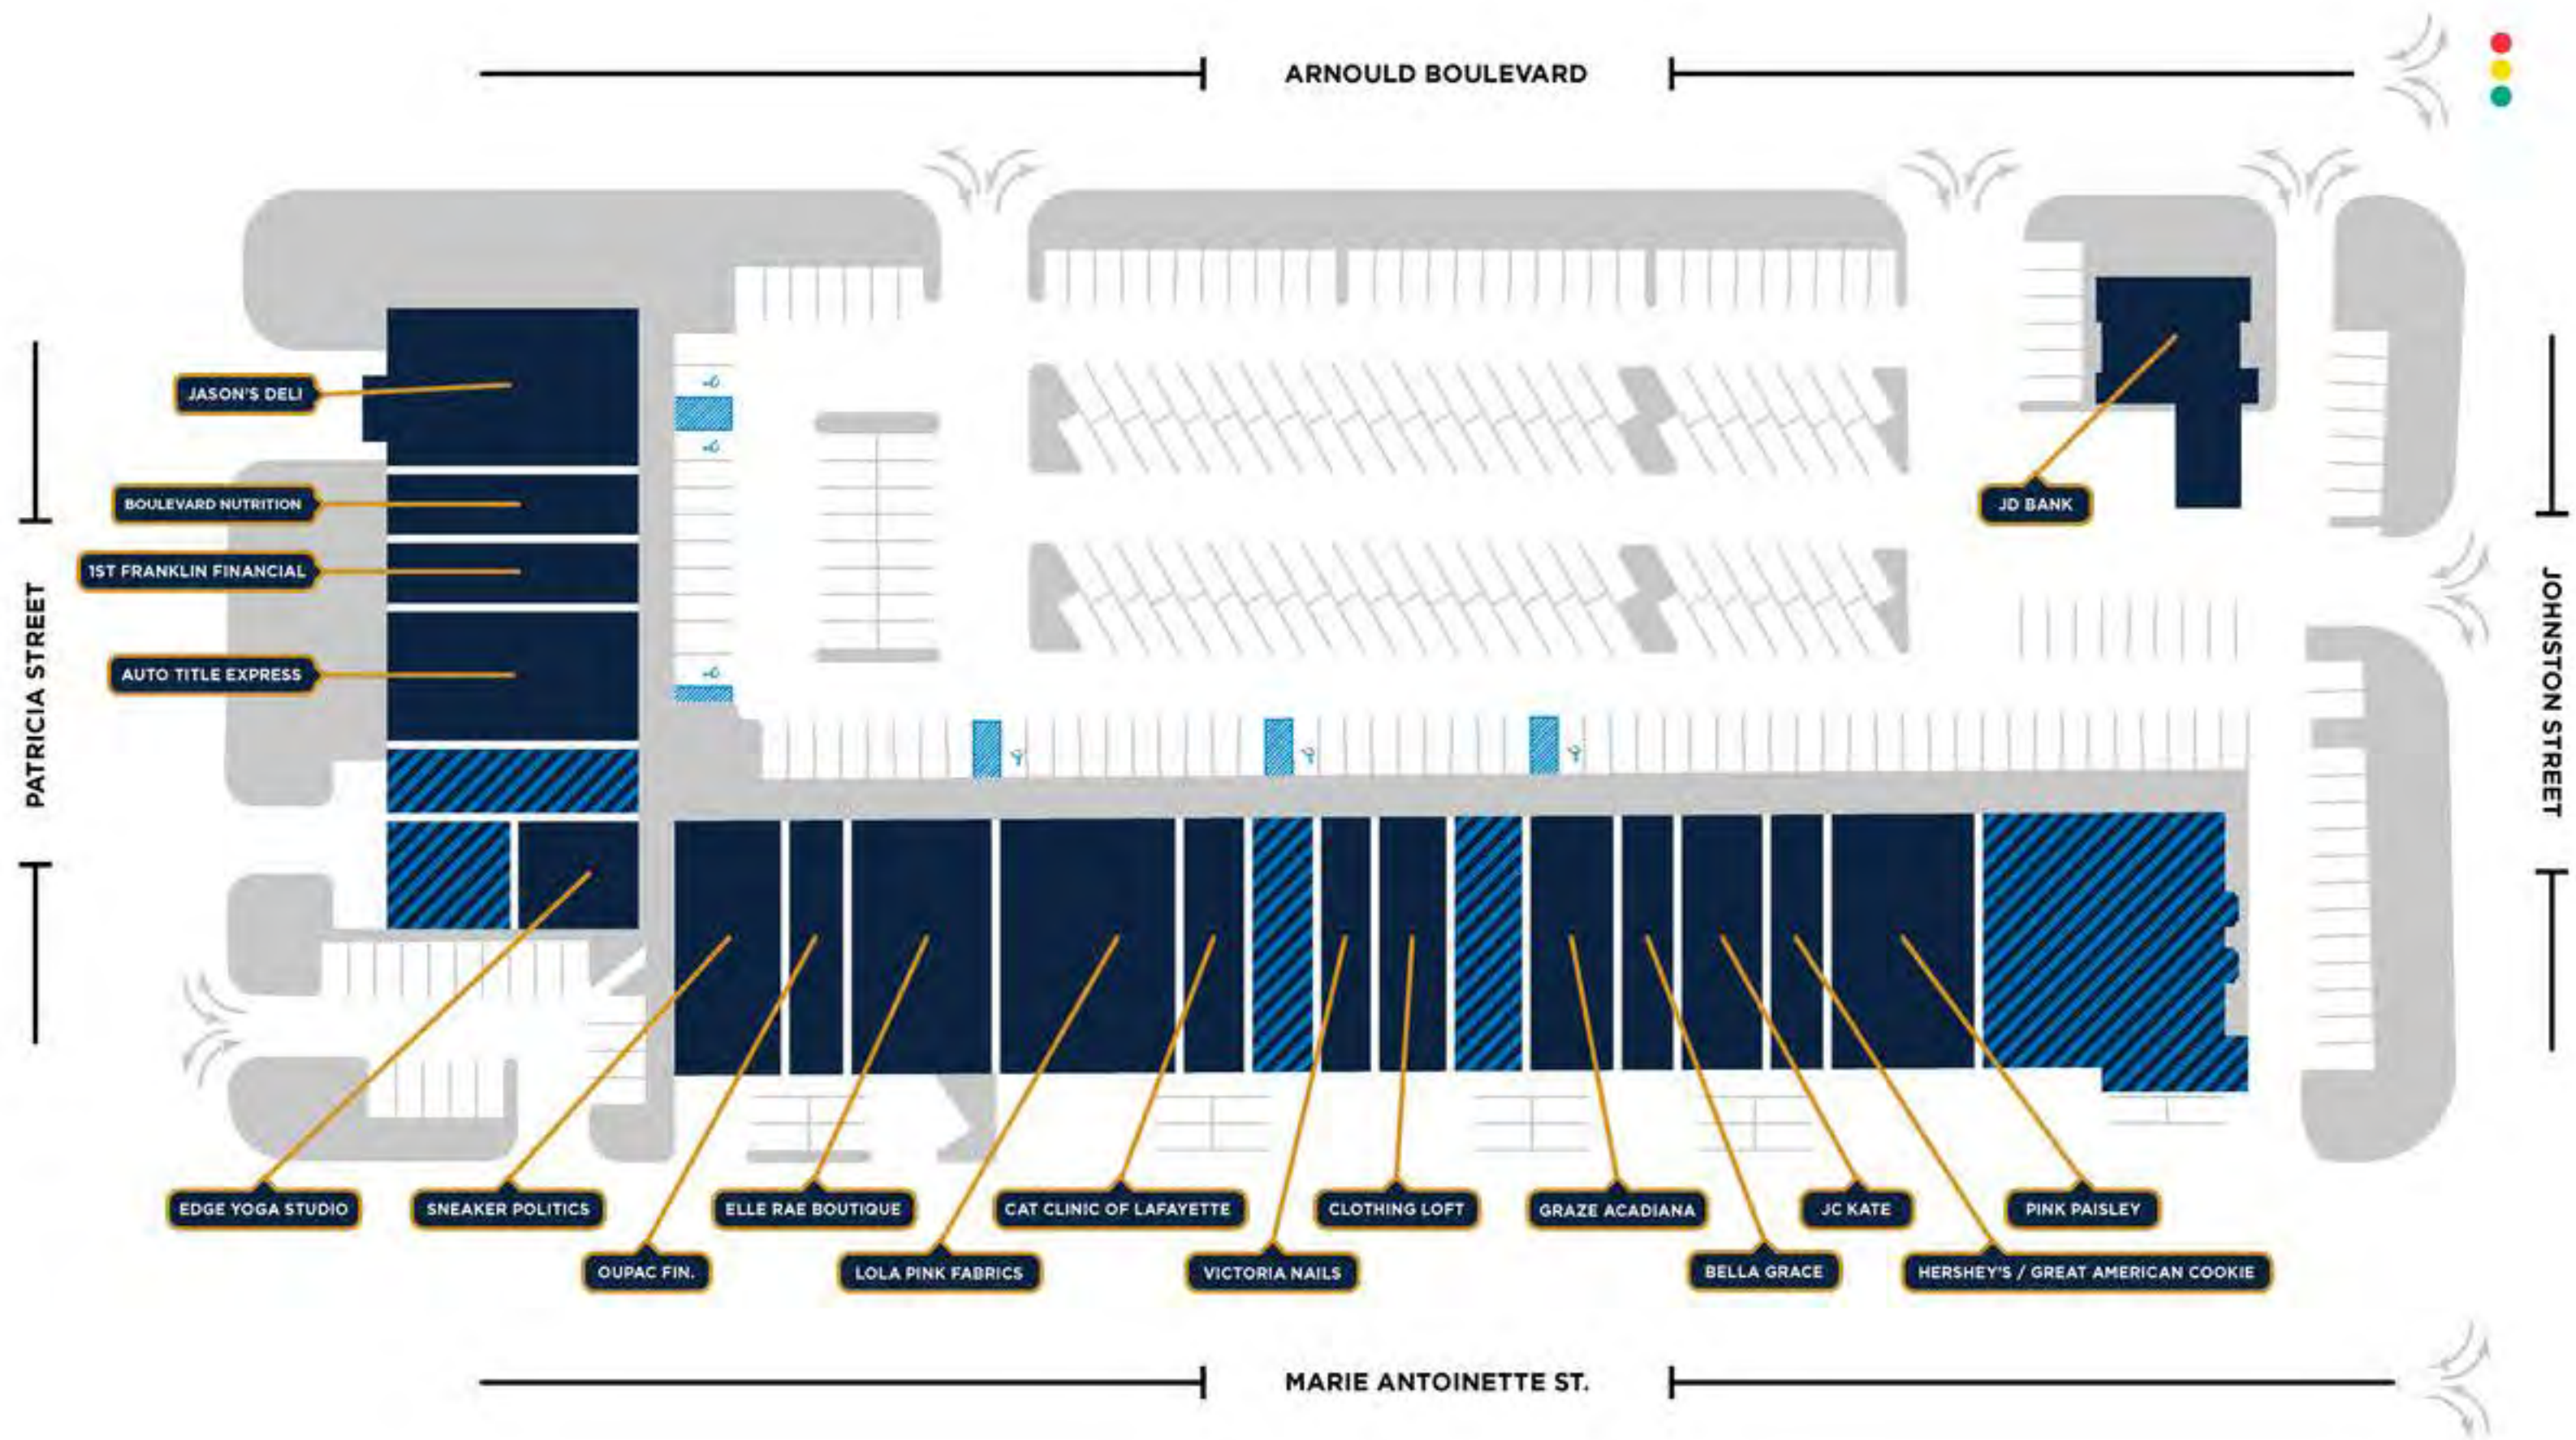


**On The Boulevard Shopping Center**  
**Belle Realty of Lafayette, LLC**  
**101 & 103 Arnould Blvd**

---

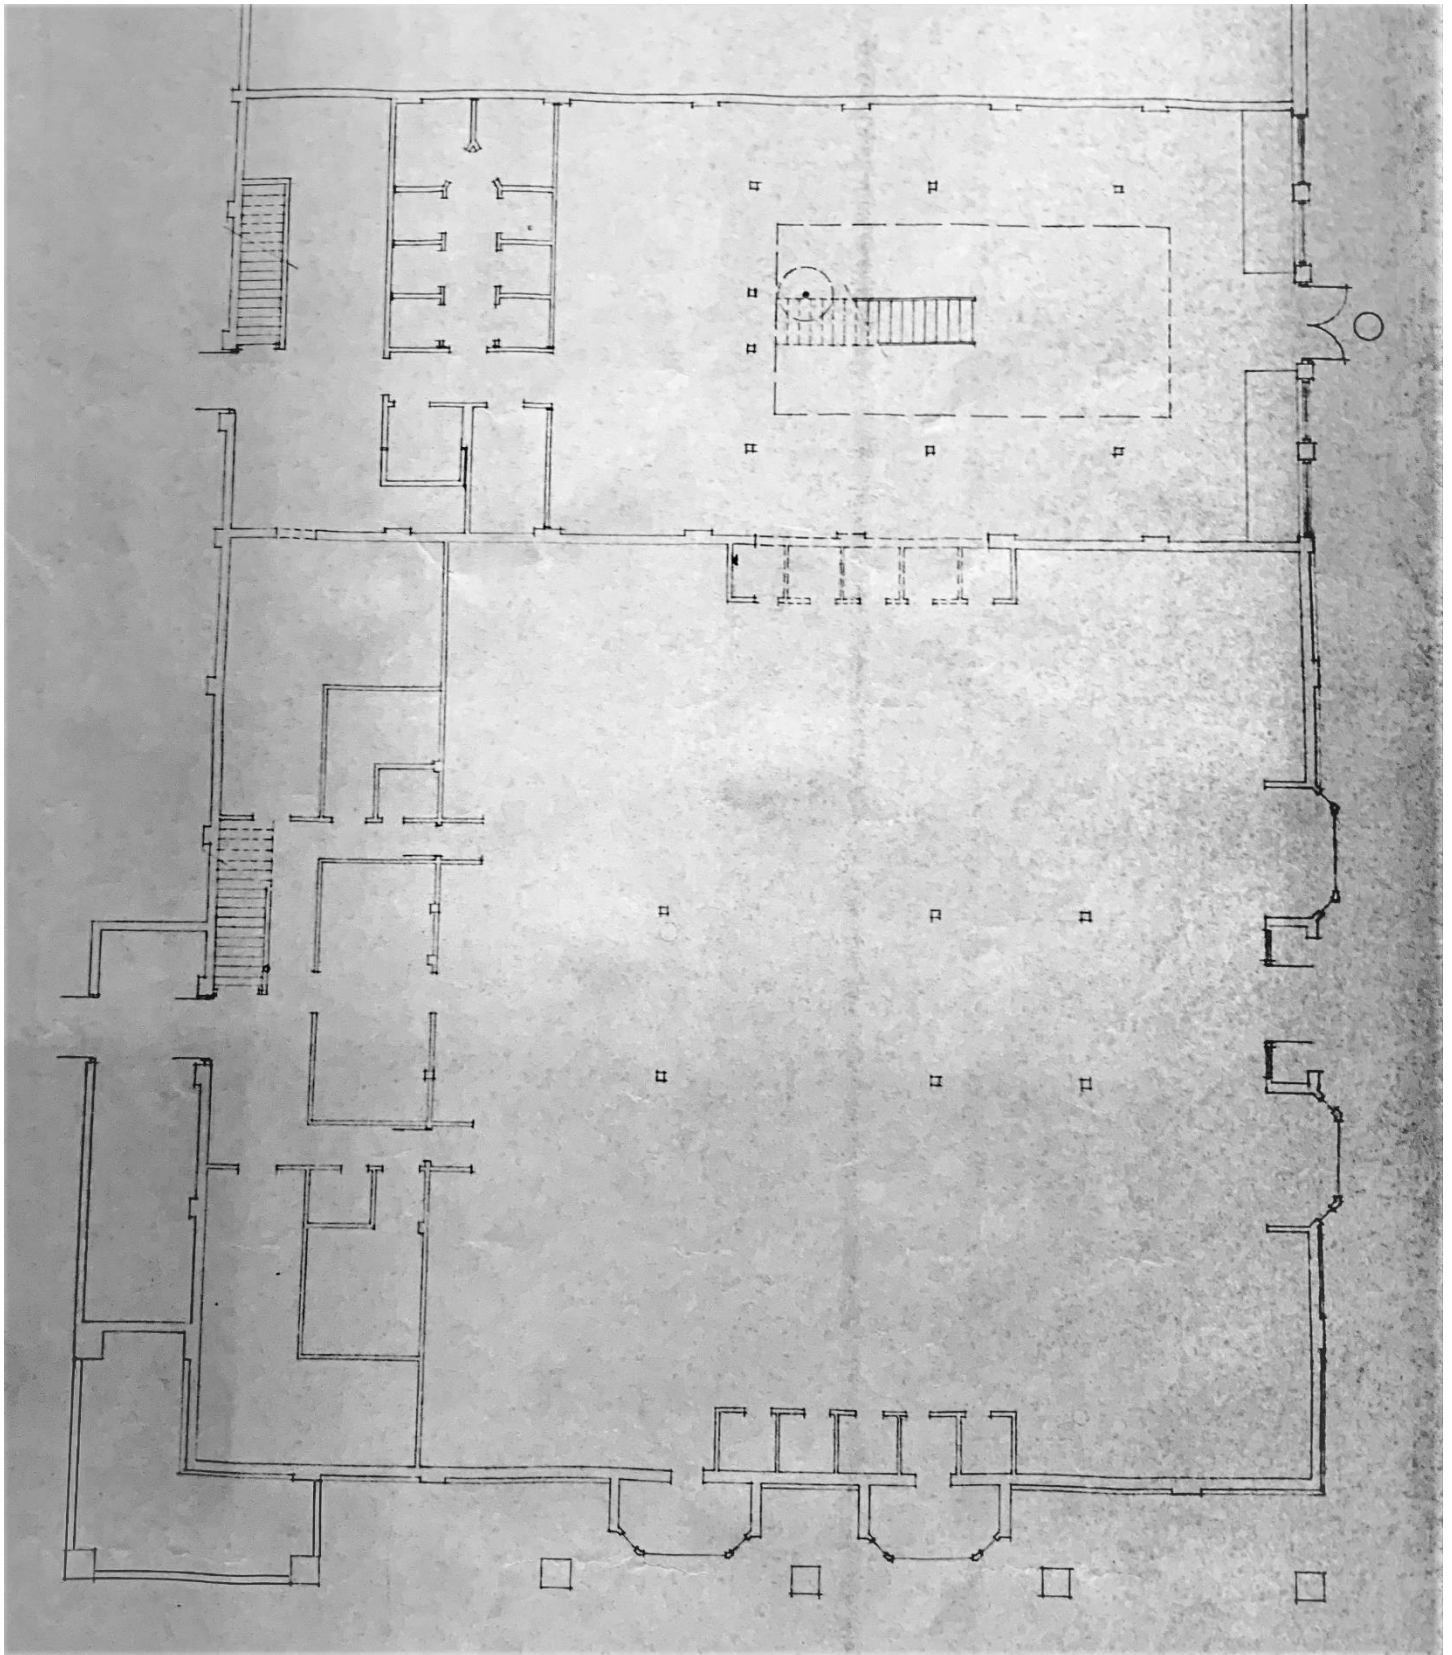


**On The Boulevard Shopping Center  
Belle Realty of Lafayette, LLC  
101 & 103 Arnould Blvd**


---

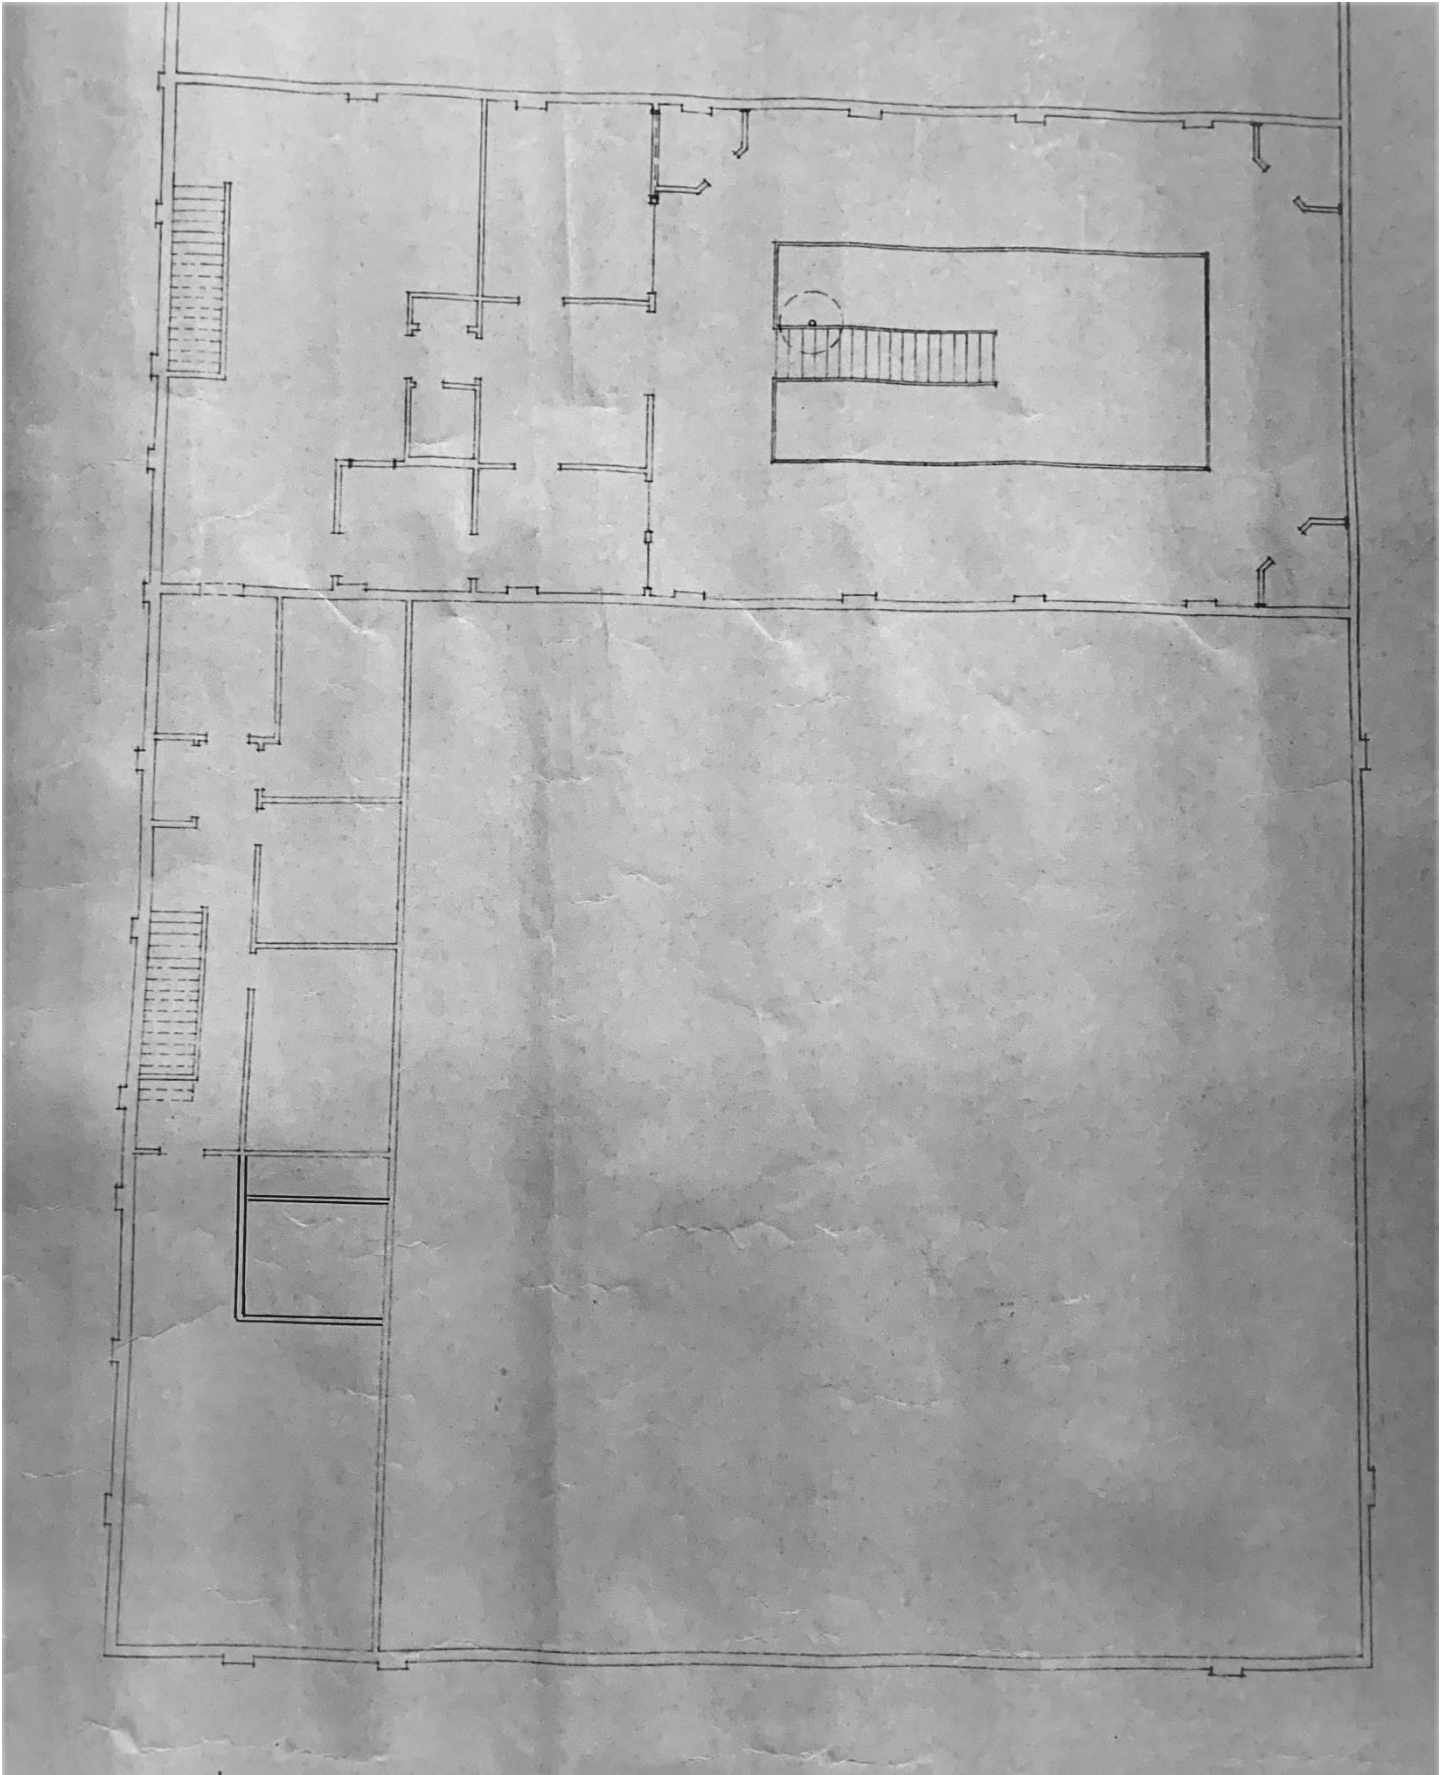



Site Plan Details:


- Building:** BROther's 6,877 Sq. Ft., BUILDING HEIGHT: 23.6'
- Parking:** Concrete Parking, 100.00' x 4.90', 2 SPACES
- Easements:**
  - 10' CITY OF LAFAYETTE ELECTRIC EASEMENT (ENTRY NO. 577566)
  - 5x5' GUY EASEMENT (10)
  - 10' UTILITY EASEMENT
- Adjacent Lots:** LOT 13, LOT 14, LOT 1
- Dimensions:**
  - BLD. HT. 13.5'
  - 108.00' (width)
  - 150.00' (length)
  - 85.45' (width)
  - 19.07' (width)
  - 66.77' (width)
  - 31.84' (width)
  - 49.65' (width)
  - 94.45' (width)
  - 100.00' (width)
  - 4.90' (width)
- Curved Dimensions:**
  - L=168', R=1872', CH=168', CB=S51°0'
  - L=48.65', R=30.00', CH=43.49', CB=N84°59'34"
- Other Labels:** LIQUOR PERMITTED THIS SIDE OF LINE, LIQUOR RESTRICTED THIS SIDE OF LINE, Apparent R/W Line, 12 SPACES, 2 SPACES, 8 SPACES, 10, 25, 14, 11/12

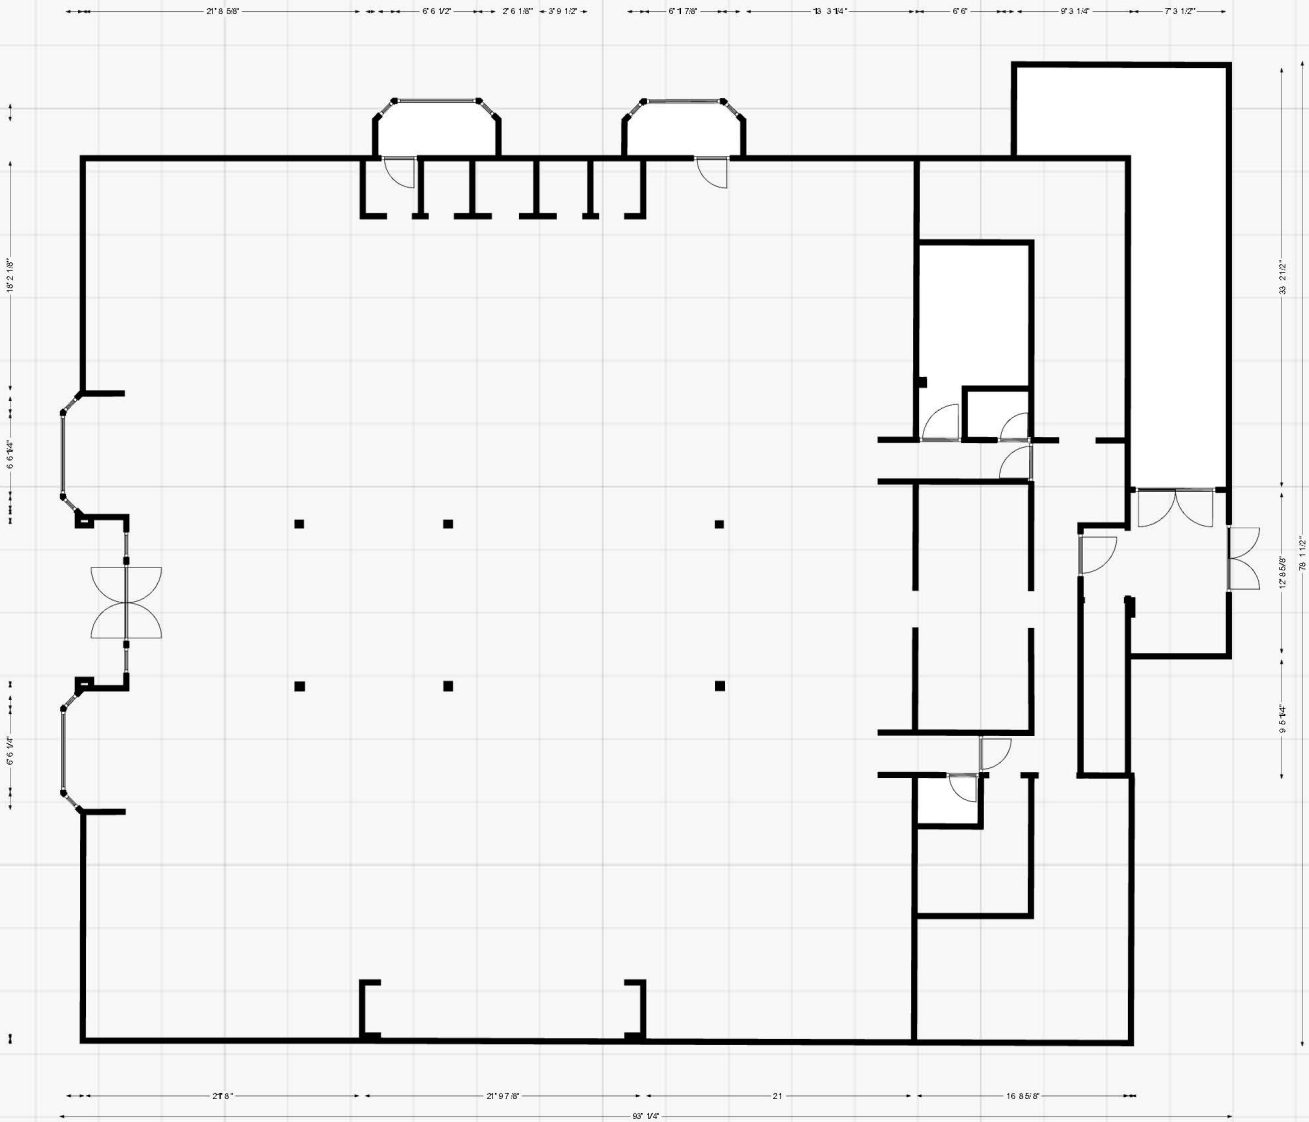

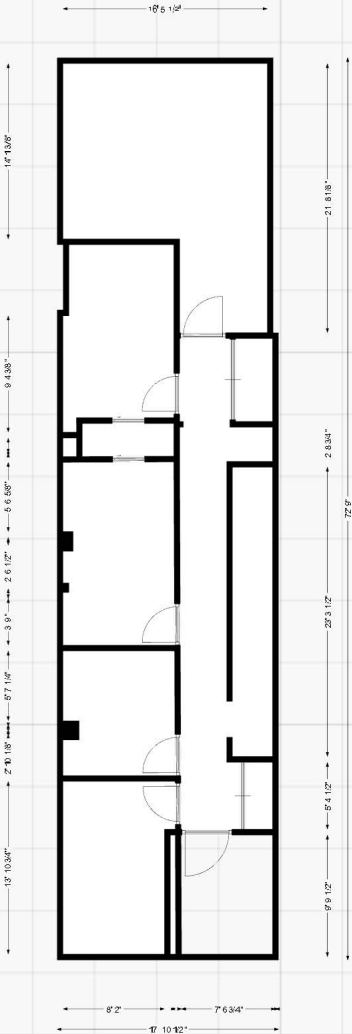

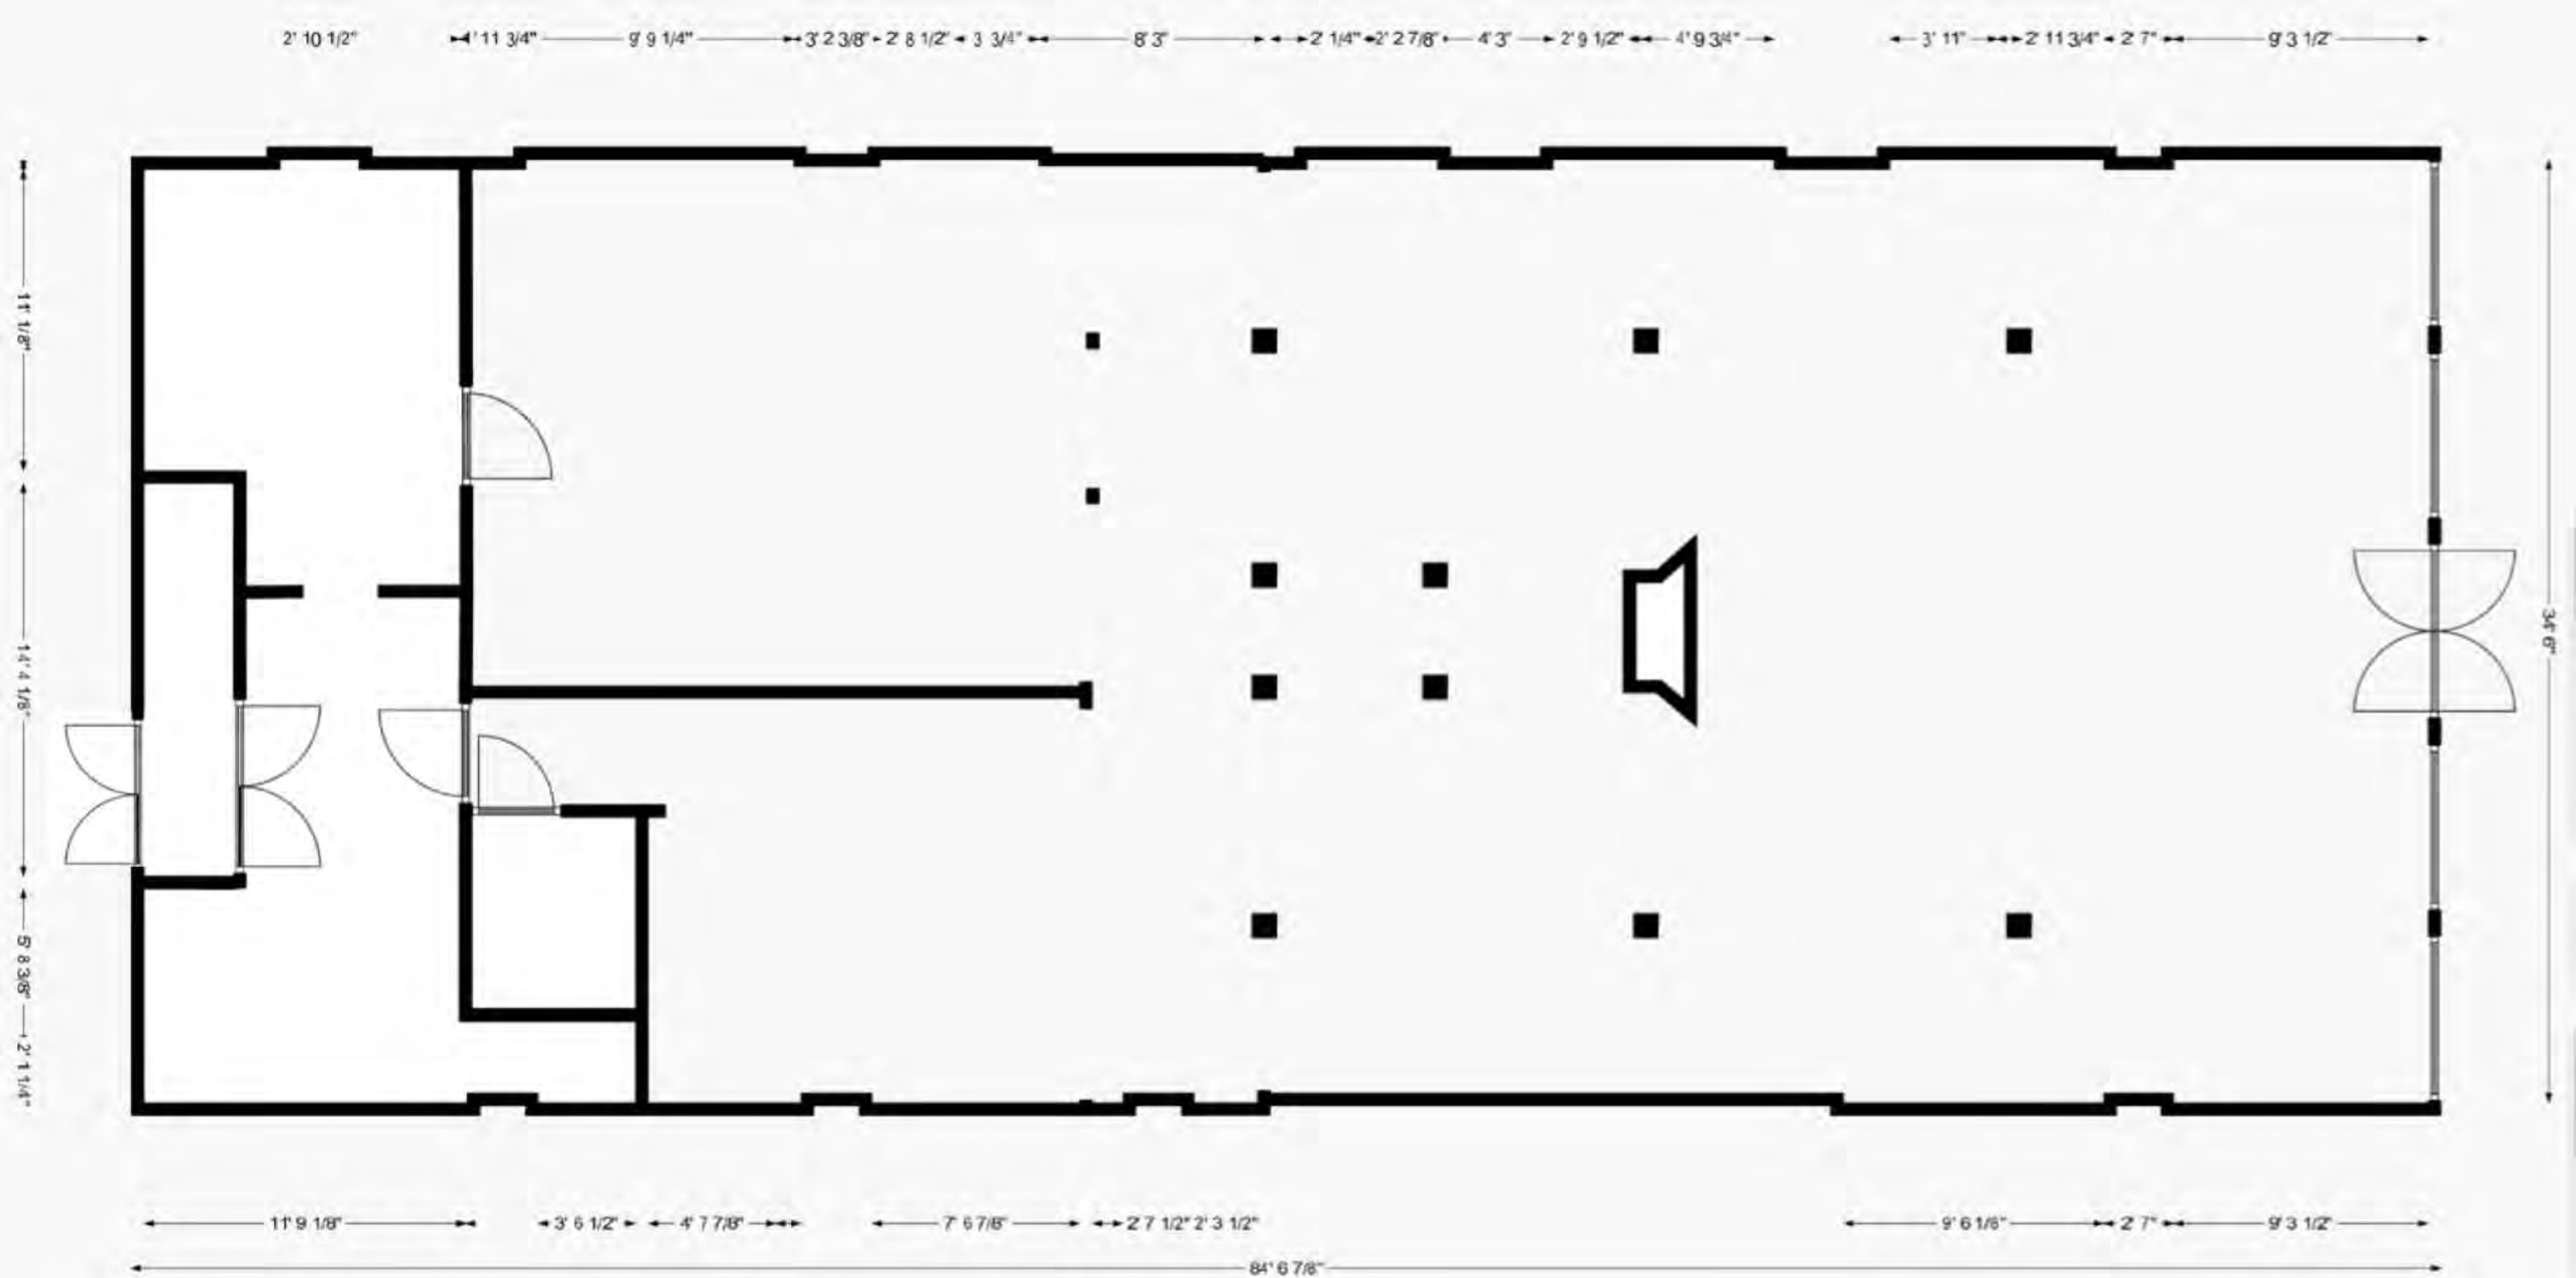

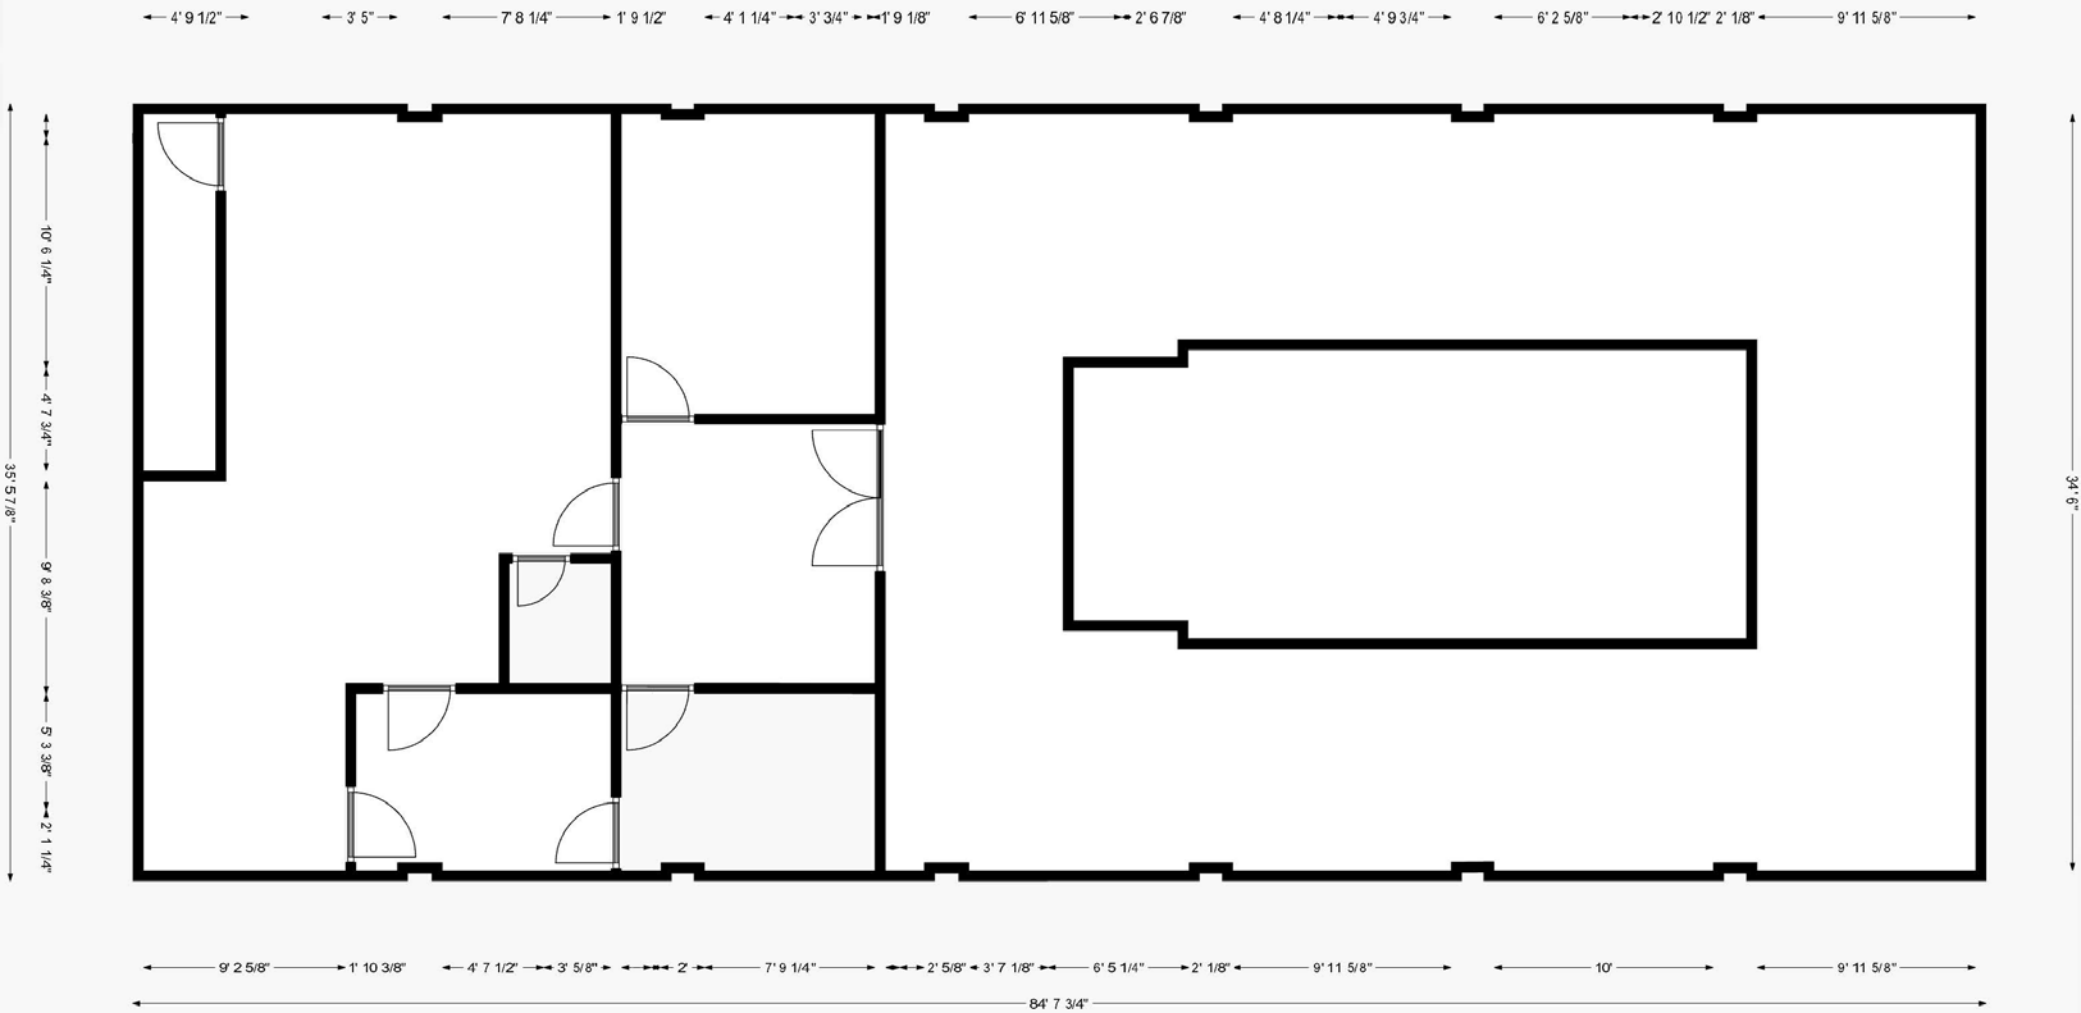

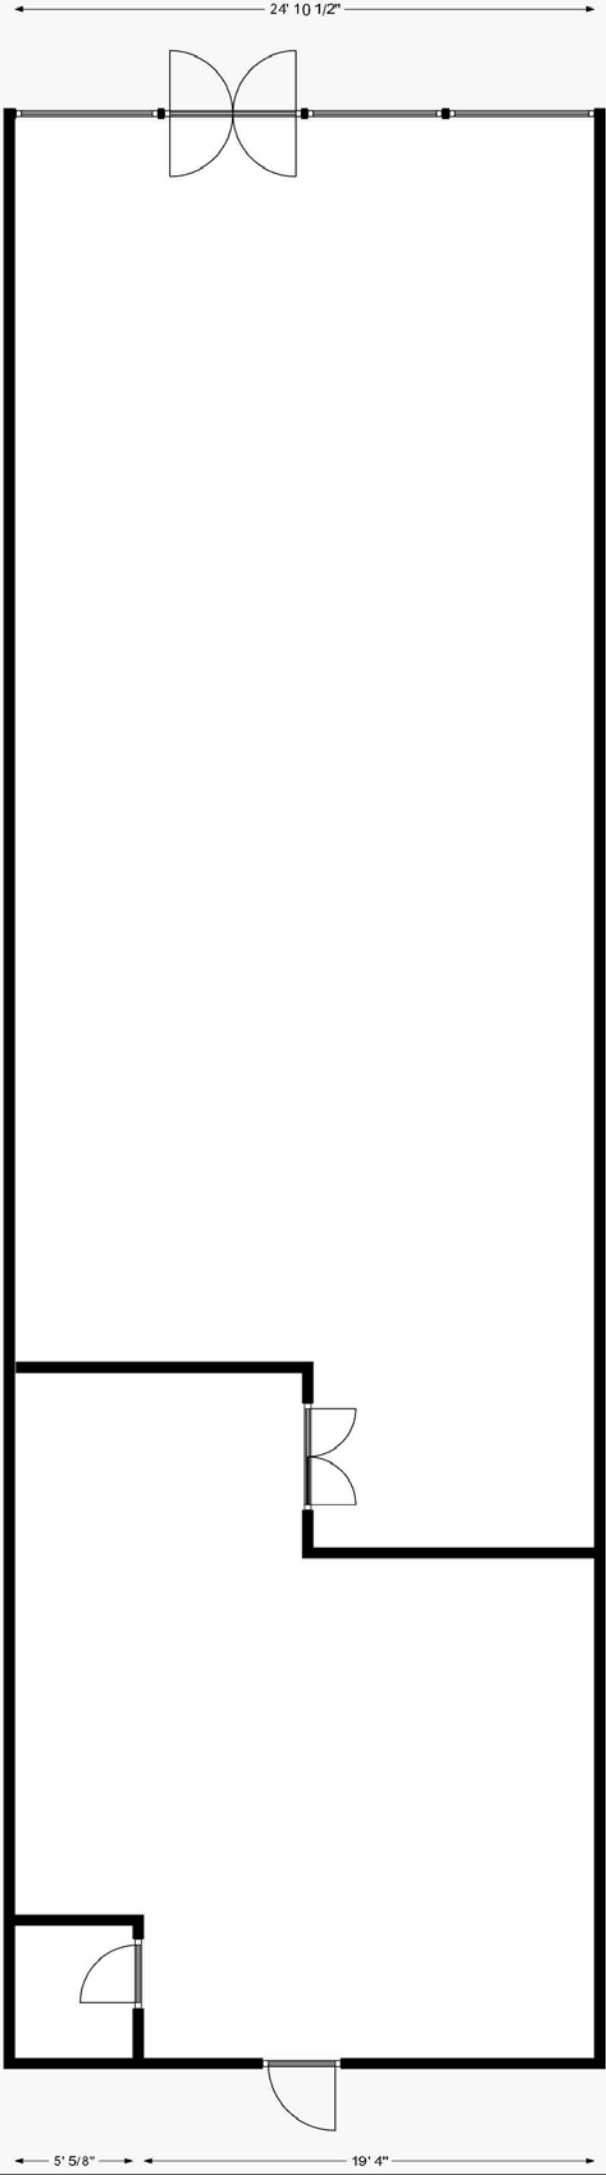

27' 7"

25' 10 5/8"

22' 9 3/8"

5' 8"

5' 5/8"

19' 4"

24' 10 1/2"

















