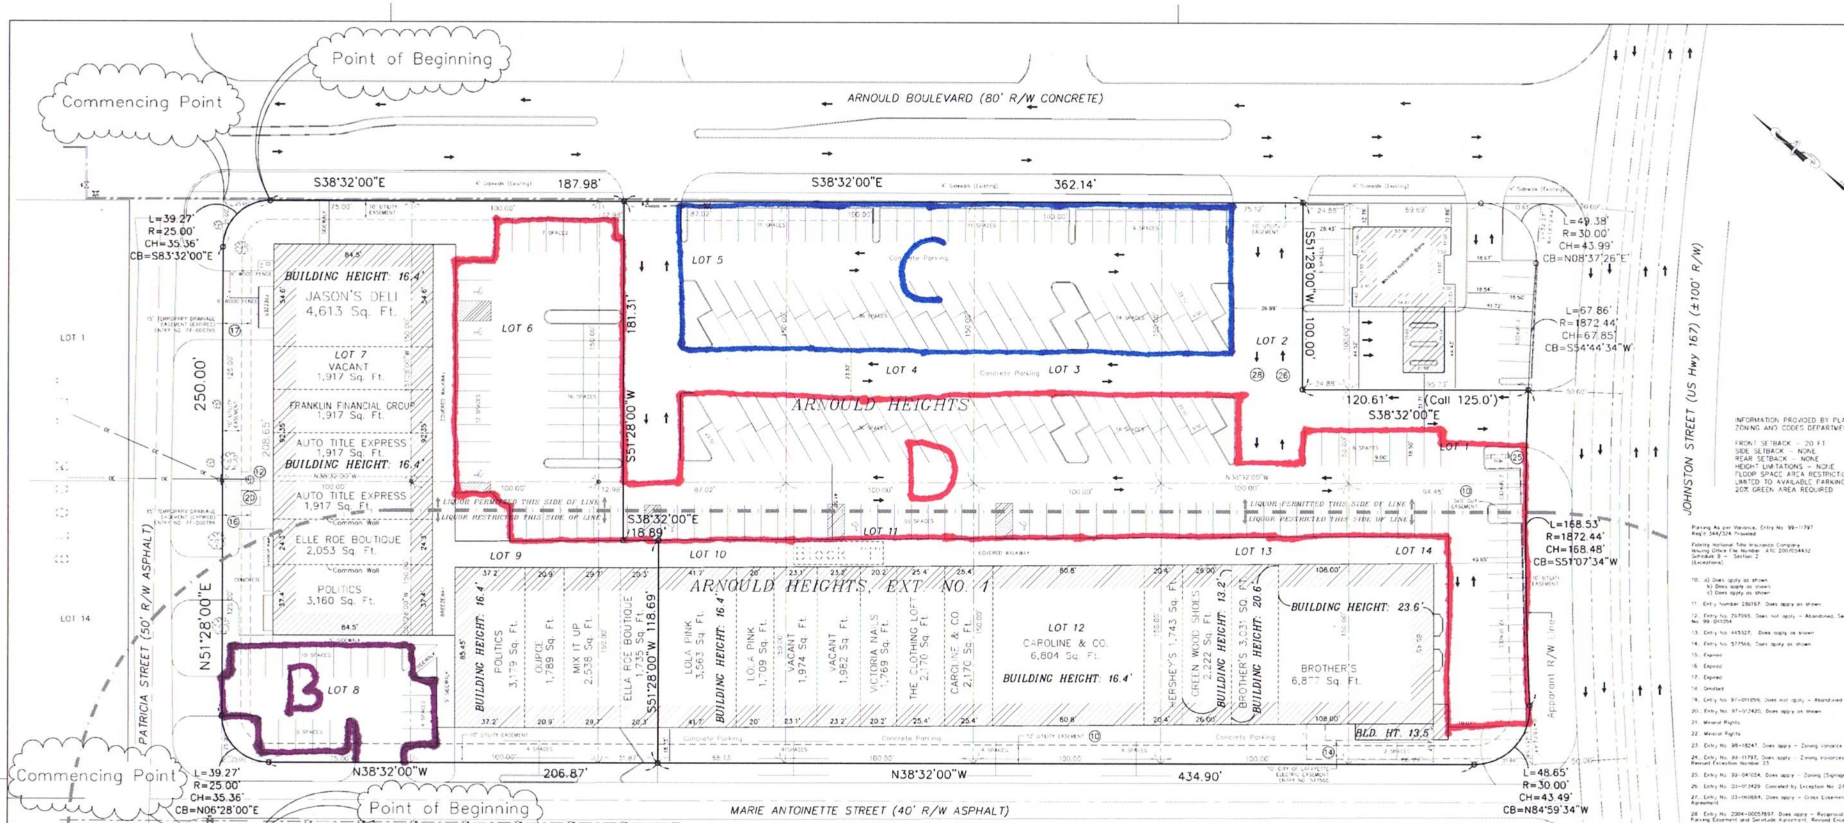
Commencing Point
Point of Beginning
ARNOULD BOULEVARD (80' R/W CONCRETE)
JOHNSTON STREET (US Hwy 167) (±100' R/W)
MARIE ANTOINETTE STREET (40' R/W ASPHALT)
PATRICIA STREET (50' R/W ASPHALT)
S38°32'00"E 187.98'
S38°32'00"E 362.14'
S51°28'00"W 100.00'
120.61' (Call 125.0')
S38°32'00"E
L=168.53' R=1872.44' CH=168.48' CB=S51°07'34"W
L=67.86' R=1872.44' CH=67.85' CB=S54°44'34"W
L=49.38' R=30.00' CH=43.99' CB=N08°37'26"E
L=48.65' R=30.00' CH=43.49' CB=N84°59'34"W
N38°32'00"W 434.90'
N38°32'00"W 206.87'
S51°28'00"W 118.69'
S38°32'00"E 18.89'
S51°28'00"W 181.31'
L=39.27' R=25.00' CH=35.36' CB=S83°32'00"E
L=39.27' R=25.00' CH=35.36' CB=N06°28'00"E
N51°28'00"E 250.00'
208.65'
LOT 1
LOT 2
LOT 3
LOT 4
LOT 5
LOT 6
LOT 7
LOT 8
LOT 9
LOT 10
LOT 11
LOT 12
LOT 13
LOT 14
C
D
B
ARNOULD HEIGHTS
ARNOULD HEIGHTS EXT. NO. 1
BLOCK I
BLOCK "M"
Arnould Hts. Subd. Ext. No 1
LIQUOR PERMITTED THIS SIDE OF LINE
LIQUOR RESTRICTED THIS SIDE OF LINE
Apparent R/W Line
Concrete Parking
BUILDING HEIGHT: 16.4'
JASON'S DELI 4,613 Sq. Ft.
LOT 7 VACANT 1,917 Sq. Ft.
FRANKLIN FINANCIAL GROUP 1,917 Sq. Ft.
AUTO TITLE EXPRESS 1,917 Sq. Ft.
AUTO TITLE EXPRESS 1,917 Sq. Ft.
ELLE ROE BOUTIQUE 2,053 Sq. Ft.
POLITICS 3,160 Sq. Ft.
POLITICS 3,179 Sq. Ft.
OUPCE 1,789 Sq. Ft.
MIX IT UP 2,538 Sq. Ft.
ELLA ROE BOUTIQUE 1,735 Sq. Ft.
LOLA PINK 3,563 Sq. Ft.
LOLA PINK 1,709 Sq. Ft.
VACANT 1,974 Sq. Ft.
VACANT 1,982 Sq. Ft.
VICTORIA NAILS 1,769 Sq. Ft.
THE CLOTHING LOFT 2,170 Sq. Ft.
CAROLINE & CO. 2,170 Sq. Ft.
CAROLINE & CO. 6,804 Sq. Ft.
HERSHEY'S 1,743 Sq. Ft.
GREEN WOOD SHOES 2,222 Sq. Ft.
BUILDING HEIGHT: 13.2'
BROTHER'S 3,031 Sq. Ft.
BUILDING HEIGHT: 20.6'
BUILDING HEIGHT: 23.6'
BROTHER'S 6,877 Sq. Ft.
BLD. HT. 13.5'
LOT 4
LOT 3
LOT 2
LOT 6
LOT 5
LOT 1
LOT 14

INFORMATION PROVIDED BY PLANNING, ZONING AND CODES DEPARTMENT:

FRONT SETBACK – 20 FT
SIDE SETBACK – NONE
REAR SETBACK – NONE
HEIGHT LIMITATIONS – NONE
FLOOR SPACE AREA RESTRICTIONS:
LIMITED TO AVAILABLE PARKING SPACES
20% GREEN AREA REQUIRED

Parking As per Variance, Entry No. 99-11797
Req'd 344/324 Provided

Fidelity National Title Insurance Company
Issuing Office File Number: ATC 2007054432
Schedule B – Section 2
(Exceptions)

10. a) Does apply as shown
    b) Does apply as shown
    c) Does apply as shown

11. Entry Number 286167: Does apply as shown

12. Entry No. 267095. Does not apply – Abandoned, See No. 25/Entry No. 99-041054

13. Entry No. 445327, Does apply as shown

14. Entry No. 577566, Does apply as shown

15. Expired

16. Expired

17. Expired

18. Omitted

19. Entry No. 97-011859, Does not apply – Abandoned

20. Entry No. 97-012420, Does apply as shown

21. Mineral Rights

22. Mineral Rights

23. Entry No. 98-18247, Does apply – Zoning Variance (Parking)

24. Entry No. 99-11797, Does apply – Zoning Variances (Parking) Revised Exception Number 23

25. Entry No. 99-041054, Does apply – Zoning (Signage)

26. Entry No. 03-013429: Canceled by Exception No. 27

27. Entry No. 03-060884, Does apply – Cross Easement and Servitude Agreement

28. Entry No. 2004-00057697, Does apply – Reciprocal Access and Parking Easement and Servitude Agreement. Revised Exception Number 26

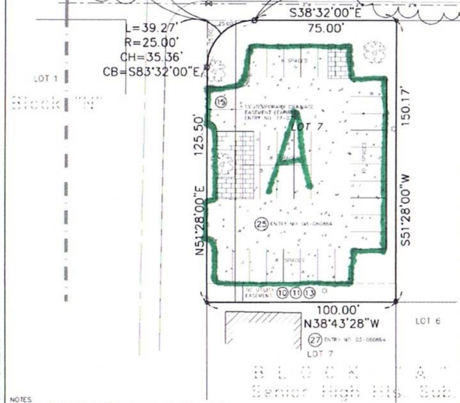

STATE OF LOUISIANA
LAFAYETTE PARISH

I, Andre E. Montagnet, a registered Professional Land Surveyor in the State of Louisiana of the firm of "Montagnet & Domingue, Inc.; Lafayette, LA; Telephone #337-981-2130", hereby certify that the premises shown hereon is a true and correct plat of the property described hereon; that the buildings thereon are located with respect to property boundaries as shown; that there are no electric or telephone wires or structures or supports therefor on or over said premises except as shown; that all Rights-of-way, Easements or joint drives over or across said premises visible on the surface are shown; that the premises surveyed do not encroach on the adjoining property and that the adjoining property does not encroach on the premises surveyed except as shown. I further certify that I have consulted Federal Insurance Administration Flood Hazard Boundary Maps as are currently available and have found that the subject property DOES NOT lie in a Special Flood Hazard Area.

WITNESS my hand this the 2nd day of May, 2007.
Andre E. Montagnet, P.L.S.
LA Reg. No.4484

LEGAL DESCRIPTION

A parcel of Ground located in Section 42, Township 10 South, Range 4 East, Lafayette Parish, Louisiana, within the City Limits of City of Lafayette and being a portion of the formally dedicated Block I of Arnould Heights Subdivision and Block I of Arnould Heights Extension No. 1.

Commencing at the Southwest Right-of-Way corner of intersection of Arnould Boulevard and Patricia Street thence South 38°32'00" East a distance of 25.00 feet to the Point of Beginning.

Thence South 38°32'00" East a distance of 550.12 feet; thence South 51°28'00" West a distance of 100.00 feet; thence South 38°32'00" East a distance of 120.61 feet; thence along a curved line to the Left having a radius of 1,872.44 feet, Length of 168.53 feet and a chord of South 51°07'34" West with a distance of 168.48 feet; thence along a curved line to the Right having a radius of 30.00 feet, Length of 48.65 feet and a chord of North 84°59'34" West a distance of 43.49 feet; thence North 38°32'00" West a distance of 641.77 feet; thence along a curved line to the Right having a Radius of 25.00 feet, Length of 39.27 feet and a chord of North 06°28'00" East a distance of 35.36 feet; thence North 51°28'00" East a distance of 250 feet; thence along a curved line to the Right having a Radius of 25.00 feet, Length of 39.27 feet and a chord of South 83°32'00" East a distance of 35.36 feet to the Point of Beginning.

LOT 7, BLOCK M, ARNOULD HEIGHTS SUBDIVISION, EXT. NO. 1 A parcel of ground located in Section 42, Township 10 South, Range 4 East, Lafayette Parish, Louisiana, within the City of Lafayette being more particularly described as follows:

Commencing at the southwestern right-of-way corner of the intersection of Marie Antoinette Street and Patricia Street, thence South 38°32'00" East a distance of 25.00 feet to the Point of Beginning.

Thence South 38°32'00" East a distance of 75.00 feet; thence South 51°28'00" West a distance of 150.17 feet, thence North 38°43'28" West a distance of 100.00 feet; thence North 51°28'00" East a distance of 125.50 feet; thence along a curve to the right having a radius of 25.00 feet, an arc length of 39.27 feet, and a chord of South 83°32'00" East and a distance of 35.36 feet to the Point of Beginning.

NOTES:
BUILDING HEIGHT EXCLUDES FACADE WHICH IS APPROX. 23.6'

"THIS SURVEY WAS CONDUCTED BY ME OR UNDER MY DIRECT SUPERVISION BASED ON STANDARDS FOR CLASS C SURVEYS IN ACCORDANCE WITH THE MINIMUM STANDARDS FOR PROPERTY BOUNDARY SURVEYS AS ADOPTED BY THE BOARD OF REGISTRATION FOR PROFESSIONAL ENGINEERS AND LAND SURVEYORS.

THIS PROPERTY IS NOT LOCATED IN A FLOOD HAZARD AREA ACCORDING TO THE F.E.M.A. FLOOD INSURANCE RATE MAP DATED DECEMBER 21, 2018 (ZONE X) Community Panel No. 22055C0160 J.

Boulev.dwg 71919 102230

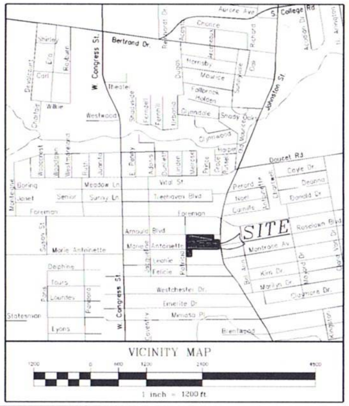

VICINITY MAP

LOT 1

TYPES OF IMPROVEMENTS
WATER ------ LUS
SEWER ------ LUS
ELECTRIC ---- LUS
TELEPHONE --- BELL SOUTH
DRAINAGE --- OPEN DITCH (EXISTING)
ROADWAY --- EXISTING ASPHALT

GENERAL NOTES
TOTAL NUMBER OF BUILDINGS --- 2
TOTAL AREA OF BUILDINGS ----- 62,883 SQ. FT.
TOTAL AREA OF DEVELOPMENT --- 4.84 ACRES
MINIMUM FRONTAGE ------------ 75.00'
ZONE ------------------------ CH
PARKING SPACES -------------- 324
⑪ -------------------------- DENOTES TITLE EXCEPTION NO.

GRAPHIC SCALE
30 0 15 30 60 120
(IN FEET)
1 inch = 30 ft

10	7/19/19	UPDATED TENANTS, ZONING, FLOOD MAP	A.E.M.
9	12/29/08	UPDATED COMPANIES	A.E.M.
8	06/03/08	LIQUOR LINE	A.E.M.
7	05/02/07	EXCEPTIONS ADDED/LEGAL UPDATED	A.E.M.
6	04/02/07	ADDED TOPO & UPTDATED CO.	A.E.M.
5	06/23/99	CHANGED NAME IN TITLE BLOCK	A.E.M.
4	04/08/98	REVISED BUILDING DIMENSIONS	A.E.M.
3	03/26/98	ADDED PARKING LOT 7	R.J.D.
2	02/25/98	ADDED BUILDINGS & PARKING	R.J.D.
1	06/03/94	PROP. LINES & LOTS PER REPLAT	R.J.D.

REVISIONS

A. E. MONTAGNET
REG. No. 4484
REGISTERED PROFESSIONAL LAND SURVEYOR

AN ALTA/ACSM SURVEY FOR
BELLE REALTY OF LAFAYETTE, LLC
BEING LOTS 1-3, 1-14, PARTITION OF
LOTS 1 & 2, BLOCK I, LOT 7, BLOCK M
ARNOULD HEIGHTS SUBDIVISION, EXT. NO. 1
STREET ADDRESS: ARNOULD BLVD.
LAFAYETTE, LA 70506
LOCATED IN THE CITY OF LAFAYETTE
LAFAYETTE PARISH, LOUISIANA

PREPARED BY: A. E. Montagnet
ANDRE' E. MONTAGNET
P. L. S. NO. 4484
C. E. NO. 18687

MONTAGNET AND DOMINGUE, INC.
136 CLARA VON DRIVE
LAFAYETTE, LOUISIANA 70503
Phone: (337)981-2130 Fax: (337)981-3282
DATE: MAY 20, 1994 SCALE: 1"=30'
LAST REVISED DATE: JULY 19, 2019