


Sign A	37" Jason's Deli
Type:	Single-Face Wall Sign
Illumination:	Internally Illuminated w/ LED's
Square Footage:	104.30
To Grade:	Top of sign to grade = 19'-6" Bottom of sign to grade = 13'-3"

Sign B	37" Jason's Deli
Type:	Single-Face Wall Sign
Illumination:	Internally Illuminated w/ LED's
Square Footage:	104.30
To Grade:	Top of sign to grade = 19'-6" Bottom of sign to grade = 13'-3"

SIGN C	Jason's Deli
Sign Type:	New Lexan panel w/ Applied Vinyl
Actual Size:	48" X 96"
Viewable Size:	45" x93"
Square Footage:	32.00

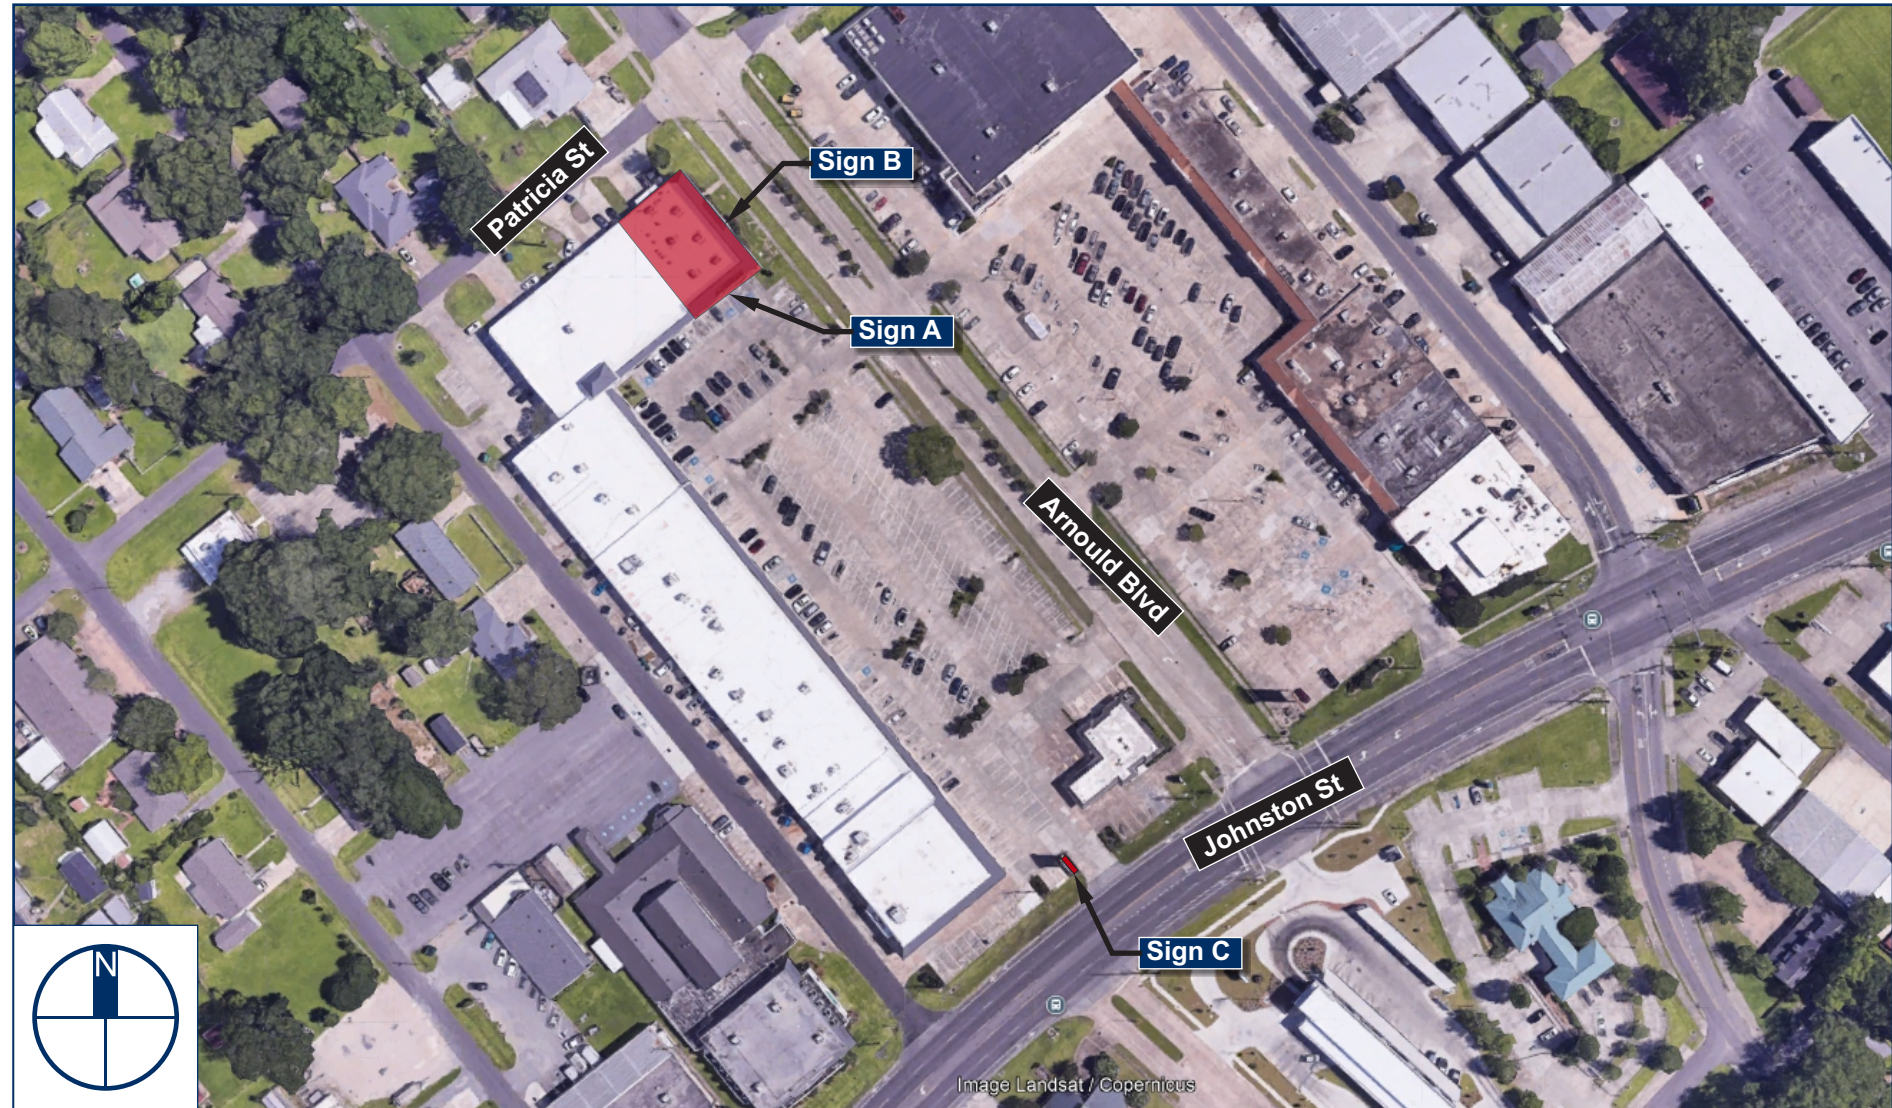

Client: Jason's Deli
Site #: JD-54
Address: 149 Arnould Boulevard
Lafayette, LA 70506

REVISION INFO

11/05/2024	Original Rendering	AB

This rendering is the property of Anchor Sign, Inc. It is for the exclusive use of Anchor Sign, Inc. and the party which requested the rendering. It is an unpublished original drawing not to be distributed, reproduced or exhibited without the consent of Anchor Sign, Inc. Please contact your account manager with questions regarding this statement.

 **AnchorSign**[®]
1.800.213.3331

Sign A	37" Jason's Deli
Type:	Single-Face Wall Sign
Illumination:	Internally Illuminated w/ LED's
Square Footage:	104.30
To Grade:	Top of sign to grade = 19'-6" Bottom of sign to grade = 13'-3"



Existing



Front Elevation (Southeast)
Scale: 1/8" = 1'-0"

Allowable Square Footage this Elevation:	104.30
Formula:	
Actual Square Footage this Elevation:	104.30



Client: Jason's Deli

Site #: JD-54

Address: 149 Arnould Boulevard
Lafayette, LA 70506

REVISION INFO

11/05/2024	Original Rendering	AB

This rendering is the property of Anchor Sign, Inc. It is for the exclusive use of Anchor Sign, Inc. and the party which requested the rendering. It is an unpublished original drawing not to be distributed, reproduced or exhibited without the consent of Anchor Sign, Inc. Please contact your account manager with questions regarding this statement.



1.800.213.3331

Sign B	37" Jason's Deli
Type:	Single-Face Wall Sign
Illumination:	Internally Illuminated w/ LED's
Square Footage:	104.30
To Grade:	Top of sign to grade = 19'-6" Bottom of sign to grade = 13'-3"



Existing



Left Elevation (Northeast)
Scale: 3/16" = 1'-0"

Allowable Square Footage this Elevation:	104.30
Actual Square Footage this Elevation:	104.30



Client: Jason's Deli

Site #: JD-54

Address: 149 Arnould Boulevard
Lafayette, LA 70506

REVISION INFO


11/05/2024	Original Rendering	AB

This rendering is the property of Anchor Sign, Inc. It is for the exclusive use of Anchor Sign, Inc. and the party which requested the rendering. It is an unpublished original drawing not to be distributed, reproduced or exhibited without the consent of Anchor Sign, Inc. Please contact your account manager with questions regarding this statement.



1 . 8 0 0 . 2 1 3 . 3 3 3 1

Sign A	37" Jason's Deli
Type:	Single-Face Wall Sign
Illumination:	Internally Illuminated w/ LED's
Square Footage:	104.30
To Grade:	Top of sign to grade = 19'-6" Bottom of sign to grade =13'-3"

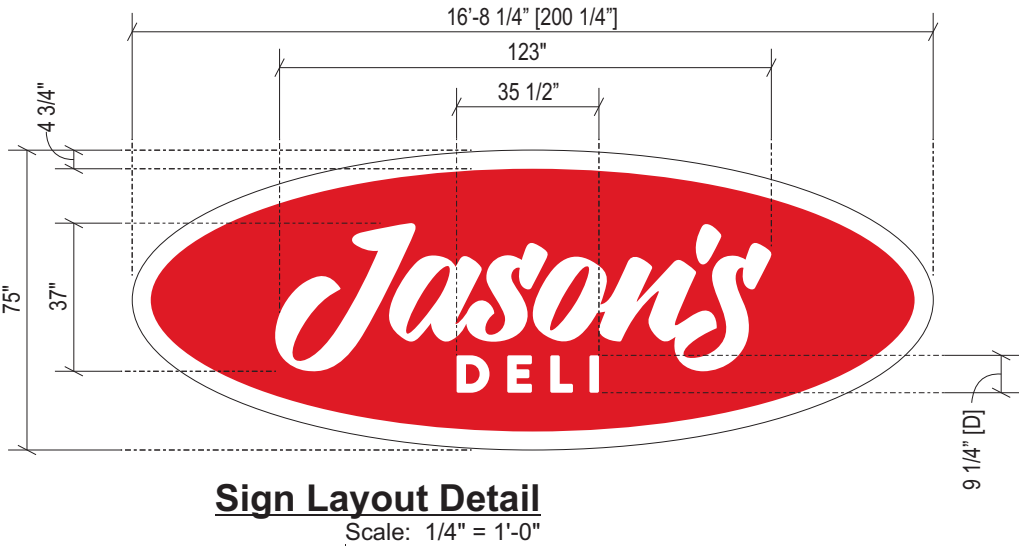


Electrical:
White LEDs (GE MiniMax)
(X) 60w Transformer @ 1.1 Amps Each
Total Amps: X.X
(1) 20 amp 120V Circuit Req.



General Notes:
This sign is to be installed in accordance with the requirements of Article 600 of the National Electrical Code.
1) Grounded and bonded per NEC 600.7/NEC 250
2) Existing branch circuit in compliance with NEC 600.5, not to exceed 20 amps
3) Sign is to be UL listed per NEC 600.3
4) UL disconnect switch per NEC 600.6- required per sign component before leaving manufacturer*
*For multiple signs, a disconnect is permitted but not required for each section


Specifications: Wall Sign, Lexan Face
1. Facade: Wood siding Wood
2. Cabinet: Aluminum frame wrapped in 0.080" aluminum sign cabinet painted to match PMS 3517c Red
3. 2" x 2" Aluminum angle retainers painted to match Matthews N202 White
4. White 3/16" lexan face with first surface applied vinyl: ■ 3M 3630-33 Red with applied matte laminate
5. Sign cabinet contains White LEDs and self contained power supplies
6. Disconnect switch UL Outdoor rated toggle type w/ neoprene boot per NEC 600-6
7. Primary electrical feed
8. Mounting hardware: 3/8" Thru Bolts

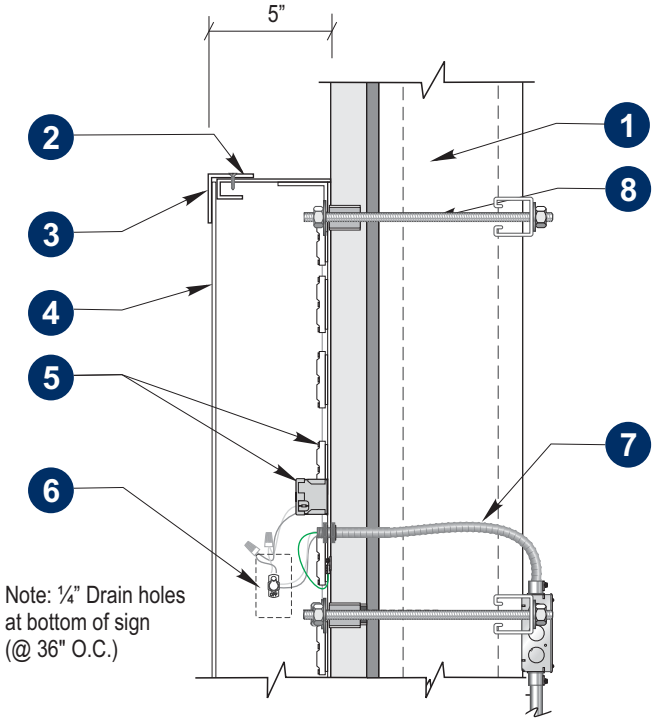

Section @ S/F Wall Sign
LED Illum Scale: N.T.S.

	Client:	Jason's Deli	REVISION INFO	11/05/2024	Original Rendering	AB	This rendering is the property of Anchor Sign, Inc. It is for the exclusive use of Anchor Sign, Inc. and the party which requested the rendering. It is an unpublished original drawing not to be distributed, reproduced or exhibited without the consent of Anchor Sign, Inc. Please contact your account manager with questions regarding this statement.
	Site #:	JD-54					
	Address:	149 Arnould Boulevard					
		Lafayette, LA 70506					
						 1.800.213.3331	

Sign B	37" Jason's Deli
Type:	Single-Face Wall Sign
Illumination:	Internally Illuminated w/ LED's
Square Footage:	104.30
To Grade:	Top of sign to grade = 19'-6" Bottom of sign to grade = 13'-3"

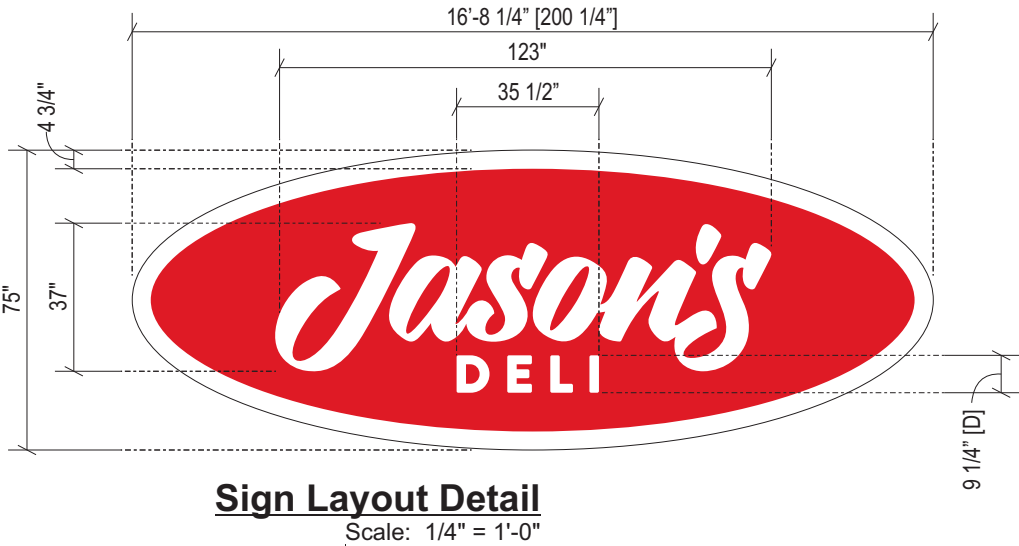


Electrical:
White LEDs (GE MiniMax)
(X) 60w Transformer @ 1.1 Amps Each
Total Amps: X.X
(1) 20 amp 120V Circuit Req.



General Notes:
This sign is to be installed in accordance with the requirements of Article 600 of the National Electrical Code.
1) Grounded and bonded per NEC 600.7/NEC 250
2) Existing branch circuit in compliance with NEC 600.5, not to exceed 20 amps
3) Sign is to be UL listed per NEC 600.3
4) UL disconnect switch per NEC 600.6- required per sign component before leaving manufacturer*
*For multiple signs, a disconnect is permitted but not required for each section

Specifications: Wall Sign, Lexan Face
1. Facade: Wood siding Wood
2. Cabinet: Aluminum frame wrapped in 0.080" aluminum sign cabinet painted to match PMS 3517c Red
3. 2" x 2" Aluminum angle retainers painted to match Matthews N202 White
4. White 3/16" lexan face with first surface applied vinyl: ■ 3M 3630-33 Red with applied matte laminate
5. Sign cabinet contains White LEDs and self contained power supplies
6. Disconnect switch UL Outdoor rated toggle type w/ neoprene boot per NEC 600-6
7. Primary electrical feed
8. Mounting hardware: 3/8" Thru Bolts

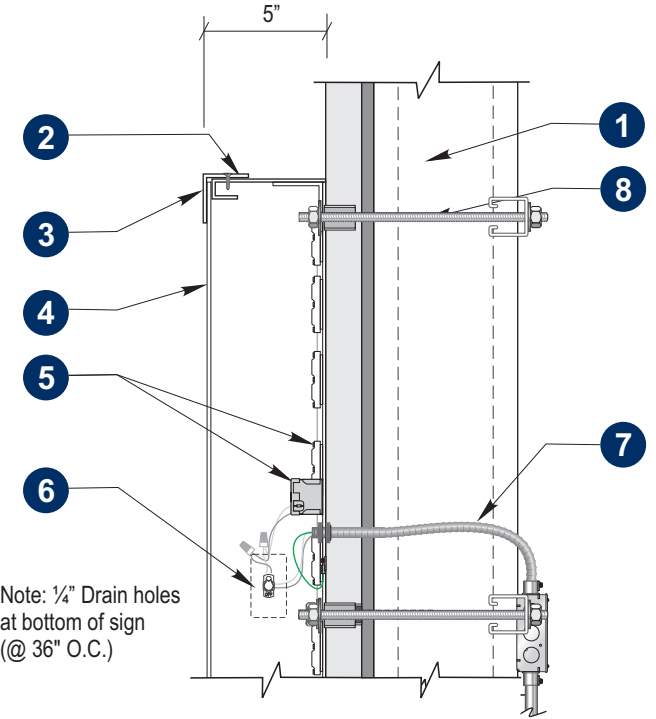

Section @ S/F Wall Sign
LED Illum Scale: N.T.S.

	Client:	Jason's Deli	REVISION INFO	11/05/2024	Original Rendering	AB	This rendering is the property of Anchor Sign, Inc. It is for the exclusive use of Anchor Sign, Inc. and the party which requested the rendering. It is an unpublished original drawing not to be distributed, reproduced or exhibited without the consent of Anchor Sign, Inc. Please contact your account manager with questions regarding this statement.
	Site #:	JD-54					
	Address:	149 Arnould Boulevard					
		Lafayette, LA 70506					
							 1.800.213.3331

SIGN C	Jason's Deli
Sign Type:	New Lexan panel w/ Applied Vinyl
Actual Size:	48" X 96"
Viewable Size:	45" x93"
Square Footage:	32.00



Panel Replacement on Existing D/F Pylon
QTY 2 (1 SET)

Scale: 3/8" = 1'-0"

Specifications:	
1.	New White Lexan panels
2.	First surface applied vinyl
	3M 3630-33 Red
3.	Retainers: Top and sides: 2" Bottom: 1-1/4"



Existing



Multi-Tenant Pylon Elevation

Scale: N.T.S.

	Client:	Jason's Deli	REVISION INFO	11/05/2024	Original Rendering	AB	This rendering is the property of Anchor Sign, Inc. It is for the exclusive use of Anchor Sign, Inc. and the party which requested the rendering. It is an unpublished original drawing not to be distributed, reproduced or exhibited without the consent of Anchor Sign, Inc. Please contact your account manager with questions regarding this statement.
	Site #:	JD-54					
	Address:	149 Arnould Boulevard					
		Lafayette, LA 70506					
			 1.800.213.3331				